

TEL: 773977786- 771017677

الملاحظات الانشائية

السقف

- اجهاد الخضوع للحديد يجب ان لا يقل عن 4200 كجم/سم² للجبور و-2800 كجم/سم² للكانات والاعصاب
- يجب ان لا تقل كمية الاسمنت في الخرسانة المسلحة للسقف عن 300 كجم في المتر المكعب الواحد
- يجب ان لا تقل مقاومة الخرسانة للضغط بعد 28 يوم عن 210 كجم/سم²
- سمانة البلاطة المصممة لا تزيد عن 10 سم وحديد التسليح 5 قطر 8 مم لكل متر في الاتجاهين
- يتم عمل حديد الفرش والغطاء من تحت حديد الاعصاب العلوي
- يتم تكتيش نهاية أطراف حديد الجسور العلوي والسفلي وذلك عند أطراف السقف فوق الأعمدة بطول من 10 إلى 20 سم
- يتم الالتزام باتجاهات الاعصاب وبحسب المخططات
- يتم تربيط جميع كانات الجسور الرئيسية وكانات الاعصاب تربيط كامل
- يتم قص كانات الجسور الرئيسية بارتفاع 23 سم وكانات الاعصاب بارتفاع 25 سم
- يتم رص البلك بطريقة فنية بحيث تكون الفتحات من الداخل ويتم ترك فراغ ما بين البلك وحديد الجسور الرئيسية بمقدار 15 سم
- يتم عمل بسكوت اسمنتى سمكة 2.5 سم اسفل حديد الجسور الرئيسية واسفل جسور الاعصاب و اسفل حديد الفرش والغطاء
- يتم استدعاء الكهربائي والسباك لعمل التأسيسات المطلوبة بعد تنفيذ حديد الجسور الرئيسية للسقف وقبل عمل جسور الاعصاب
- لا تزيد المسافة بين قوائم الدعم للسقف عن 60 سم
- يتم التأكد من راسية جوانب الشدة الخشبية بحيث تكون قائمة ويتم تثبيتها تثبيتاً جيداً
- يتم عمل اختبار الكسر لمكعبات الخرسانة الجاهزة لضمان مقاومة الخرسانة التصميمية وبإشراف المهندس
- المكتب المصمم غير مسئول في حالة عدم الإشراف

اسم المالك/ جبران المخرفي

معماري

م / عبدالله بينون --- م / نوح القاضي

تصميم

م / انشائي وضاح صلاح

اسم اللوحه


سقف الدور الارضي

01:26:00 2025/12/23

ST-111 رقم AS مقاييس 14/01/2025 التاريخ

جدول تسليح الجسور والاعصاب

ابعاد الجسور		التسليح السفلي		التسليح العلوي		الكانات	
رمز الجسر	عرض (m)	ارتفاع (m)	المستمر	المكسح	المستمر	اضافي	وسط الجسر
B1	0.20	0.30	2Φ16	1Φ16	2Φ14	-----	1Φ8@20cm
B2	0.20	0.30	2Φ16	-----	2Φ14	-----	1Φ8@20cm
HB1	0.80	0.30	6Φ16	5Φ16	7Φ14	6Φ16	2Φ8@15cm
HB2	0.80	0.30	6Φ16	-----	10Φ18	-----	1Φ8@15cm
HB3	0.70	0.30	4Φ16	3Φ16	6Φ14	-----	2Φ8@15cm
HB4	0.70	0.30	4Φ16	3Φ16	6Φ14	-----	2Φ8@15cm
HB5	0.60	0.30	4Φ16	2Φ16	5Φ14	-----	1Φ8@15cm
HB6	0.60	0.30	3Φ16	2Φ16	5Φ14	-----	1Φ8@15cm
HB7	0.40	0.30	3Φ16	-----	3Φ14	-----	1Φ8@20cm
HB8	0.30	0.30	3Φ16	-----	3Φ14	-----	1Φ8@20cm
K1	0.80	0.30	6Φ16	-----	14Φ18	-----	3Φ8@10cm
K2	0.80	0.30	6Φ16	-----	10Φ18	-----	3Φ8@10cm
K3	0.80	0.30	6Φ16	-----	8Φ16	-----	2Φ8@15cm
K4	0.60	0.30	4Φ16	-----	5Φ14	-----	1Φ8@15cm
R1	0.12	0.30	2Φ12	-----	2Φ10	-----	1Φ8@20cm
R2	0.12	0.30	2Φ10	-----	2Φ12	-----	1Φ8@20cm
R3	0.12	0.30	2Φ10	-----	2Φ10	-----	1Φ8@20cm

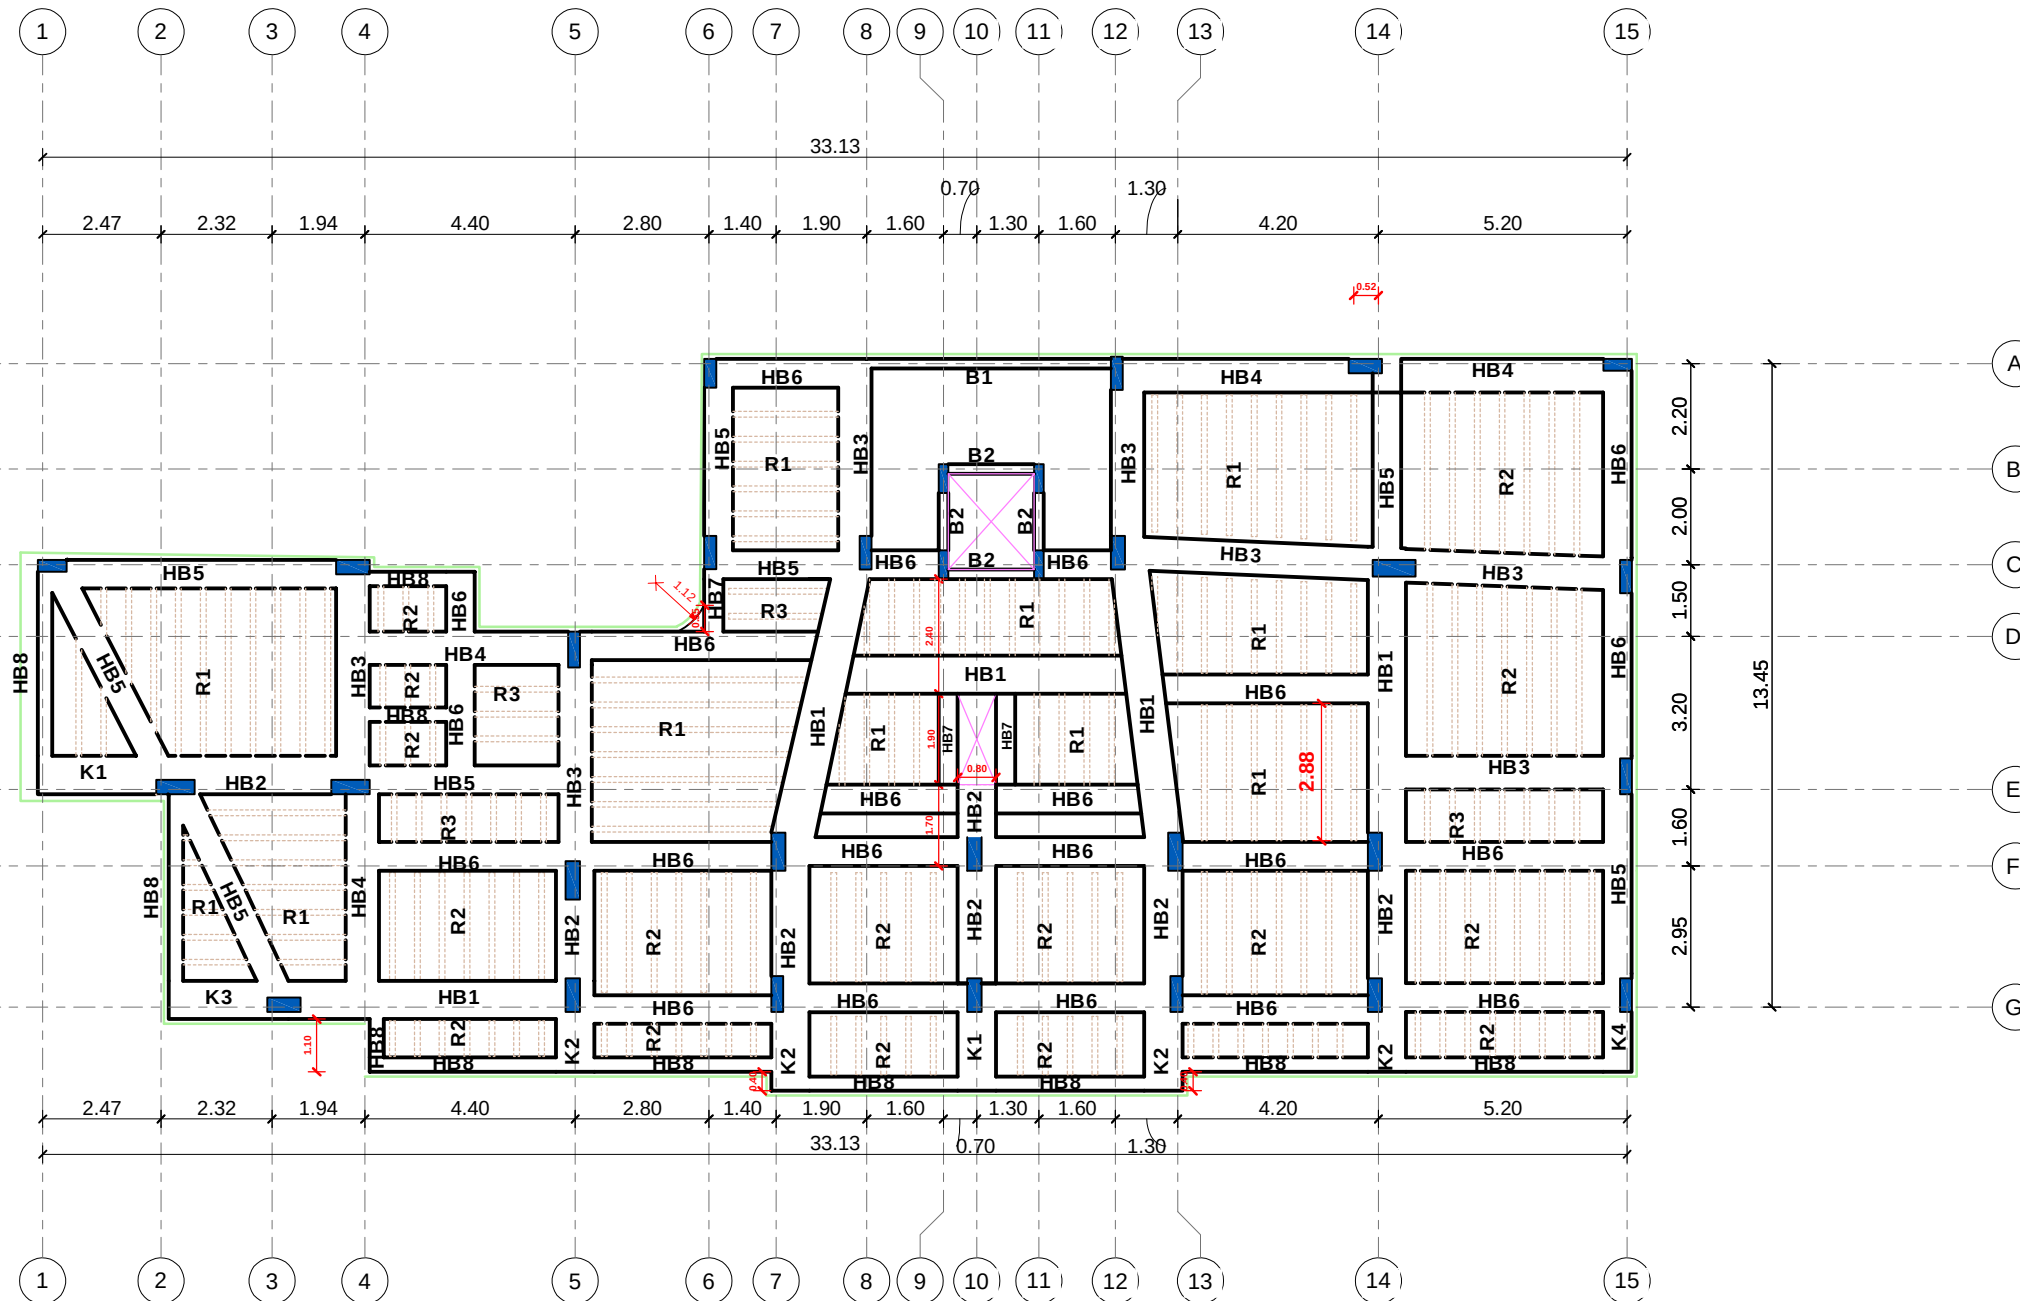

سقف الدور الارضي
1: 75

