


المخططات التنفيذية

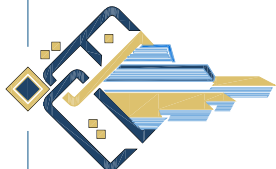


مكتب تمكين للهندسة
والمقاولات

T- 773977786 - 771017677 -
تخصصنا في استشارات هندسية - مقاولات - حساب كميات -
رفع مساحي - كروني دي - تخطيط حضري .

جدول التوافيق	
الرمز	الوصف الأرضيات الخشبية
ملاحظات	
W0	حسب المخططات التفصيلية للأجزاء
W1	-
W2	-
W3	حسب المخططات التفصيلية للأجزاء
W4	-
W5	-
WK	حسب المخططات التفصيلية للأجزاء
WB	-
WS	-
W1	-

جدول الأبواب	
الرمز	الوصف الأرضيات
ملاحظات	
D1	أبواب الخشب ضد الماء بقطب
D2	أبواب الخشب ضد الماء بقطب
D3	أبواب الخشب ضد الماء بقطب
D4	أبواب الخشب ضد الماء بقطب
D5	أبواب الخشب ضد الماء بقطب
D6	أبواب الخشب ضد الماء بقطب

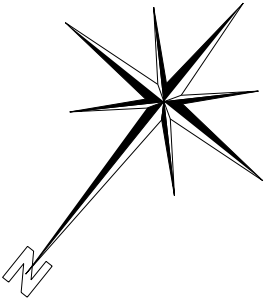

المخططات التنفيذية

مسقط البدر وم


الملك/ الاخ جبران المخرفي


اسم العرشي
مبنى سكني حسيه

تصميم
م: عبد الله بينون
م: نوح الفاضي
م: عبد الرحمن المغربي

الطوبوغرافيا
مقياس الرسم 1/100
تاريخ المخطط

مساحه البناء للدور الارضي 375.77 متر مربع

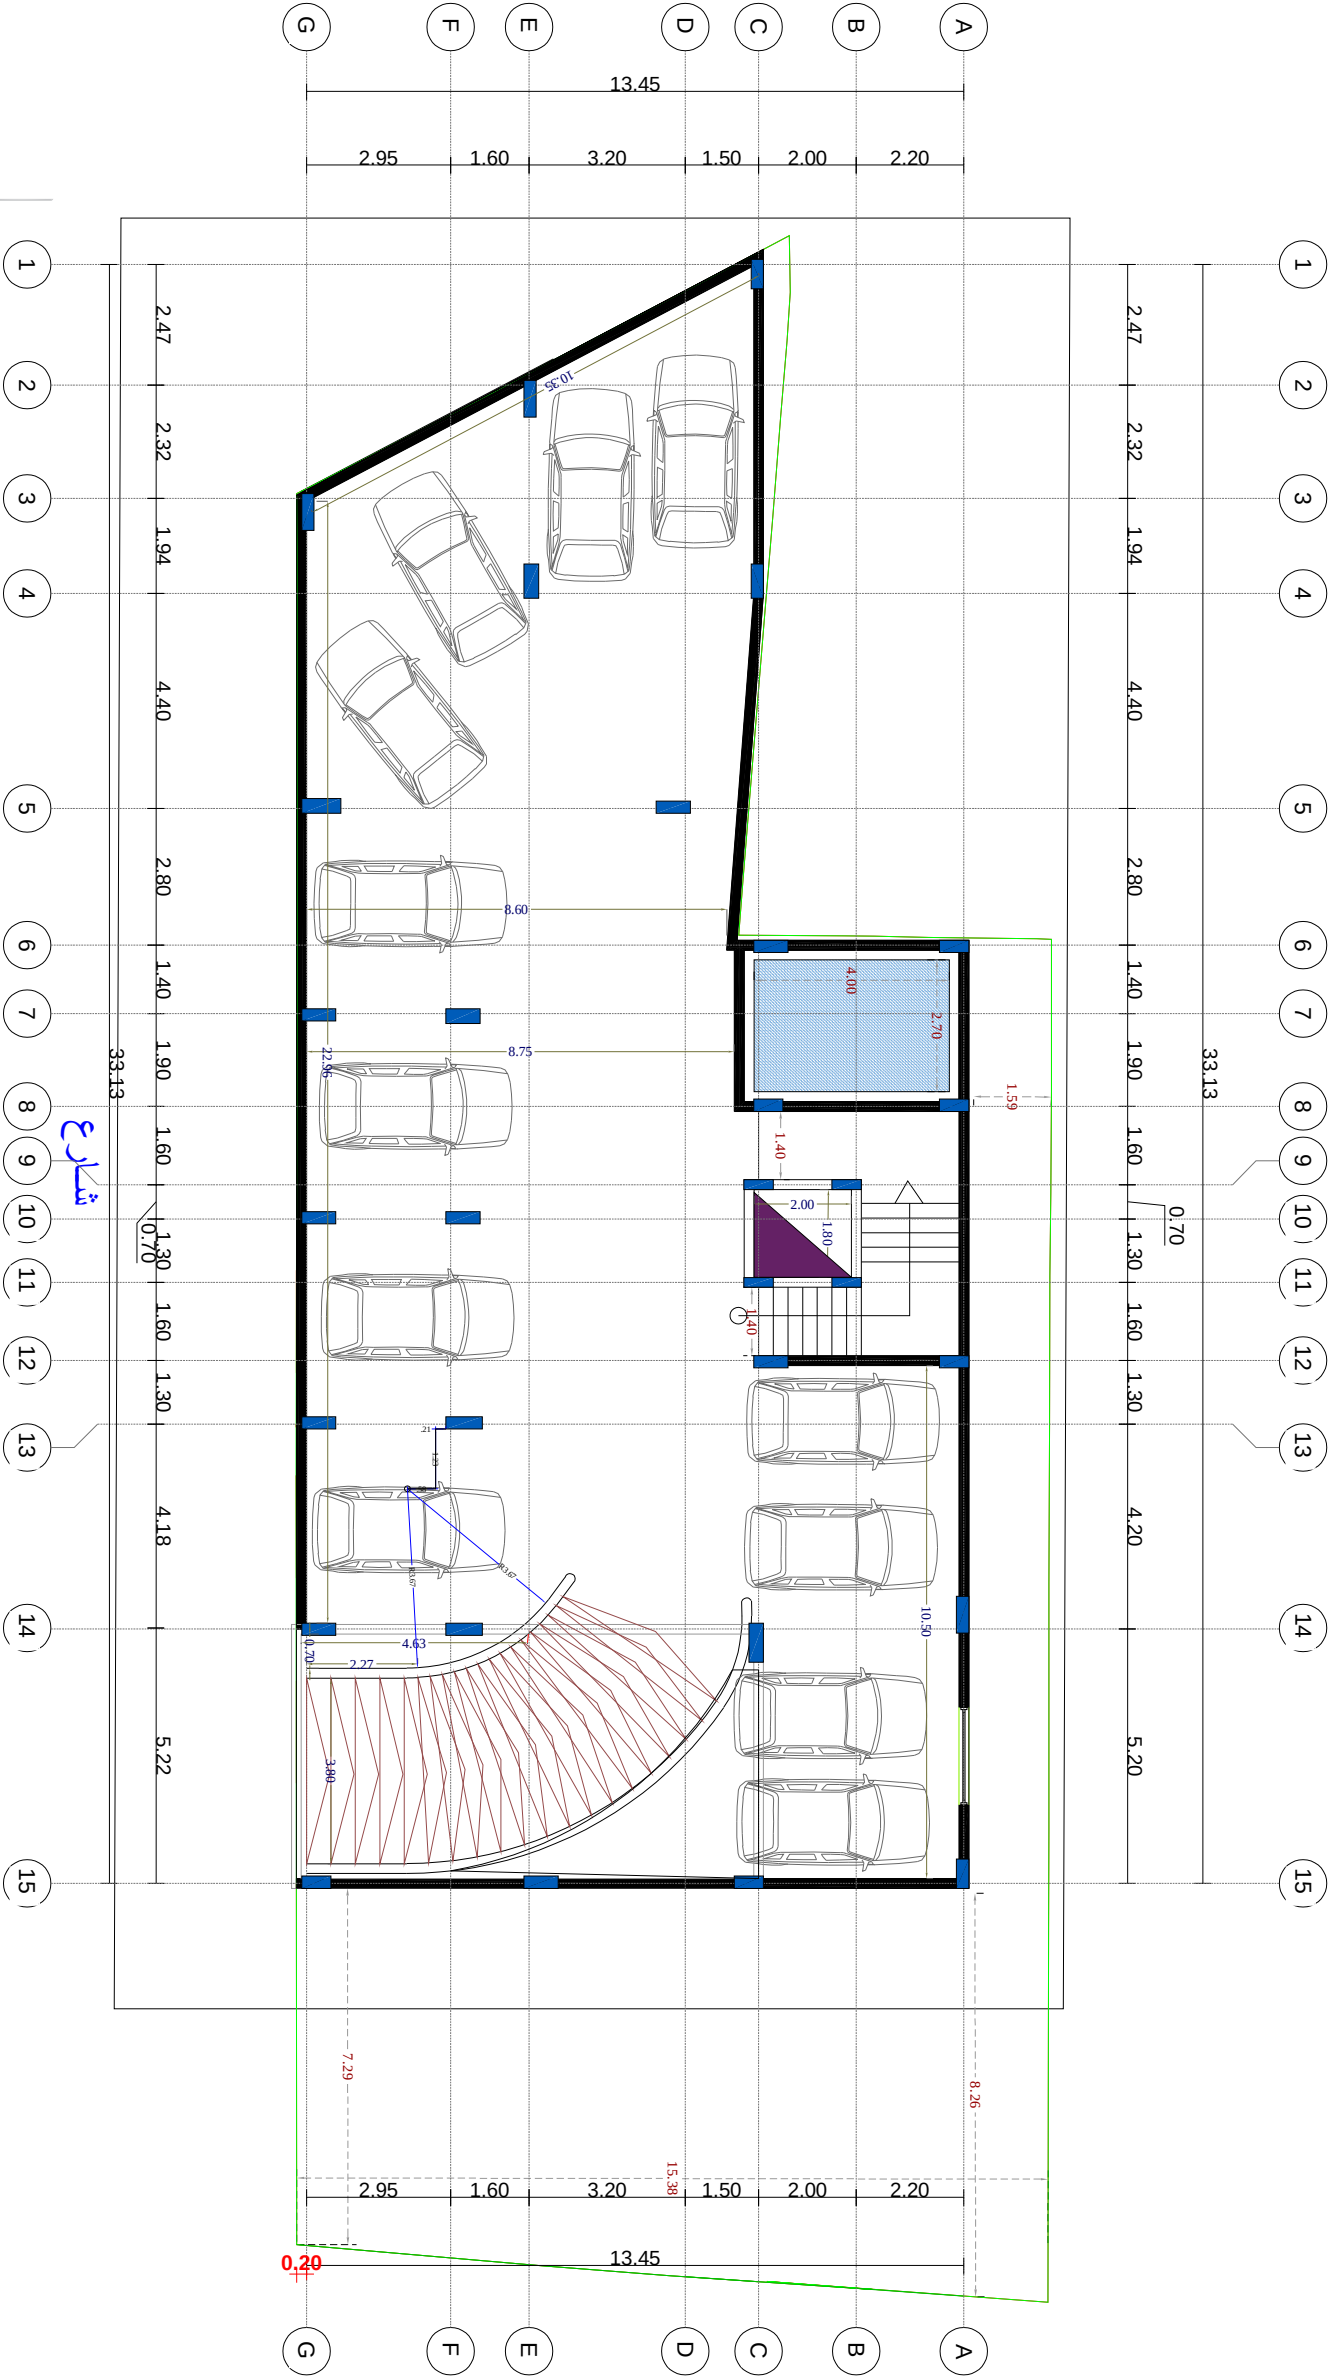

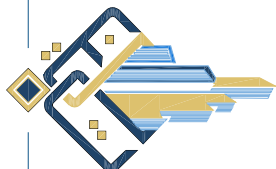

مكتب تمكين للهندسة
والمقاولات


T- 773977786 - 771017677 -
تصاميم واستشارات هندسية - مقاولات - حديد كبريت -
رفع مساحي - تزيدي دي - تخطيط حضري .

جدول التوافيق

ملاحظات	الرمز	المرصع	الارتفاع	الطبقة
حصب الحفظات التفتيزية لالوجهات	W0	-	-	-
حصب الحفظات التفتيزية لالوجهات	W1	-	-	-
حصب الحفظات التفتيزية لالوجهات	W2	-	-	-
حصب الحفظات التفتيزية لالوجهات	W3	-	-	-
حصب الحفظات التفتيزية لالوجهات	W4	-	-	-
حصب الحفظات التفتيزية لالوجهات	W5	-	-	-
حصب الحفظات التفتيزية لالوجهات	WK	-	-	-
حصب الحفظات التفتيزية لالوجهات	WB	-	-	-
حصب الحفظات التفتيزية لالوجهات	WS	-	-	-
حصب الحفظات التفتيزية لالوجهات	W1	-	-	-

جدول الارتفاع

ملاحظات	الرمز	المرصع	الارتفاع
الارتفاع منسوب مياه جاذب	D1	2.2	1
الارتفاع منسوب مياه جاذب	D2	2.2	0.8
الارتفاع منسوب مياه جاذب	D3	2.2	0.9
الارتفاع منسوب مياه جاذب	D4	2.2	1.60
الارتفاع منسوب مياه جاذب	D5	-	-
الارتفاع منسوب مياه جاذب	D6	3.00	3

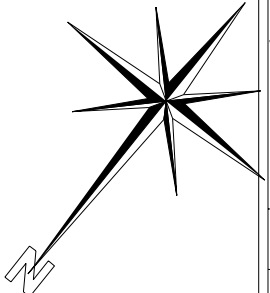

اسم الوحدة
المخططات التنفيذية

مسقط الدور الارضي

الملك/
الاخ جبران المخرفي


اسم الشارع
مبنى سكني حسيه


تصميم

م: عبد الله بينون
م: نوح الفاضي
م: عبد الرحمن المغربي

المقياس
1/100
نقش الرس
1/100
نقش الرس

مساحة البناء للدور الارضي 373.15 متر مربع

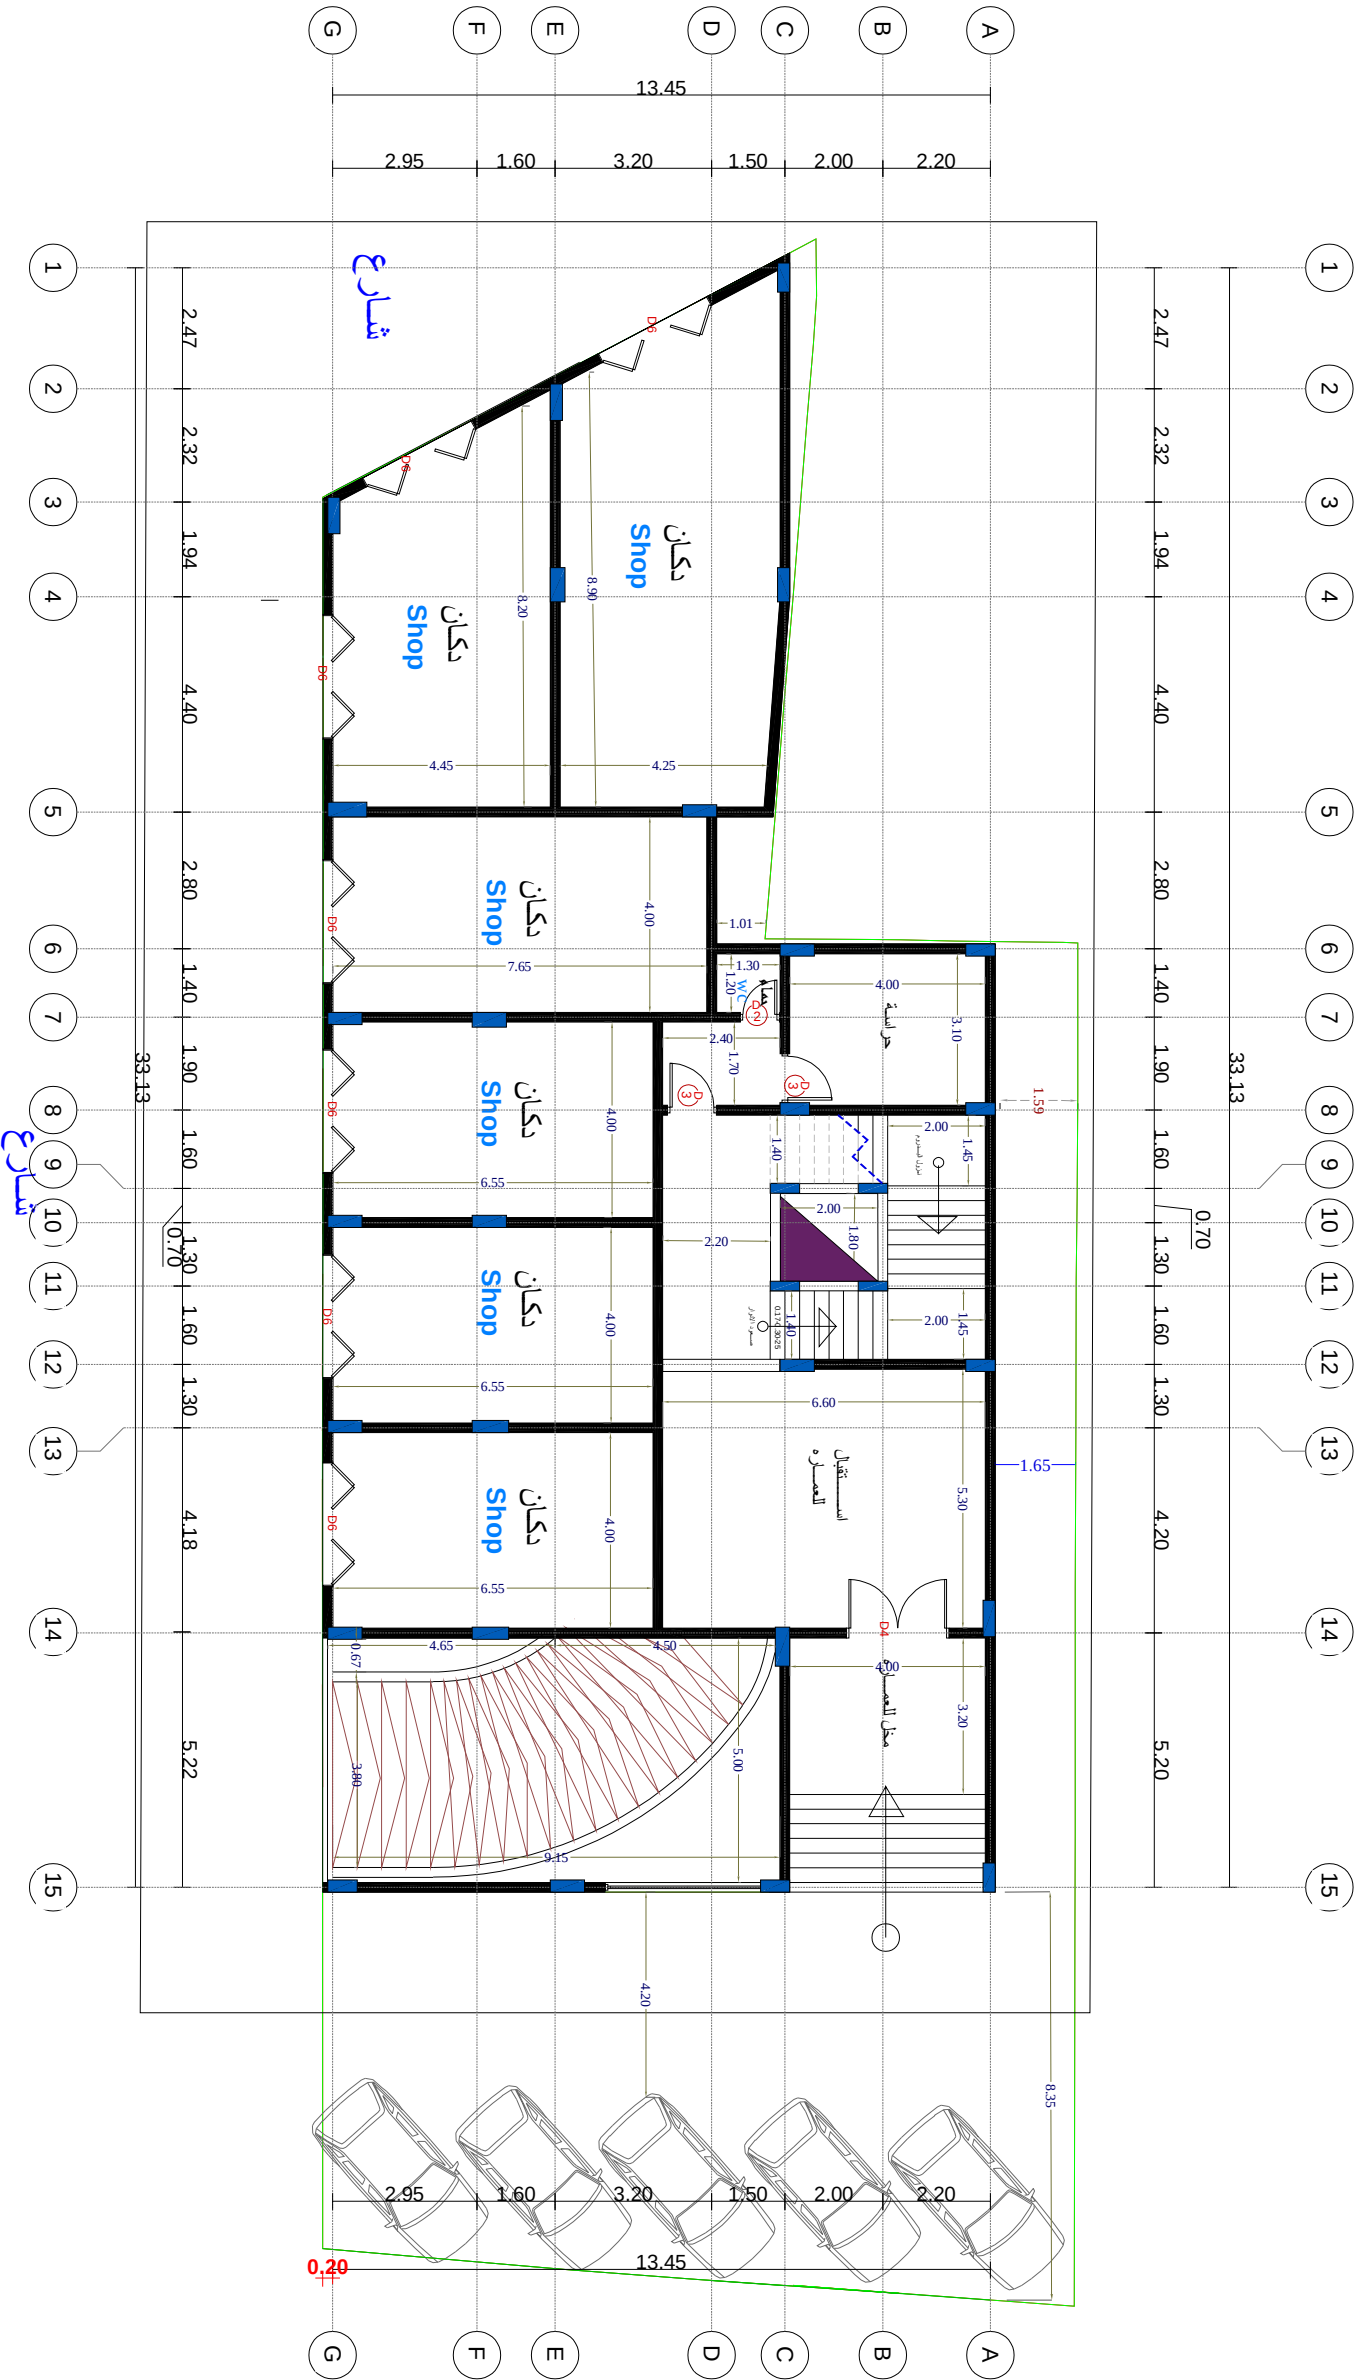

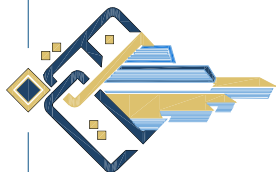

مكتب تمكين للهندسة
والمقاولات


T- 773977786 - 771017677 -
تصاميم واستشارات هندسية - مقاولات - مكتب كبريات -
رفع مساحي - تزيدي دي - تخطيط حضري .

جدول التوافق

ملاحظات	الرمز	الرمز الآخر	الجدول
حساب الحفظات للتوزيع	-	-	W0
حساب الحفظات للتوزيع	-	-	W1
حساب الحفظات للتوزيع	-	-	W2
حساب الحفظات للتوزيع	-	-	W3
حساب الحفظات للتوزيع	-	-	W4
حساب الحفظات للتوزيع	-	-	W5
حساب الحفظات للتوزيع	-	-	WK
حساب الحفظات للتوزيع	-	-	WB
حساب الحفظات للتوزيع	-	-	WS
حساب الحفظات للتوزيع	-	-	W1

جدول الأبعاد

ملاحظات	الرمز	الرمز الآخر	الجدول
حساب الأبعاد	2.2	1	D1
حساب الأبعاد	2.2	0.8	D2
حساب الأبعاد	2.2	0.9	D3
حساب الأبعاد	2.2	1.60	D4
حساب الأبعاد	-	-	D5
حساب الأبعاد	3	3.00	D6

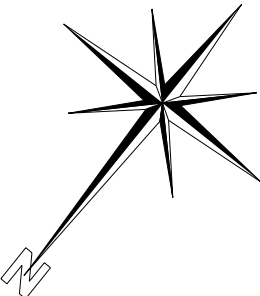

اسم الوحدة
المخططات التنفيذية

مسقط الدور الاول

الملك/
الاخ/ جبران المخرفي


اسم المشروع
مبنى سكني حصة

تصميم
م: عبد الله بينون


م: نوح الفاضي
م: عبد الرحمن المغربي

الموقع
مقياس الرسم 1/100
تاريخ المخطط

مساحة البناء للدور المتكرر 424.76 متر مربع

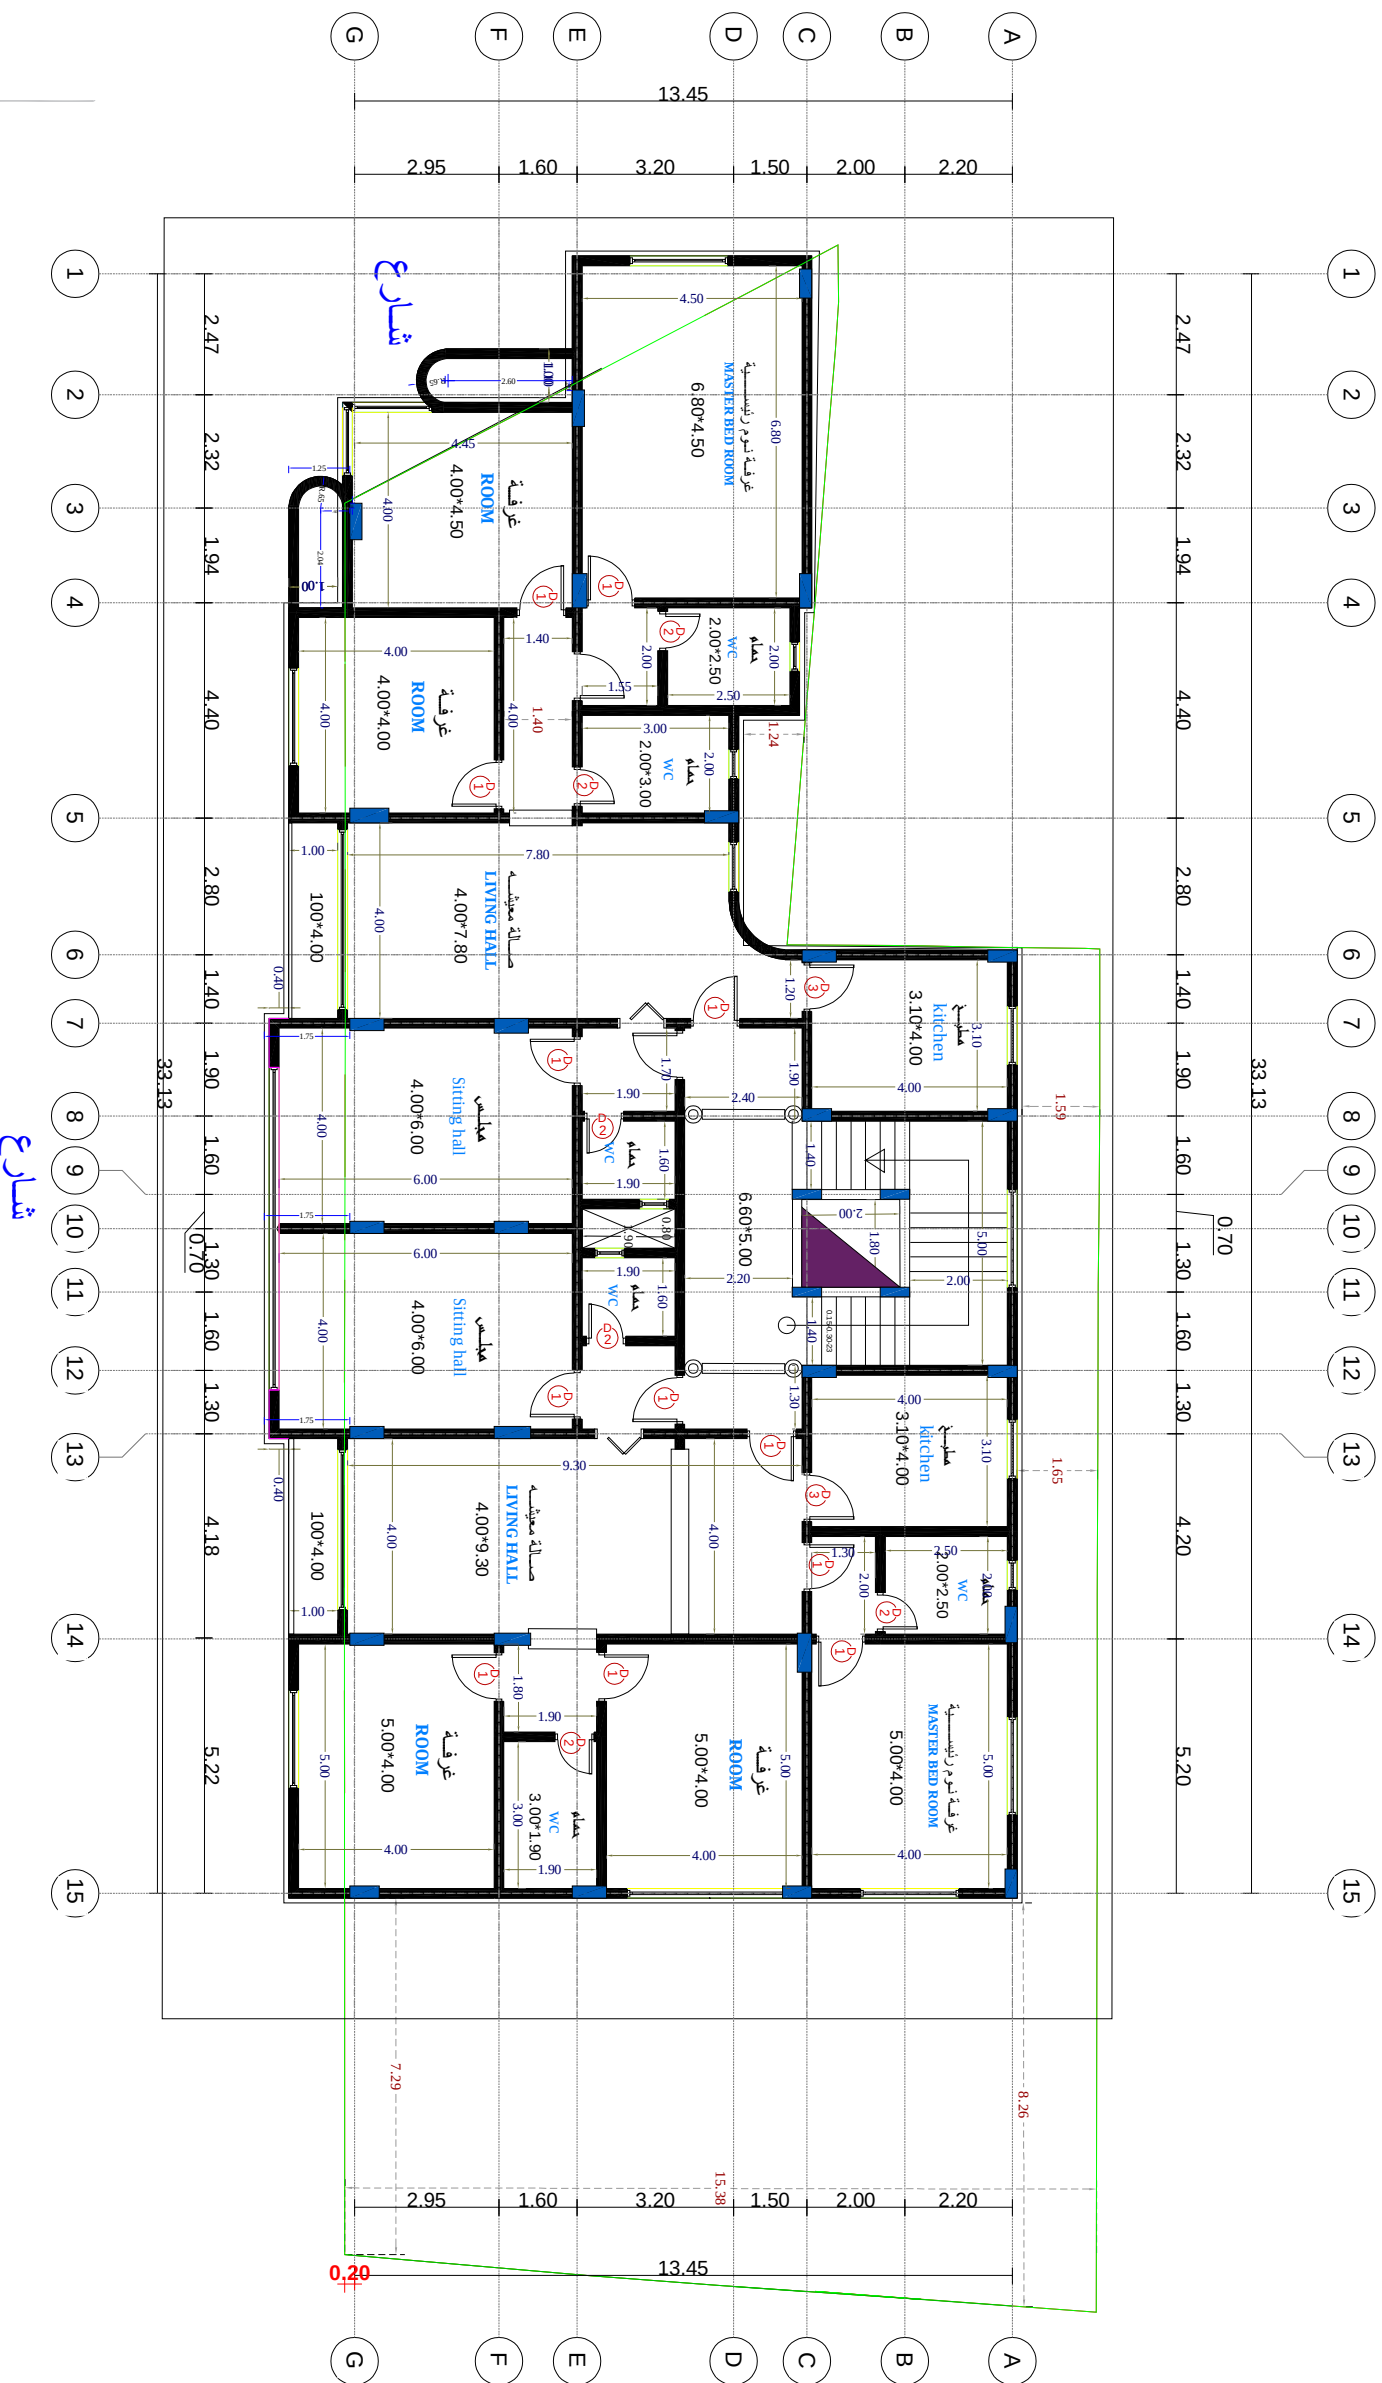

مساحة البناء للدور المتكرر 424.76 متر مربع

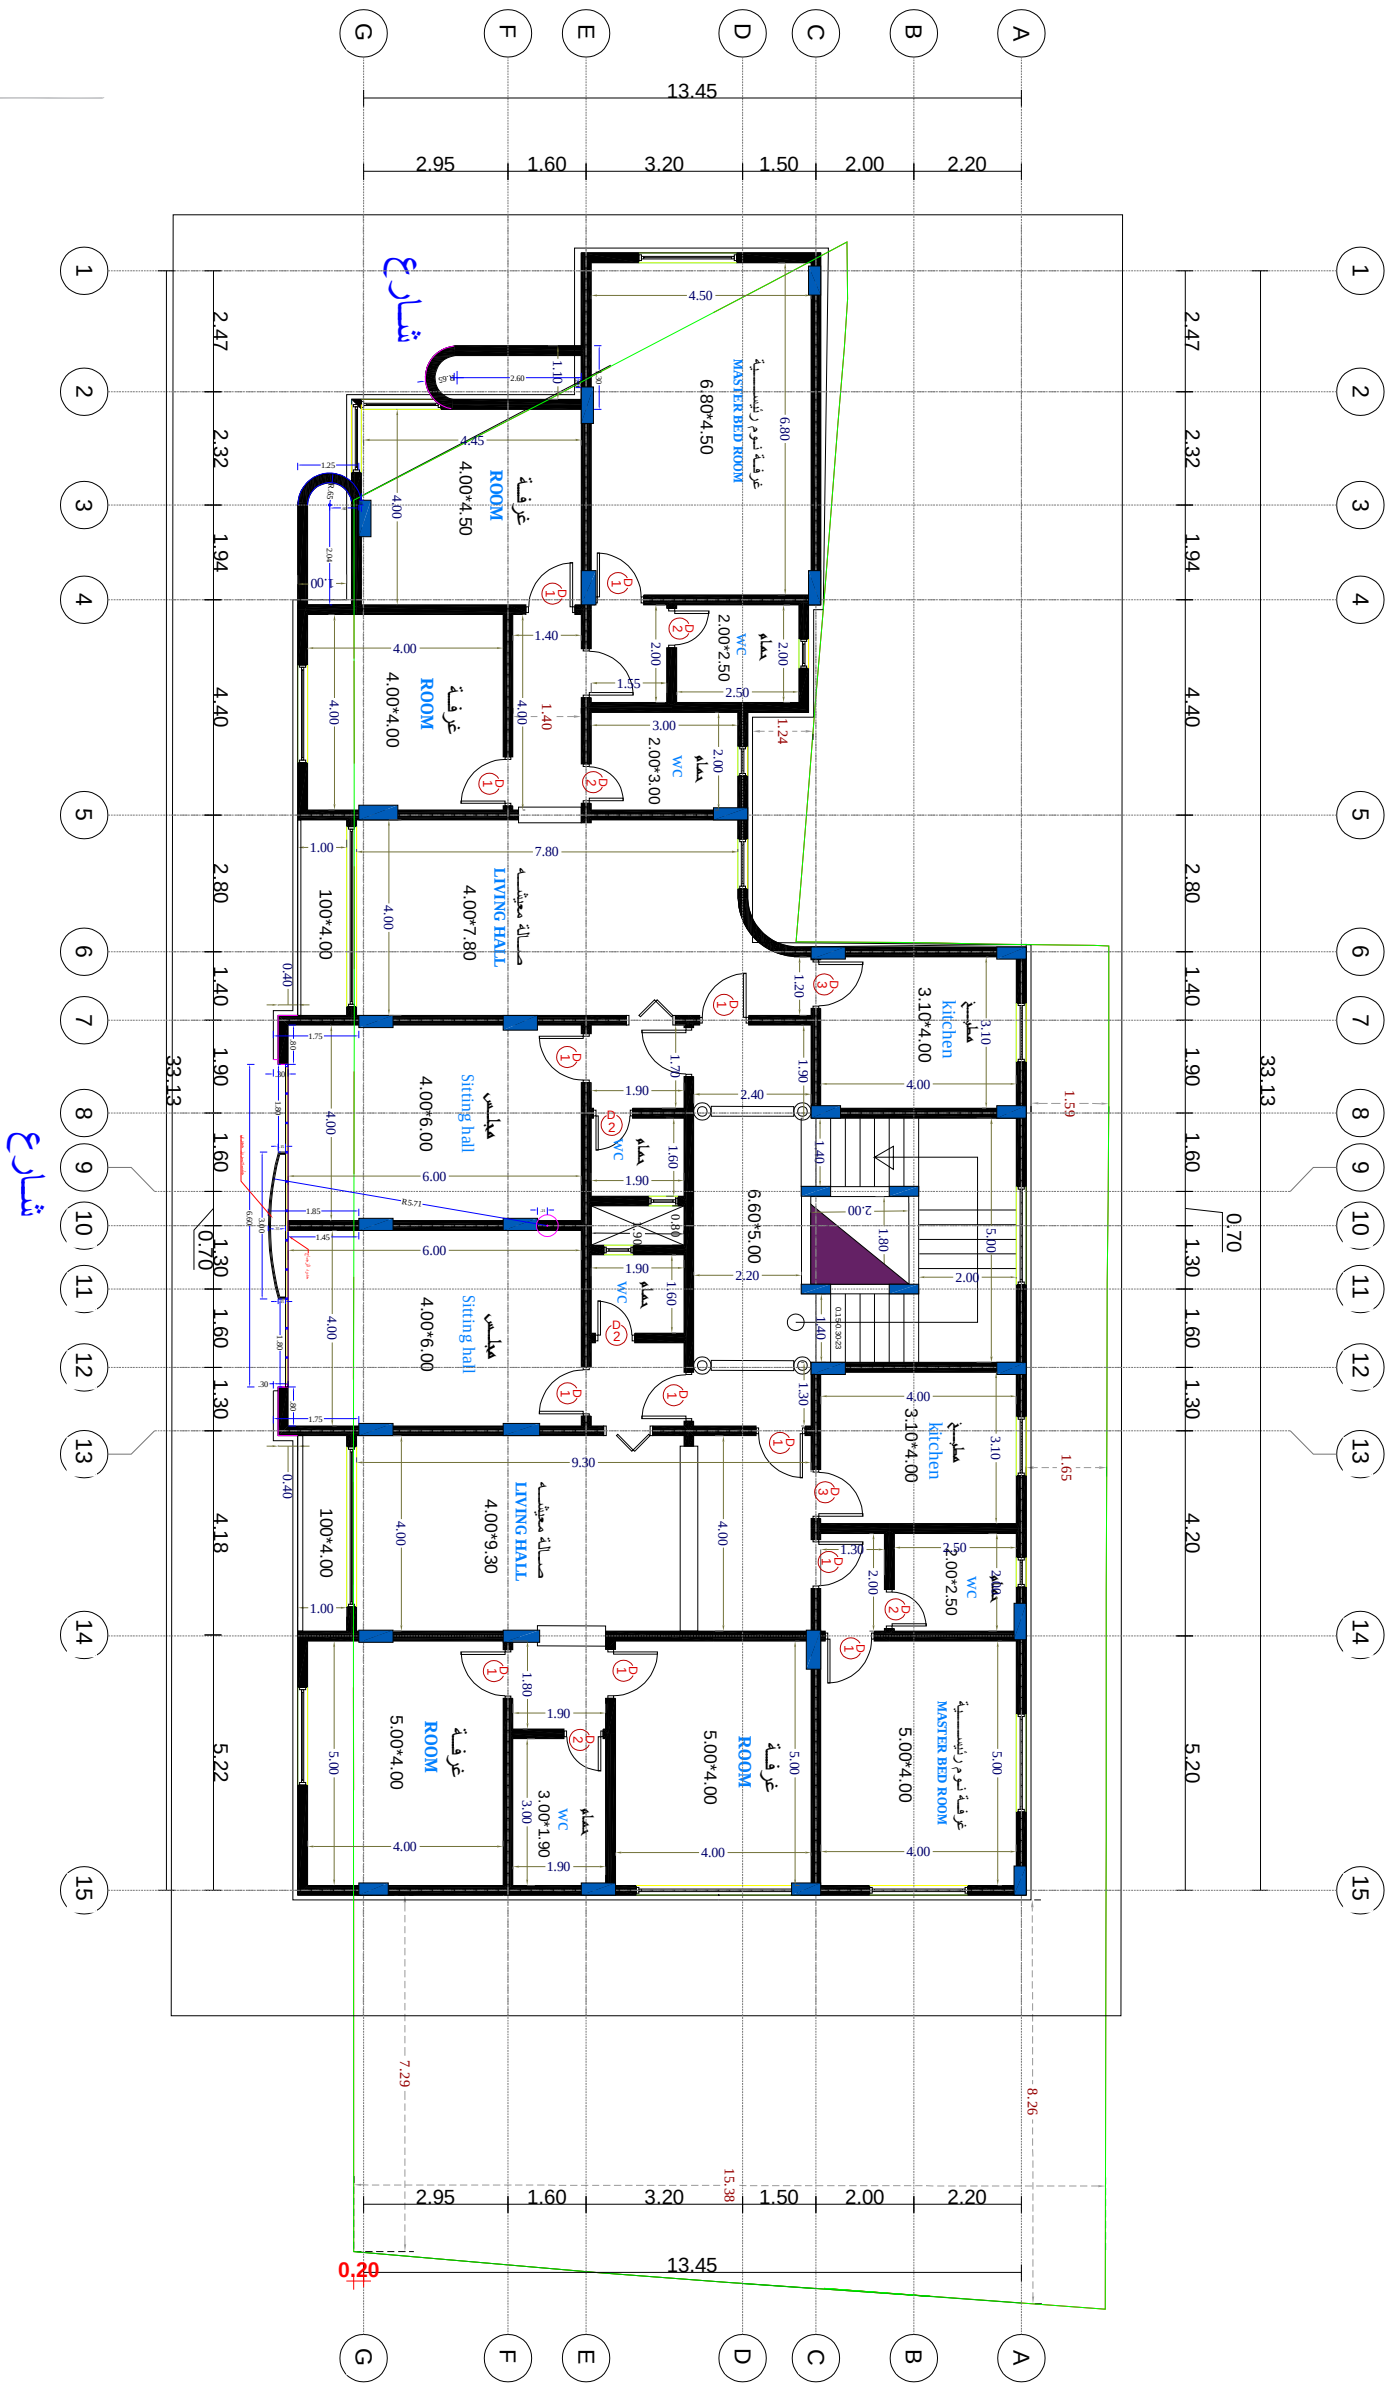

مكتب تمكين للهندسة والمقاولات

T- 773977786 - 771017677 -

تصاميم واستشارات هندسية - مقاولات - خدمات كبرى -

رفع مساحي - تزيدي دي - تخطيط حضري -

جدول التوافيق	
ملاحظات	الرمز
حسب المخططات التفصيلية	W0
حسب المخططات التفصيلية للأجزاء	W1
حسب المخططات التفصيلية للأجزاء	W2
حسب المخططات التفصيلية للأجزاء	W3
حسب المخططات التفصيلية للأجزاء	W4
حسب المخططات التفصيلية للأجزاء	W5
حسب المخططات التفصيلية للأجزاء	WK
حسب المخططات التفصيلية للأجزاء	WB
حسب المخططات التفصيلية للأجزاء	WS
حسب المخططات التفصيلية للأجزاء	W1

جدول الأبعاد	
ملاحظات	الرمز
أبعاد الغرف حسب المخطط	D1
أبعاد الحمامات حسب المخطط	D2
أبعاد المطابخ حسب المخطط	D3
أبعاد الشقق حسب المخطط	D4
أبعاد مساحات التجميع	D5
أبعاد مساحات التجميع	D6

اسم الوحدة

المخططات التنفيذية

مسقط الدور الثاني

الإخ/ جبران المخرفي

المالك/

اسم المشروع

مبنى سكني - مسند

تصميم

م: عبد الله بيلون


م: نوح الفاضي

م: عبد الرحمن المغربي


الموقع

مقياس الرسم 1/100

نوع المخطط

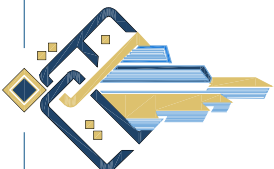

مساحة البناء للدور المتكرر 424.76 متر مربع

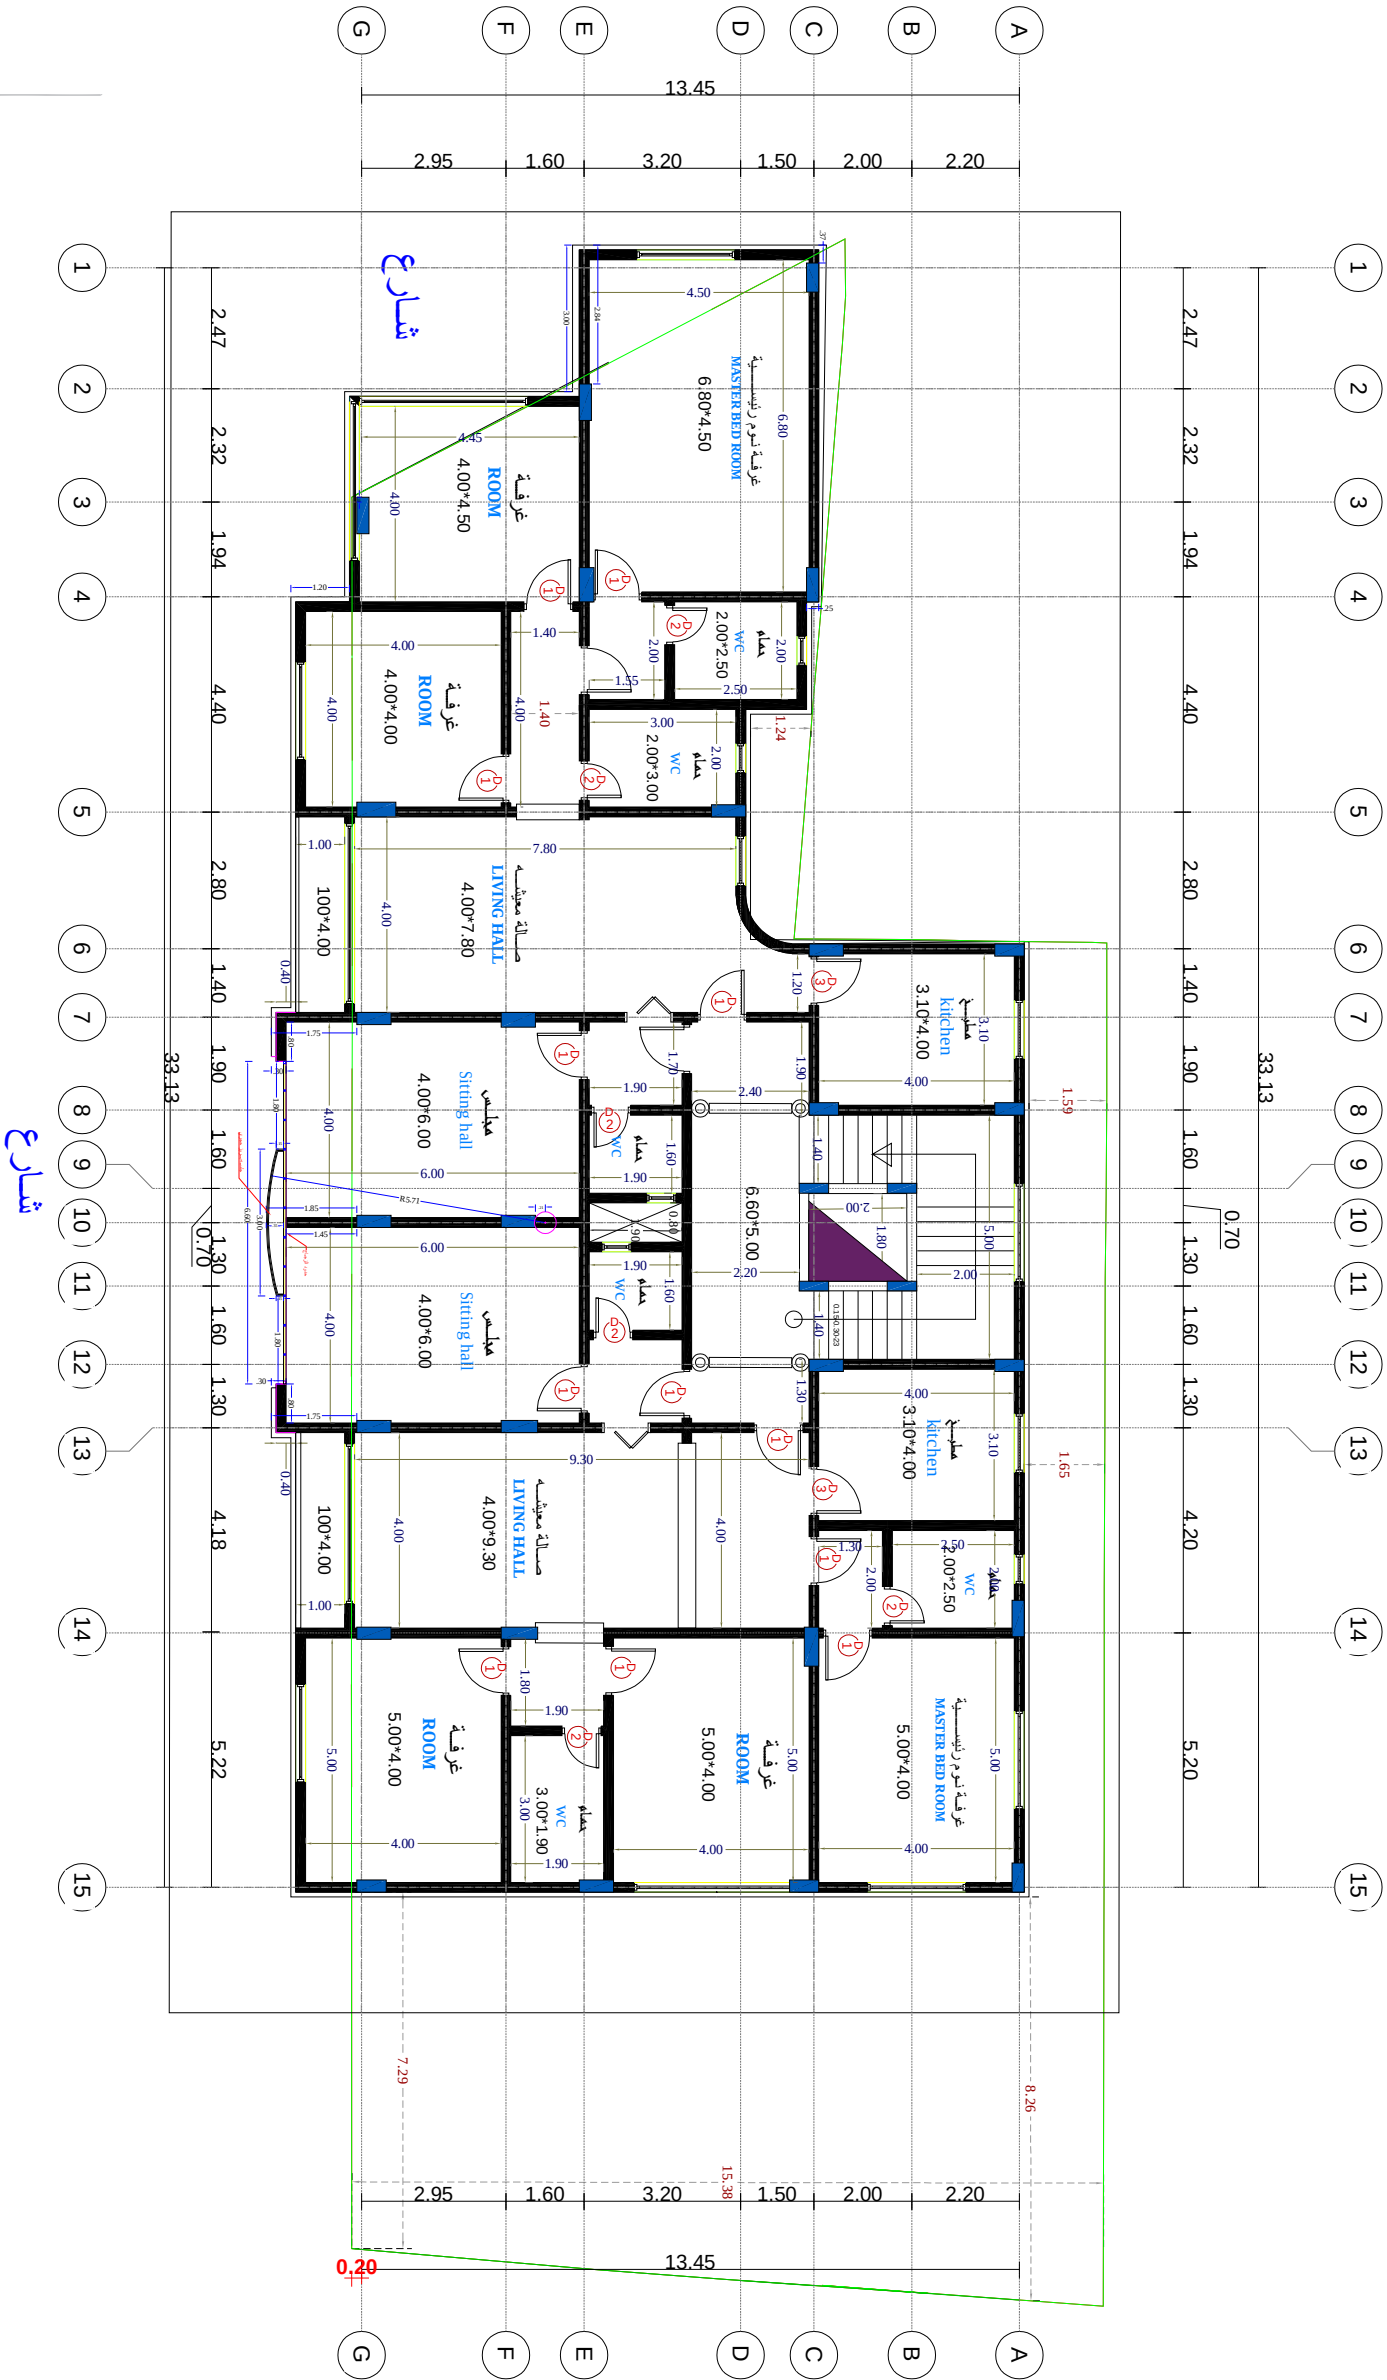


مكتب تمكين للهندسة والمقاولات
T- 773977786 - 771017677 -
تصاميم واستشارات هندسية - مقاولات - حديد كبريت -
رفع مساحي - تزيدي دي - تخطيط حضري .

جدول التوافيق

ملاحظات	الرمز	الرمز الأرفق الحسية
حبيب الحفظات التفتير	-	W0
حبيب الحفظات التفتير	-	W1
حبيب الحفظات التفتير	-	W2
حبيب الحفظات التفتير	-	W3
حبيب الحفظات التفتير	-	W4
حبيب الحفظات التفتير	-	W5
حبيب الحفظات التفتير	-	WK
حبيب الحفظات التفتير	-	WB
حبيب الحفظات التفتير	-	WS
حبيب الحفظات التفتير	-	W1

جدول الإبراب

ملاحظات	الرمز	الرمز الأرفق الحسية
حبيب الحفظات التفتير	-	D1
حبيب الحفظات التفتير	-	D2
حبيب الحفظات التفتير	-	D3
حبيب الحفظات التفتير	-	D4
حبيب الحفظات التفتير	-	D5
حبيب الحفظات التفتير	-	D6

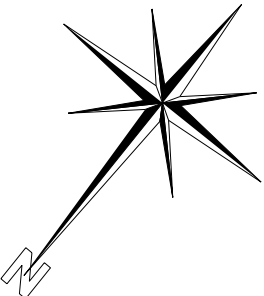

المخططات التنفيذية


مسقط الدور الثالث

الإخ/ جبران المخرفي

مبنى سكني حسيه

تصميم
م: عبد الله بيلون
م: نوح الفاضي
م: عبد الرحمن المغربي

الموقع
المقياس الرسم 1/100
تاريخ المخطط

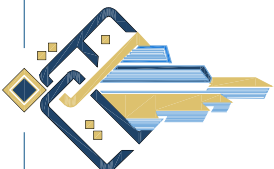


مكتب تمكين للهندسة
والمقاولات

T- 773977786 - 771017677 -

تصاميم واستشارات هندسية - مقاولات - خدمات كبرى -
رفع مساحي - تزيدي دي - تخطيط حضري -

جدول التوافيق	
الرمز	الوصف أو تسمية الحصة
ملاحظات	
W0	حصة المخططات التنفيذية للأجوات
W1	-
W2	حصة المخططات التنفيذية للأجوات
W3	-
W4	حصة المخططات التنفيذية للأجوات
W5	-
WK	حصة المخططات التنفيذية للأجوات
WB	-
WS	حصة المخططات التنفيذية للأجوات
W1	-

جدول الأبعاد	
الرمز	الوصف أو تسمية الأبعاد
ملاحظات	
D1	2.2
D2	2.2
D3	2.2
D4	2.2
D5	2.2
D6	3.00

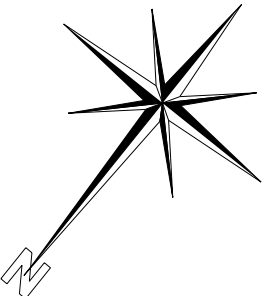

اسم الوحدة
المخططات التنفيذية

مسقط الدور الرابع


الملك/ **الإخ/ جبران المخرفي**

اسم الشارع
مبنى سكني - مسند

تصميم
م: عبد الله بيلون

م: نوح الفاضي

م: عبد الرحمن المغربي

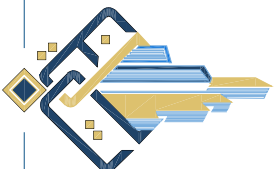

مكتب تمكين للهندسة
والمقاولات

T- 773977786 - 771017677 -


تصاميم واستشارات هندسية - مقاولات - خدمات كبريات -
رفع مساحي - تزيدي دي - تخطيط حضري -

جدول التوافق

ملاحظات	الرمز	الرمز الآخر	الجدول
حساب الحسابات التفصيلية	-	-	W0
حساب الحسابات التفصيلية	-	-	W1
حساب الحسابات التفصيلية	-	-	W2
حساب الحسابات التفصيلية	-	-	W3
حساب الحسابات التفصيلية	-	-	W4
حساب الحسابات التفصيلية	-	-	W5
حساب الحسابات التفصيلية	-	-	WK
حساب الحسابات التفصيلية	-	-	WB
حساب الحسابات التفصيلية	-	-	WS
حساب الحسابات التفصيلية	-	-	W1

جدول الإبراب

ملاحظات	الرمز	الرمز الآخر	الجدول
حساب الحسابات التفصيلية	-	-	D1
حساب الحسابات التفصيلية	-	-	D2
حساب الحسابات التفصيلية	-	-	D3
حساب الحسابات التفصيلية	-	-	D4
حساب الحسابات التفصيلية	-	-	D5
حساب الحسابات التفصيلية	-	-	D6

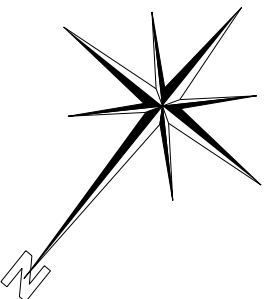

المخططات التنفيذية

مسقط الدور الخامس

الإخ/ جبران المخرفي

مبنى سكني - مسند

تصميم

م: عبد الله بيلون
م: نوح الفاضي
م: عبد الرحمن المغربي

الموقع

مساحة البناء للدور المتكرر 424.76 متر مربع

