

الشمال جار



دور مفتوح مكاتب تجارية

دور مفتوح مكاتب

تجارية

صالة توزيع

الجنوب جار

الأسقاط الأفقي للدور المسروق

جدول نماذج النوافذ

الرمز	المقاسات العرض	المقاسات الارتفاع	الجلسة	المواصفات
W1	200	120	120	نوافذ الألمنيوم أبيض حليبي بزجاج 6 مم
W2	150	120	120	نوافذ الألمنيوم أبيض حليبي بزجاج 6 مم

جدول نماذج الأبواب والفتحات

الرمز	المقاسات العرض	المقاسات الارتفاع	المواصفات
D1	110	220	أبواب خشب ميرنيتي حشو فردتين ثلثين وثلاث.
D2	95	210	أبواب خشب حشو فردة واحدة للغرف.
D3	80	210	أبواب خشب حشو فردة واحدة للحمامات.
D4	120	220	أبواب حديد قيوكات رص مع النقشة فردتين
D5	277	290	أبواب حديد فردات رص أو حديد سحب

الجمهورية اليمنية
Sana'a R.of YEMEN
P.O.Box / 8425
Tele / 00967-01-226583
fax / 00967-01-239170

مكتب الهندسة المعمارية
AA-Hikmah Office.For Eng.

اسم المشروع

اسم المالك

نوع المخطط

اسم المخطط

مقياس الرسم

عمارة سكنية

الأخ / محمد فرحان أحمد الجثام

معماري

الأسقاط الأفقي للدور المسروق

رقم المخطط


4

1 : 100

الشمال جار



الغرب شارع مشترك

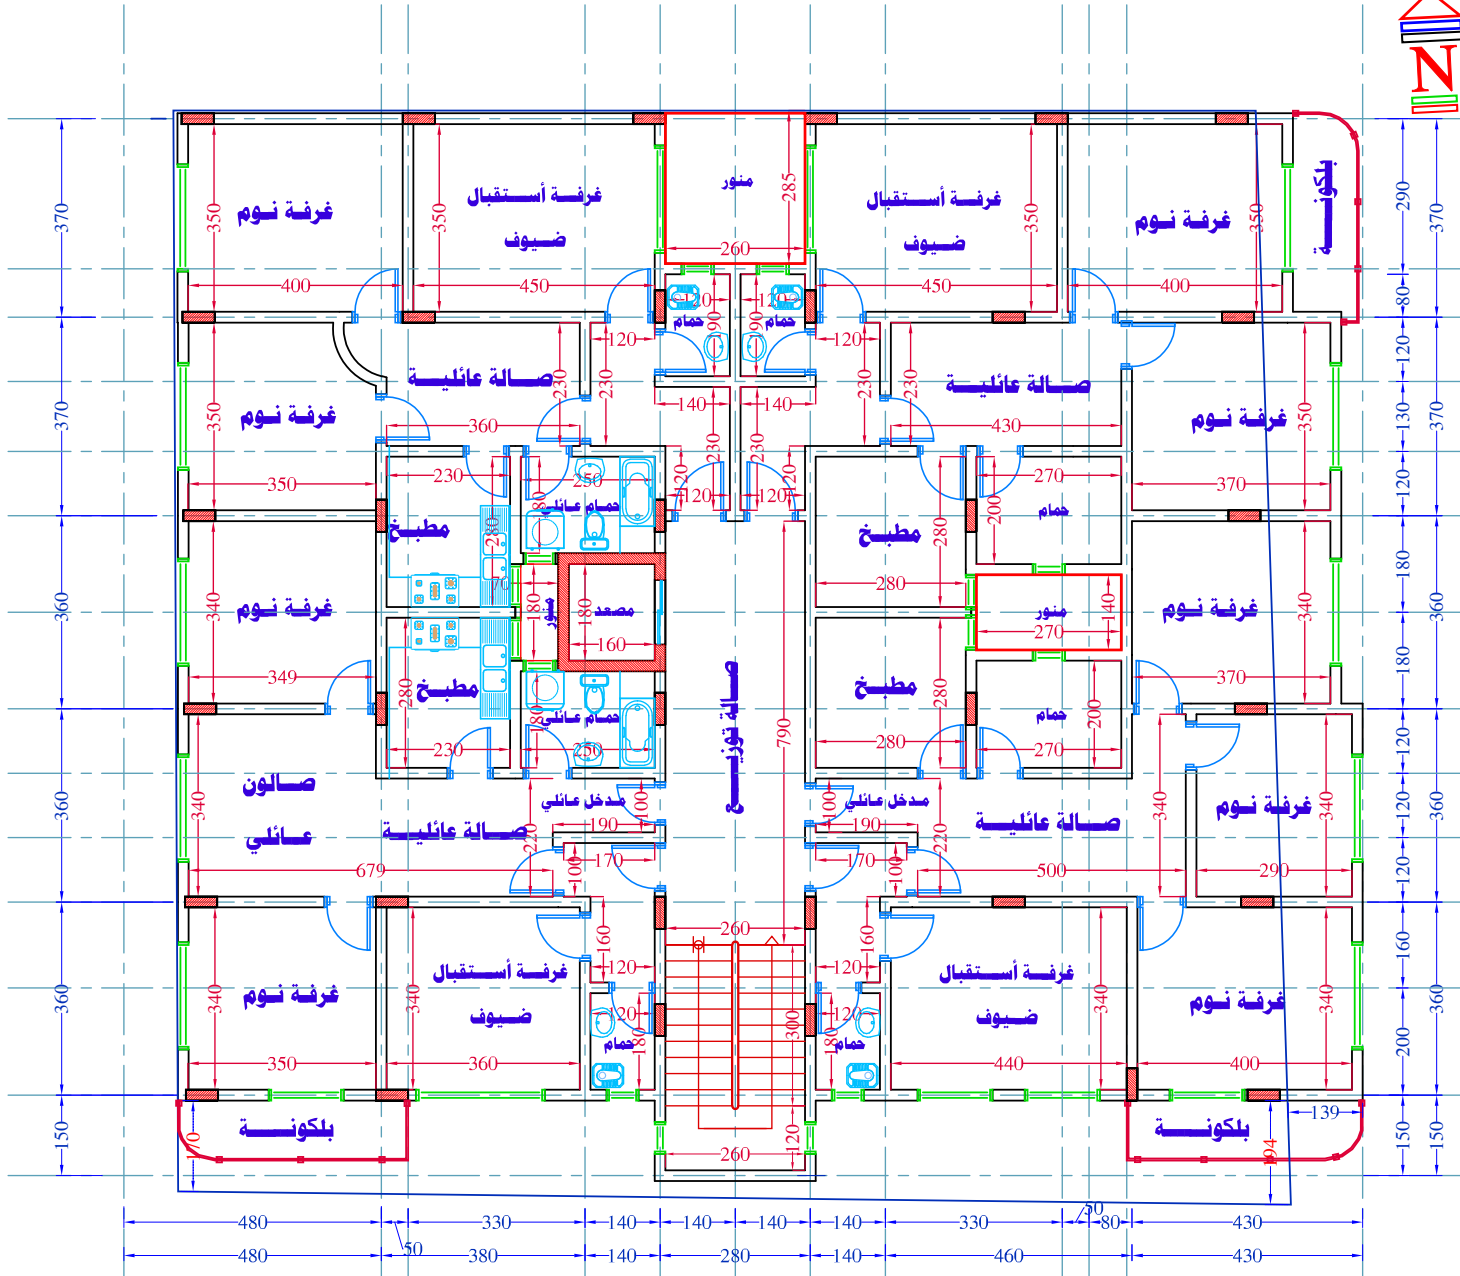

الجنوب جار

الأسقاط الأفقي للدور الثاني والمتكرر

جدول نماذج النوافذ

الرمز	المقاسات العرض الارتفاع	الجلسة	المواصفات
W1	200 180	60	نوافذ الألمنيوم أبيض حليبي بزجاج 6 مم
W2	150 180	60	نوافذ الألمنيوم أبيض حليبي بزجاج 6 مم
W3	140 180	60	نوافذ الألمنيوم أبيض حليبي بزجاج 6 مم
W4	100 100	100	نوافذ الألمنيوم أبيض حليبي بزجاج 6 مم
W5	60 60	140	نوافذ الألمنيوم أبيض حليبي بزجاج 6 مم
W6	60 200	60	نوافذ الألمنيوم أبيض حليبي بزجاج 6 مم

جدول نماذج الأبواب والفتحات

الرمز	المقاسات العرض الارتفاع	المواصفات
D1	95 210	أبواب خشب حشو فردة واحدة للغرف.
D2	90 210	أبواب خشب حشو فردة واحدة للمطابخ.
D3	80 200	أبواب خشب حشو فردة واحدة للحمامات.

الجمهورية اليمنية
Sana'a R. of YEMEN
P.O.Box / 8425
Tele / 00967-01-226583
fax / 00967-01-239170

مكتب الهندسة المعمارية
AA Hikmah Office. For Eng.

أسم المشروع	عمارة سكنية
أسم المالك	الأخ / محمد فرحان أحمد الجثام
نوع المخطط	معماري
أسم المخطط	الأسقاط الأفقي للدور الثاني والمتكرر
مقياس الرسم	1 : 100
رقم المخطط	5