منور التصريف بمقاس
260×285سم بهبوط 50سم
عن مستوى سقف المسروق

خط تصريف مجاري
معلق قطر 6هنش
داخل جسر خرسانة ساقط
مقاس 35 × 35سم

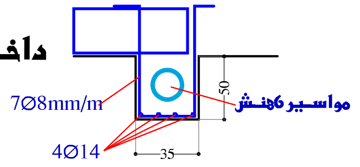

خط تصريف مجاري
معلق قطر 6هنش
داخل جسر خرسانة ساقط
مقاس 35 × 35سم

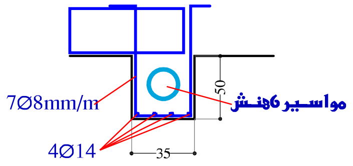

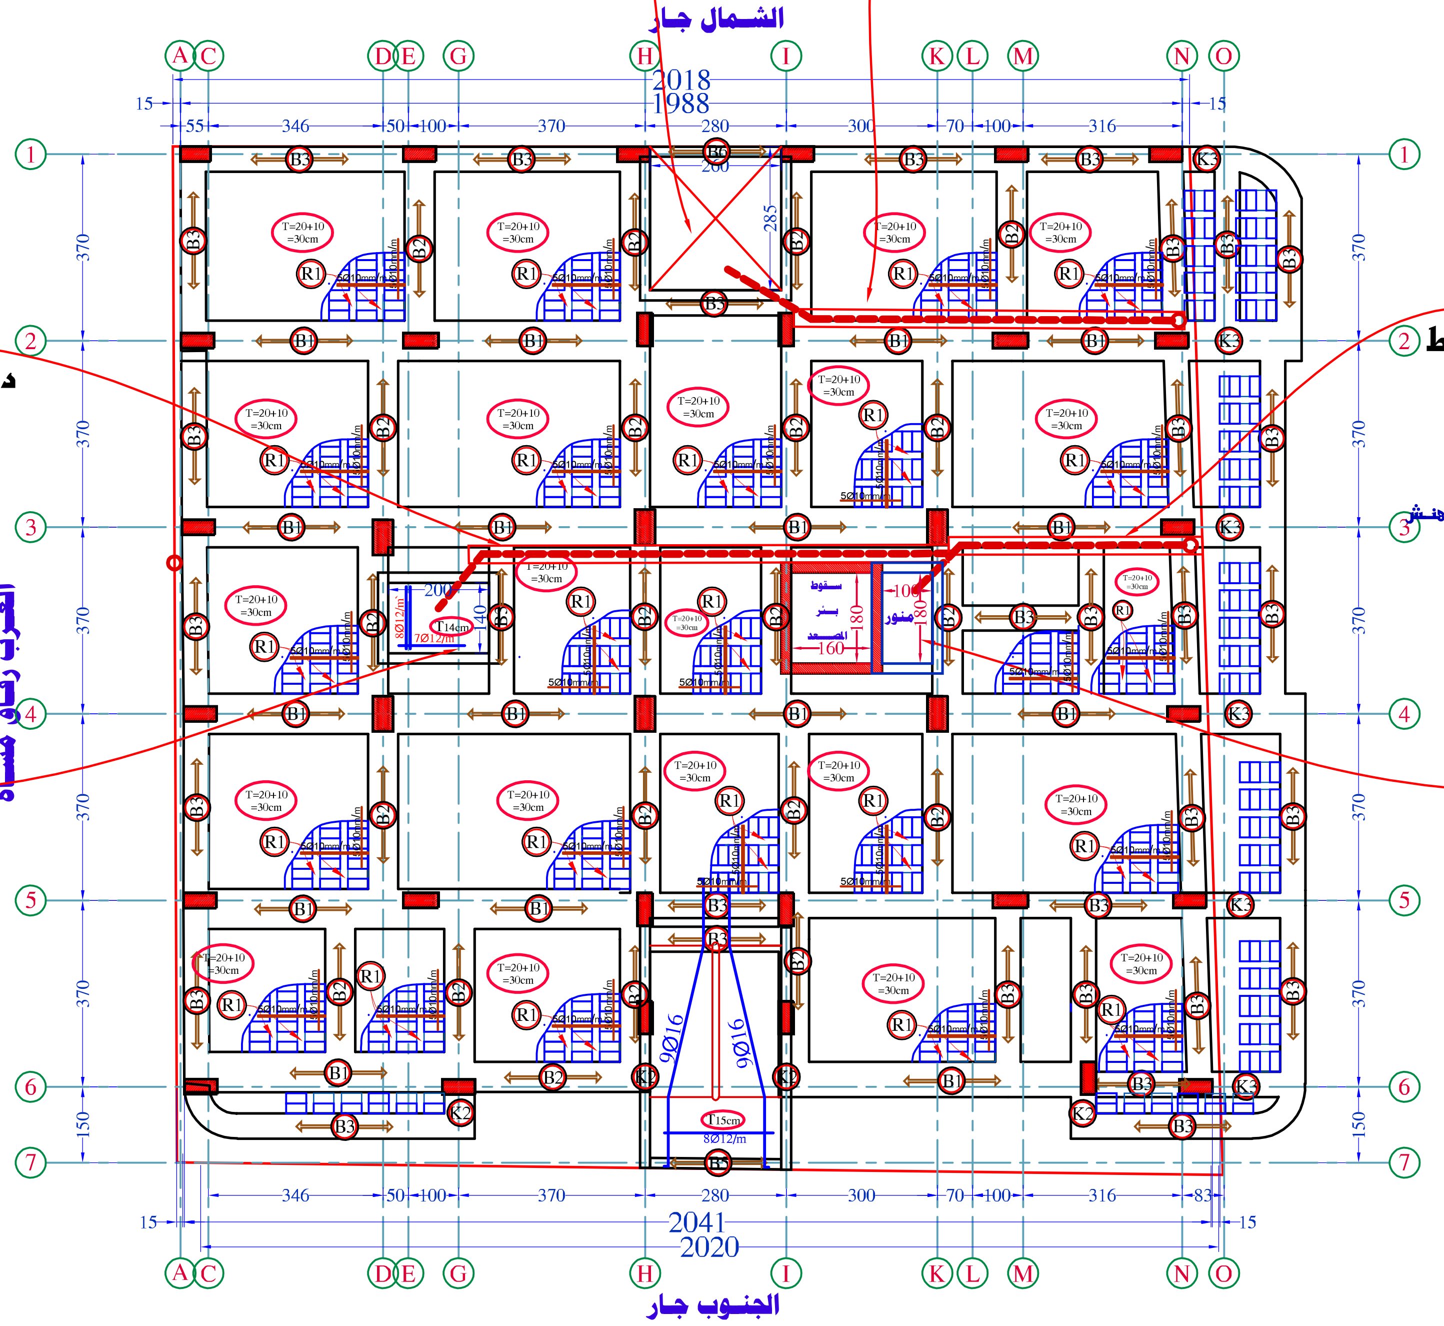

خط تصريف مجاري
معلق قطر 6هنش
داخل جسر خرسانة ساقط
مقاس 35 × 35سم

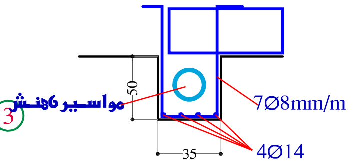

منور التصريف بمقاس
140×200سم بهبوط 50سم
عن مستوى سقف المسروق

منور التصريف بمقاس
100×180سم بهبوط 50سم
عن مستوى سقف المسروق
بجسر 20×80 سم

الأسقاط الأفقي لسقف الدور المسروق

جدول تسليح حديد السقف الهردي

الرمز	المقاسات		حديد التسليح			الكانات
	عرض (سم)	أرتفاع (سم)	سفلي مستقيم	سفلي مكسح	علوي مستقيم	
B1	80	30	6ø16	5ø16	5ø16	2*7Ø8 mm / m
B2	60	30	4ø16	3ø16	5ø14	7Ø8 mm / m
B3	50	30	4ø16	2ø16	4ø14	7Ø8 mm / m
B4	40	30	4ø16	---	3ø14	7Ø8 mm / m
B5	20	50	2ø16	2ø16	2ø14	7Ø8 mm / m
B6	25	30	3ø16	———	3ø14	7Ø8 mm / m
R1	15/18	30	2ø12	———	1ø12	7Ø8 mm / m
K1	عرض الجسر المقابل	30	4ø16	———	4ø16	7Ø8 mm / m
K2	25	80	5ø18	———	5ø18	7Ø8 mm / m
K3	عرض الجسر المقابل	30	4ø18	———	4ø18	7Ø8 mm / m

أشتراطات هامة في تنفيذ الأسقف

1. ارتفاع الجسور المحددة في الجدول يشمل البلك الهردي 20سم وبلاطة السقف .بسمك10سم
2. يتم تكسيح حديد الجسور بعد الأعمدة بمقدار ربع المسافة بين الأعمدة
3. يتم الخلط للخرسانة المسلحة بكمية 350 كجم أسمنت لكل متر مكعب
4. يتم الخلط للخرسانة من المواد النظيفة) الكري و النيس(والخالية من الأتربة والمواد العضوية
5. يتم التربيط لجميع تقاطعات الحديد سواء في الجسور أو الأعصاب أو البلاطات
6. يتم رفع حديد الجسور من فوق سطح الشدات الخشبية بمقدار (2.5 .)سم
7. يتم الرش بالمياه للخرسانة لفترة لاتقل عن 21يوماً من تاريخ الصب
8. يتم عمل التمديدات اللأزمة لنقاط الكهرباء والتمديدات الصحية قبل موعد الصب
9. يجب أن لاتزيد المسافة بين قوائم الدعم عن 70 سم ولايتم فك الخشب قبل مرور 21يوماً
10. حديد الكوابيل هوحديد اضافي الى الحديد الممتد من الجسور المقابلة لهذه الكوابيل
11. الجسور رقم5. هي جسور ساقطة مع منسوب بسطة الدرج

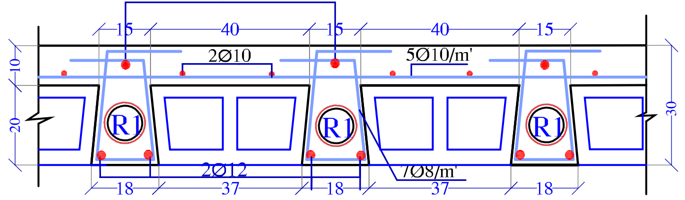

تفصيلة السقف الهوردي

الجمهورية اليمنية صنعاء
Sana'a R.of YEMEN
P.O.Box / 8425
Tele / 00967-01-226583
fax / 00967-01-239170

مكتب الحكمة للهندسة
AL-Hikmah Office. For Eng.

أسم المشروع	عمارة تجارية سكنية
أسم المالك	الأخ / محمد فرحان أحمد الجثام
نوع المخطط	إنشائي
أسم المخطط	الأسقاط الأفقي لسقف الدور المسروق
مقياس الرسم	1 :150
رقم المخطط	7