

 
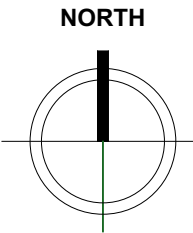
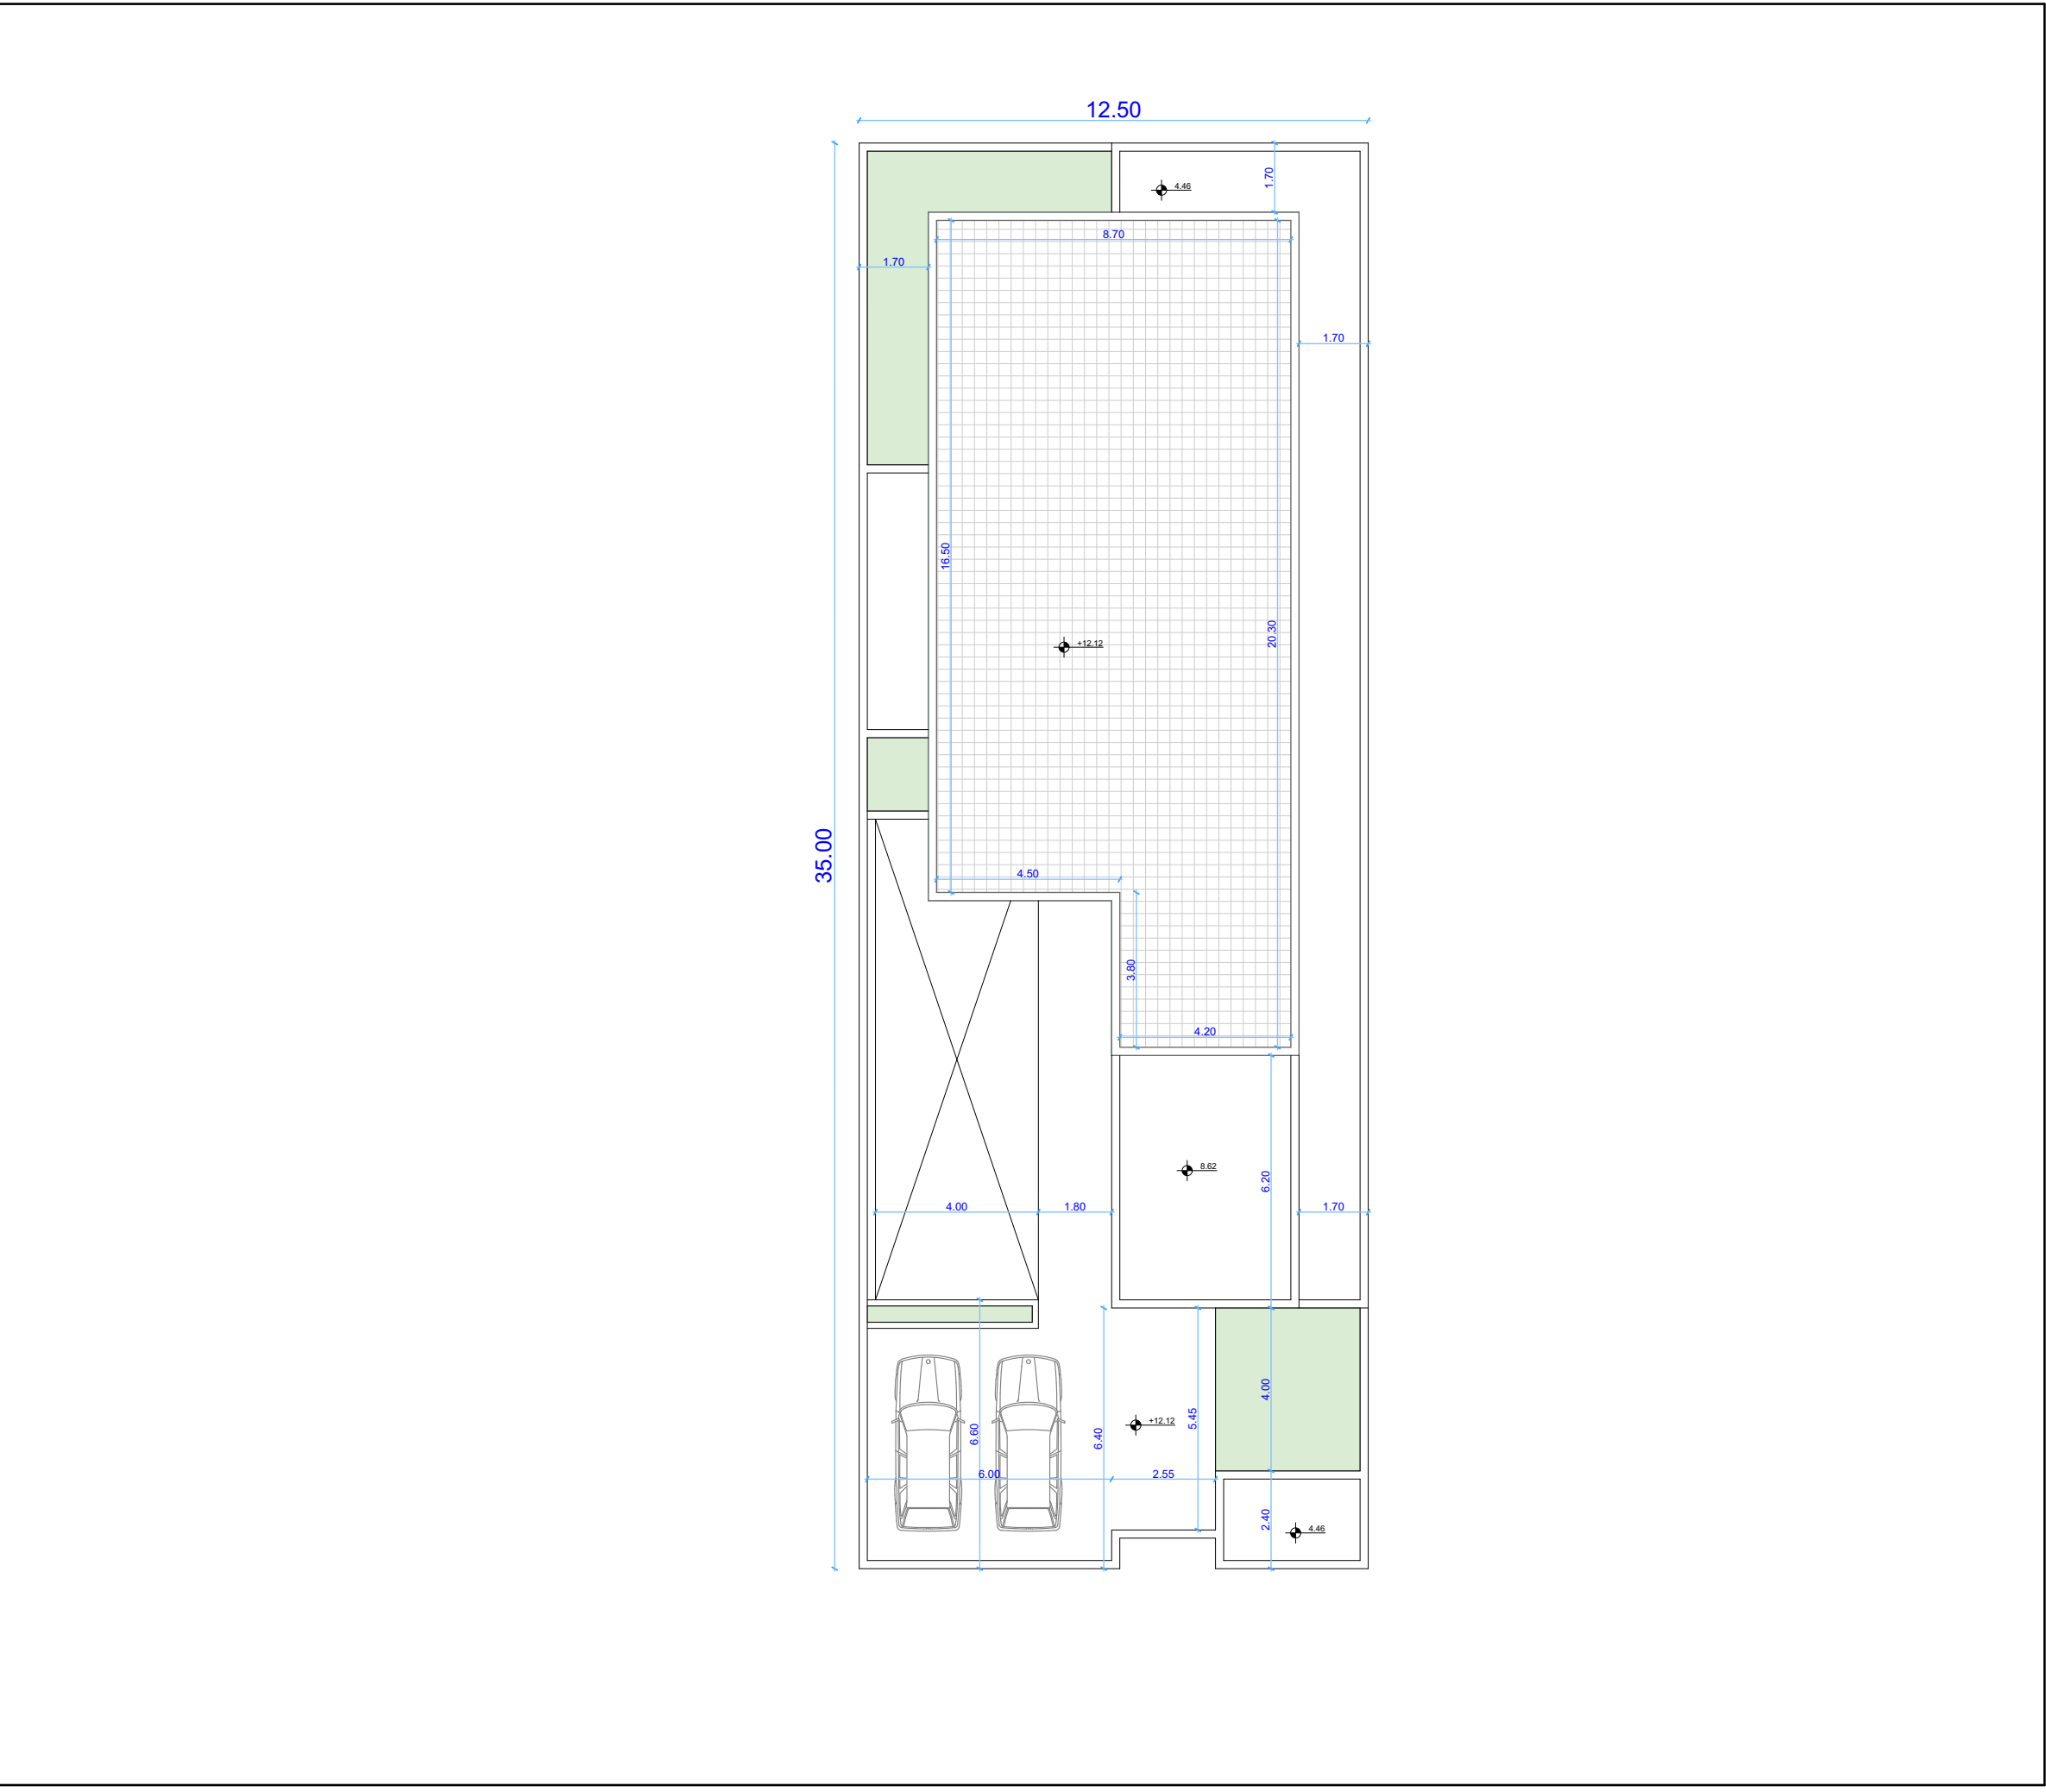


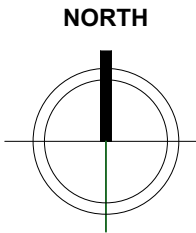

PROJECT : VILLA	
MR. ABDLALLAH BIN RASHEED	
NEIGHBOURHOOD	LOCATION
ALAHIQ	RIYADH
SHEET :	

SITE PLAN

Designed	Drawn	Checked	Approved	Date
Project No.			Drawing No.	
-	D	0	0	1
REVISION NO.				

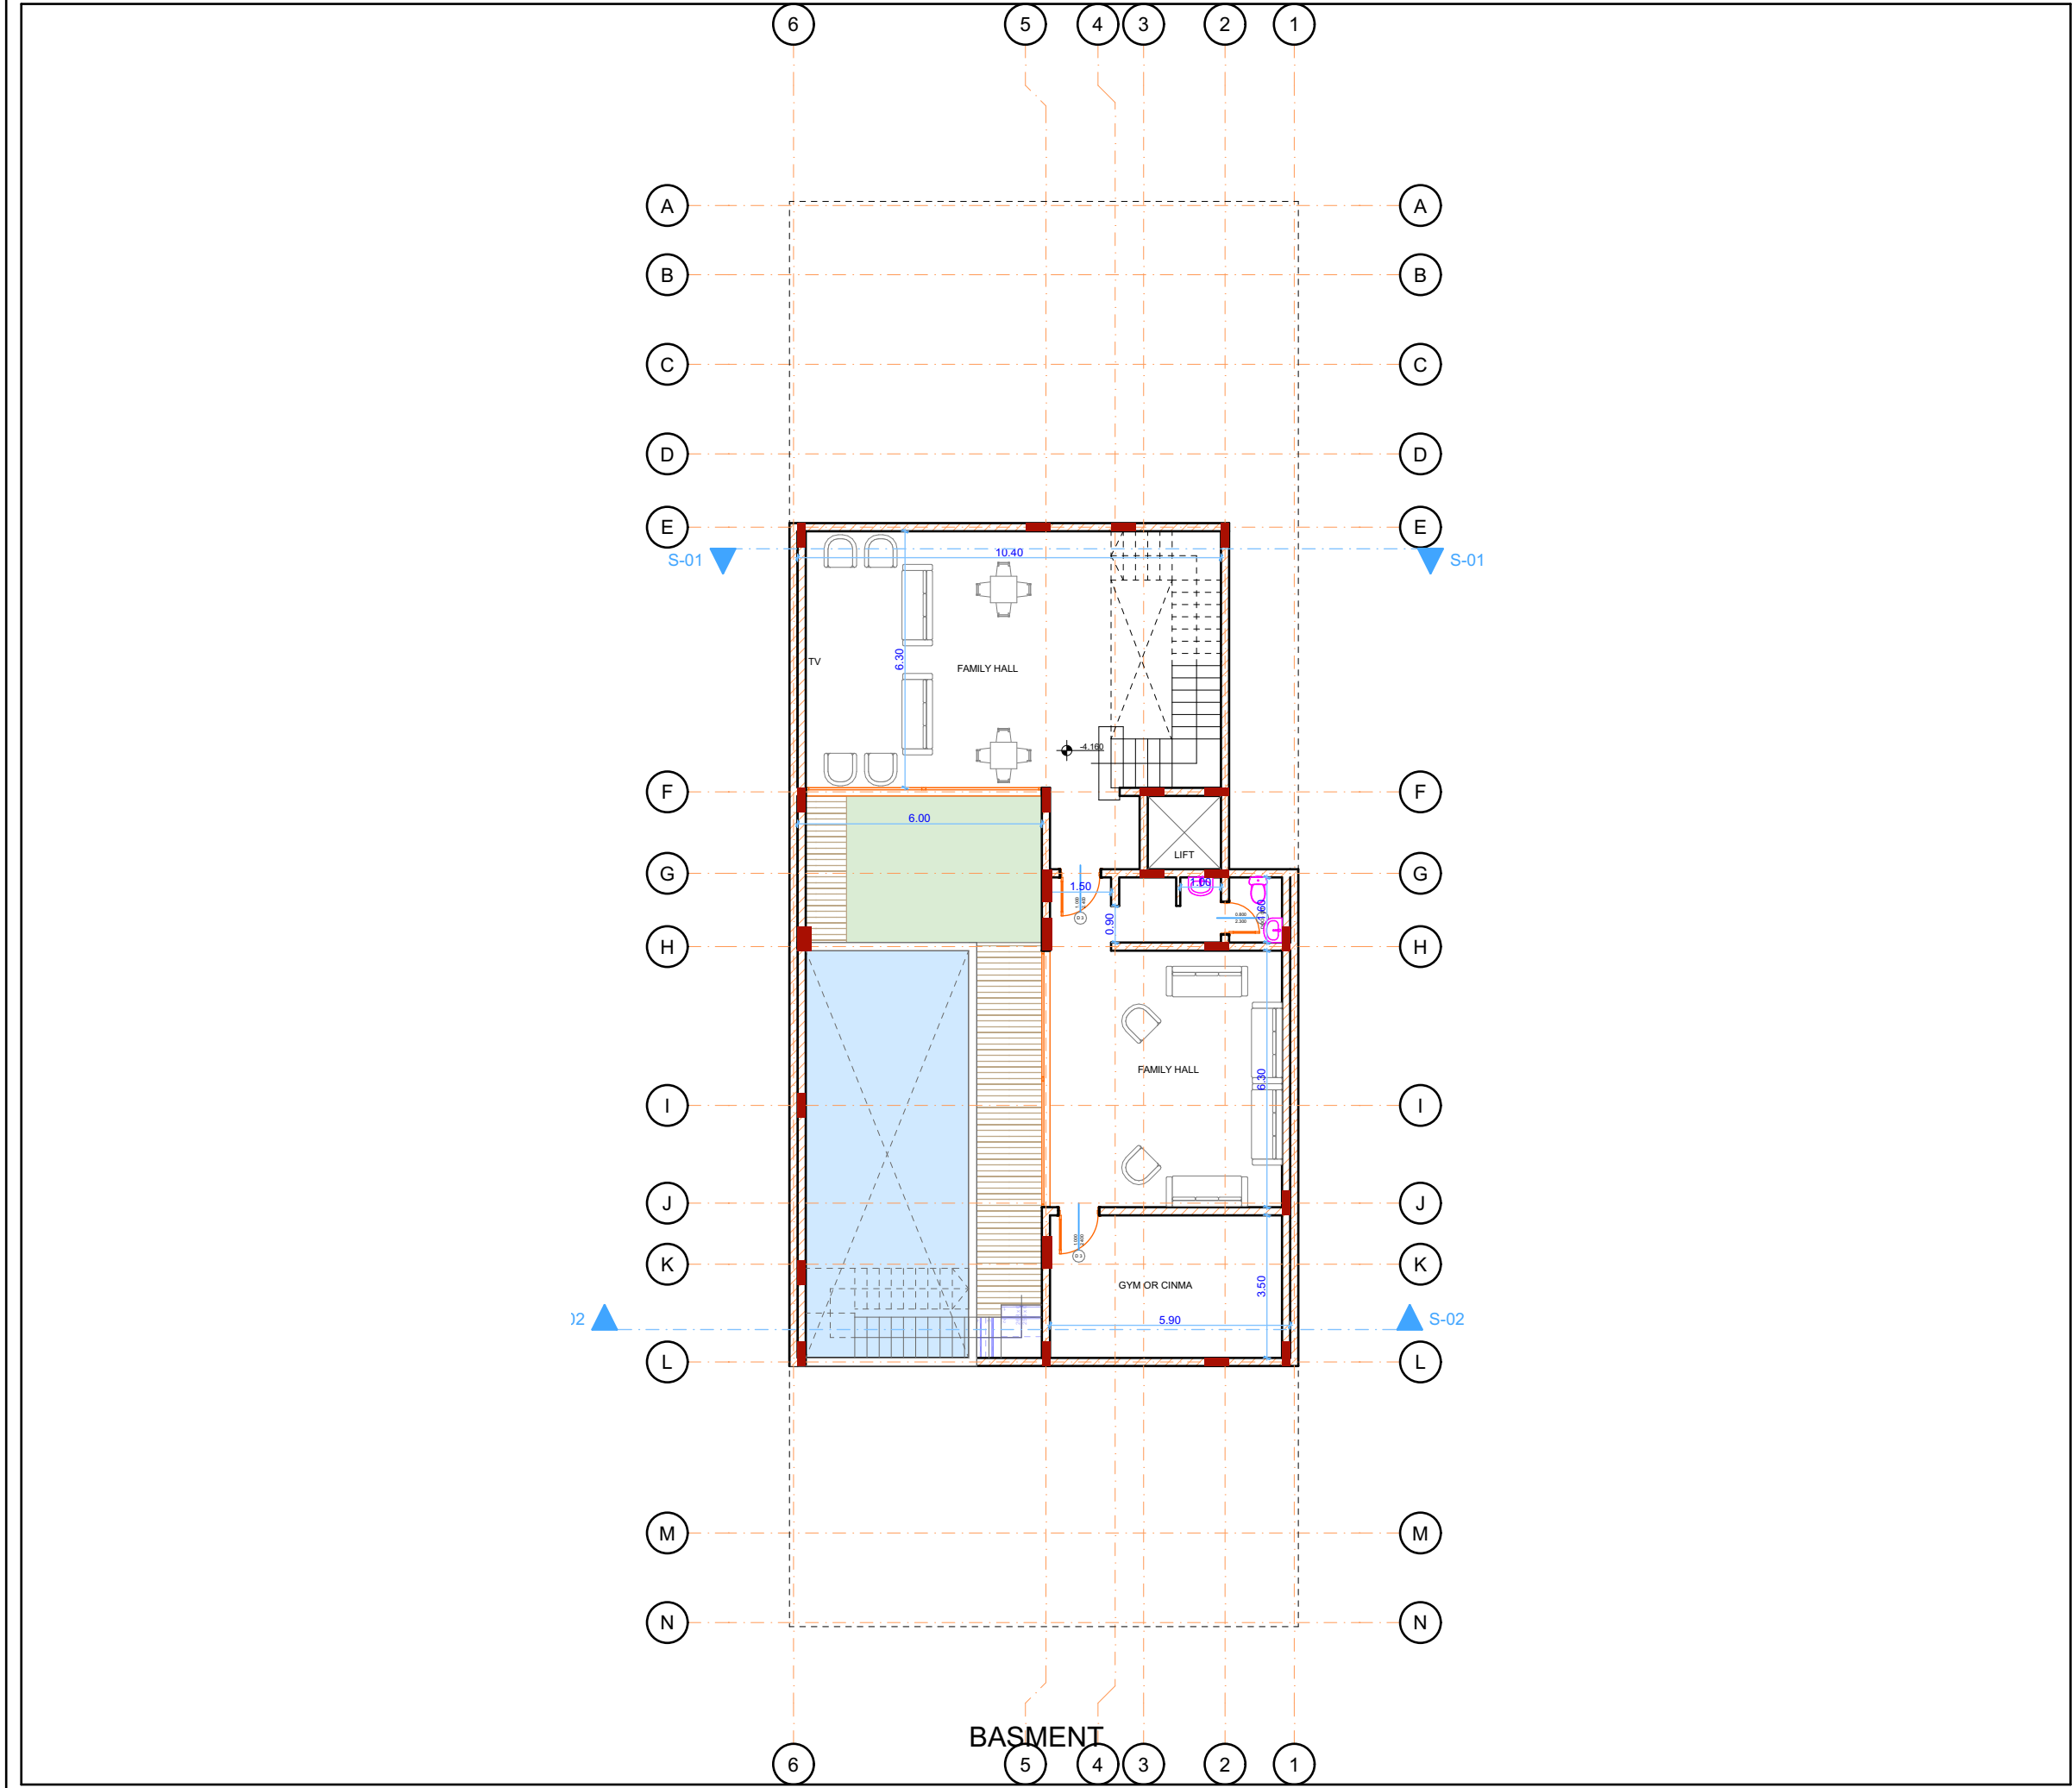

PROJECT : VILLA

MR. ABDLALLAH BIN RASHEED

NEIGHBOURHOOD

LOCATION




ALAQIQ

RIYADH

SHEET :

BASEMENT PLAN

Designed		Drawn		Checked		Approved		Date		
Project No.						Drawing No.				
-	D	0	0	0	1					-
REVISION NO.										

 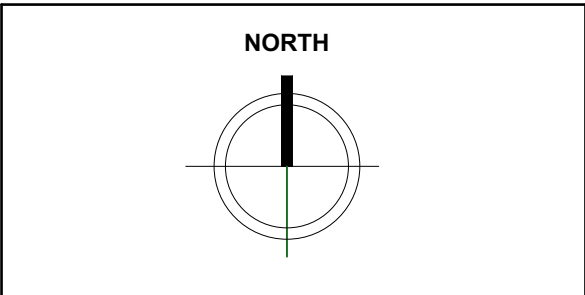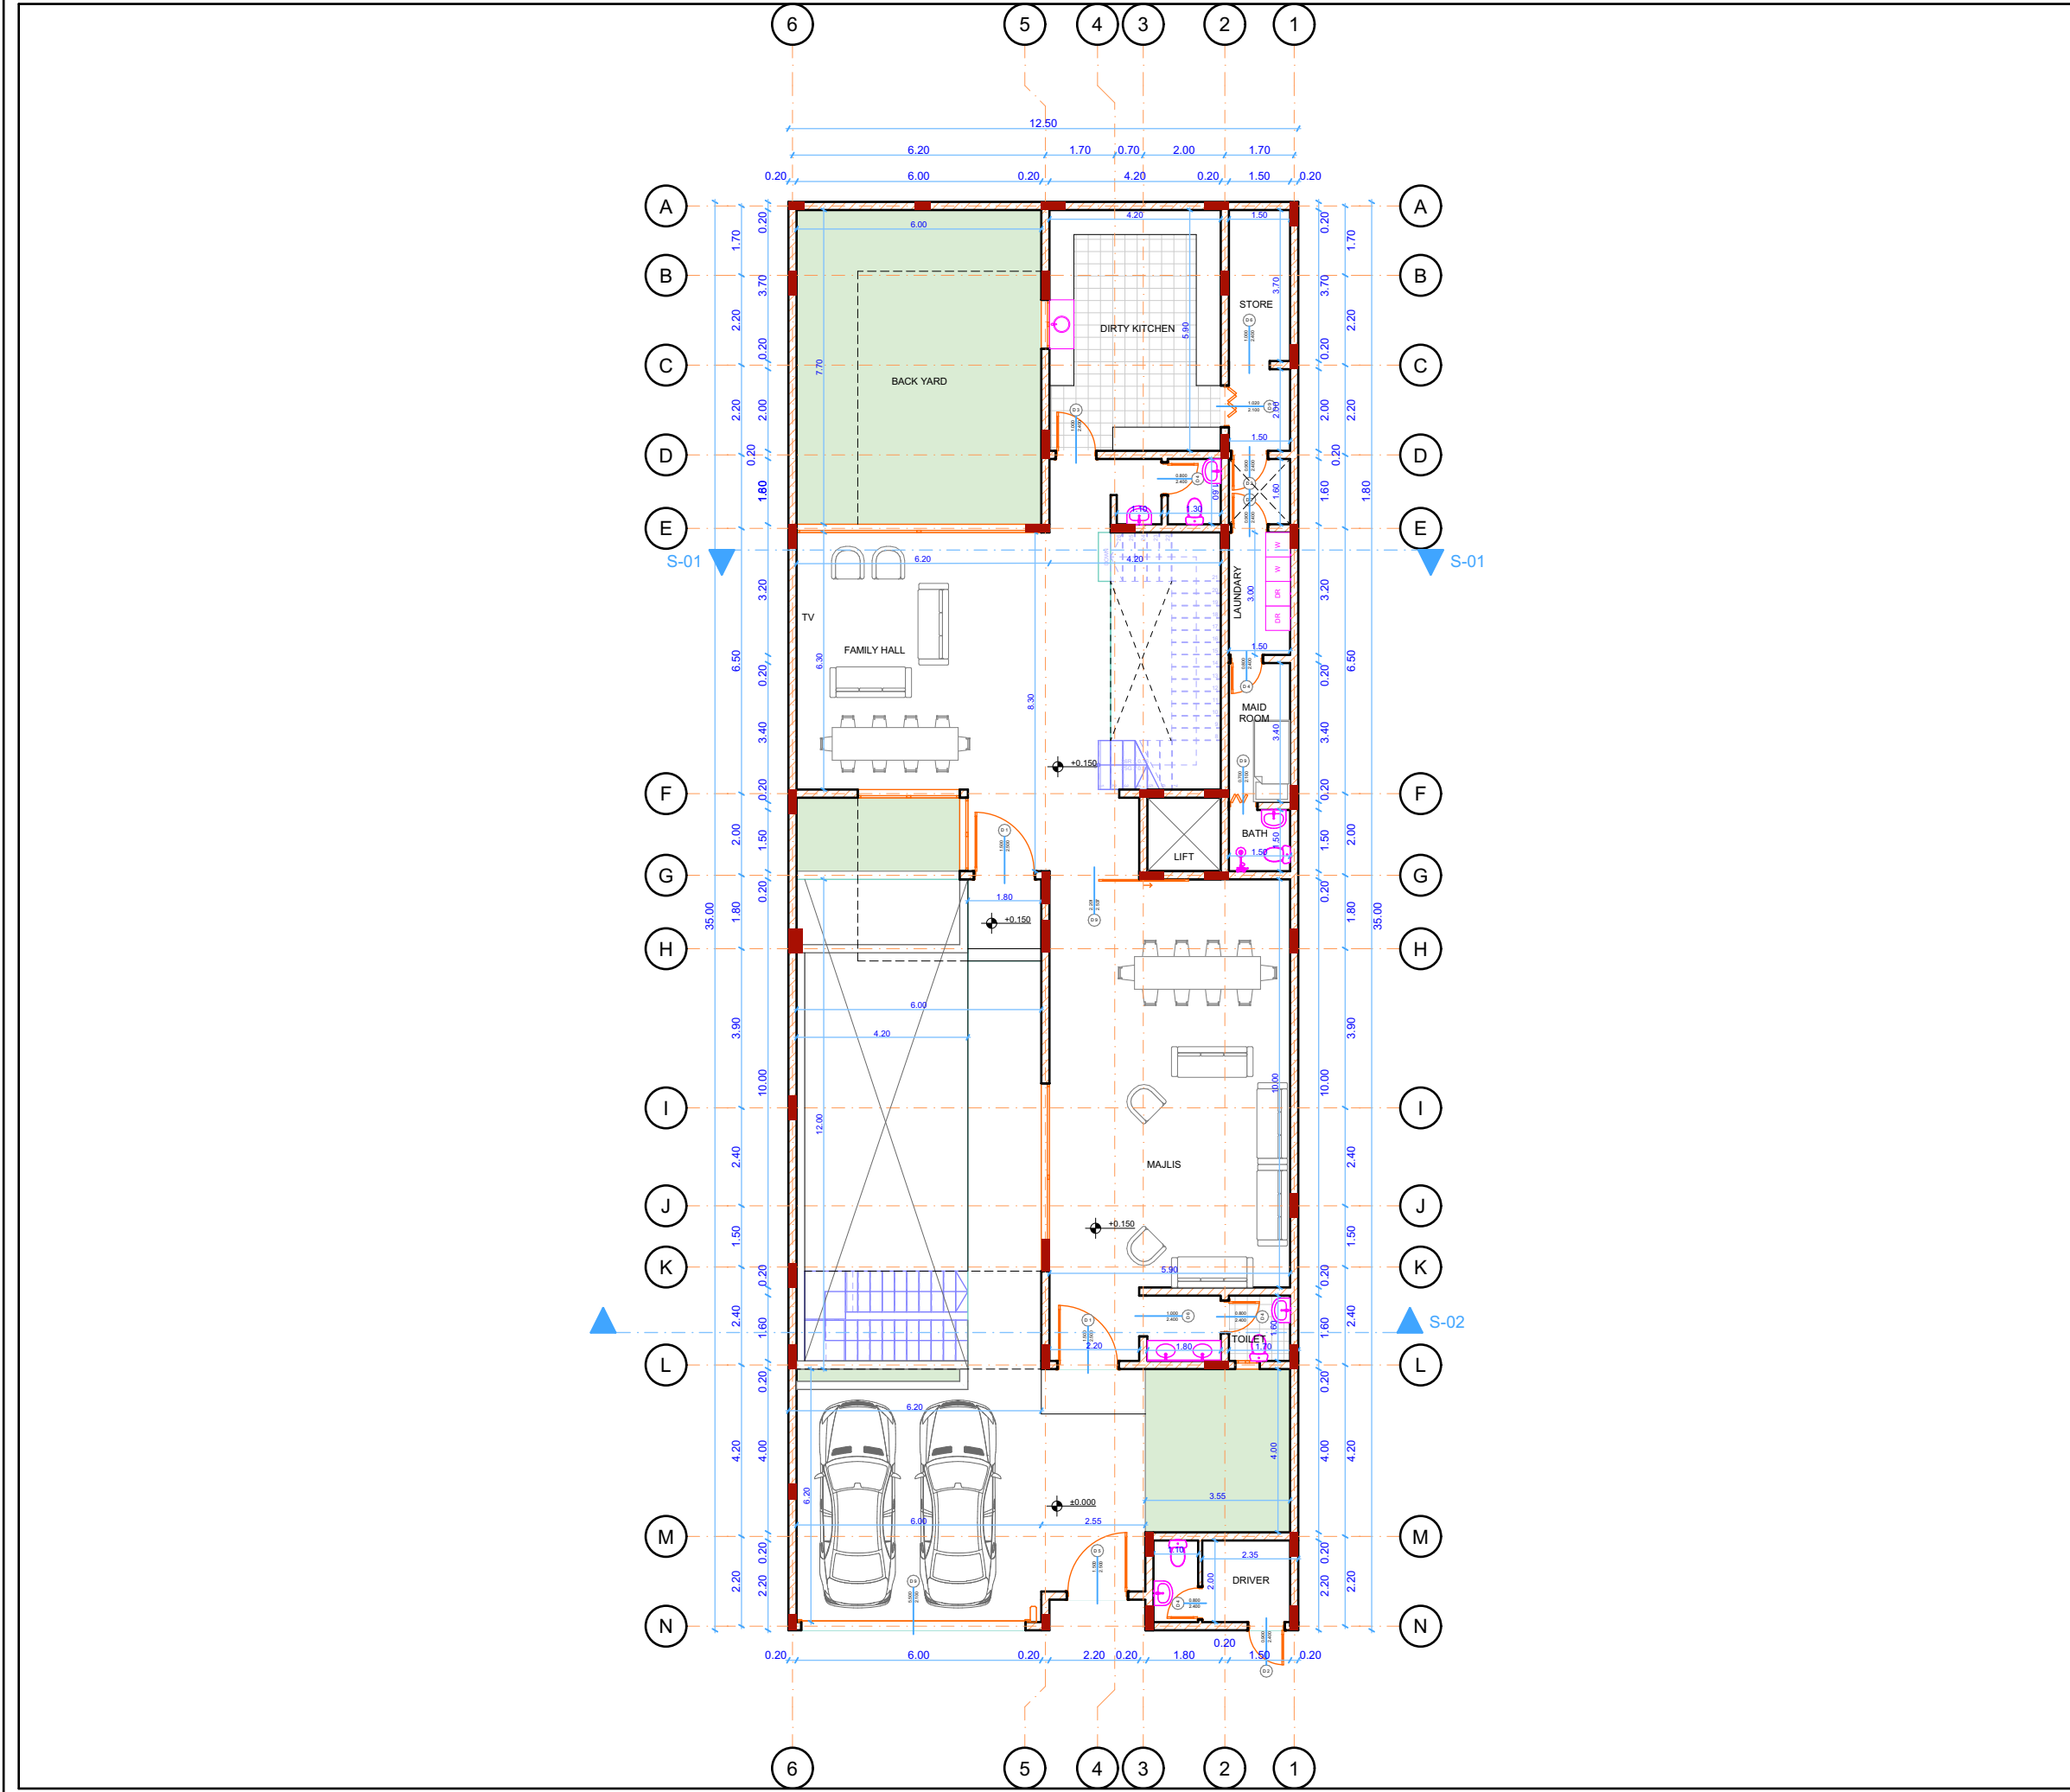



PROJECT : VILLA	
MR. ABDLALLAH BIN RASHEED	
NEIGHBOURHOOD	LOCATION
ALAHIQ	RIYADH

SHEET :

GROUND FLOOR PLAN



Designed	Drawn	Checked	Approved	Date
Project No.			Drawing No.	
-	D	0	0	0
REVISION NO.				

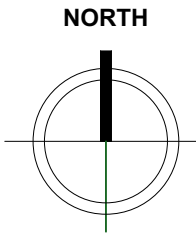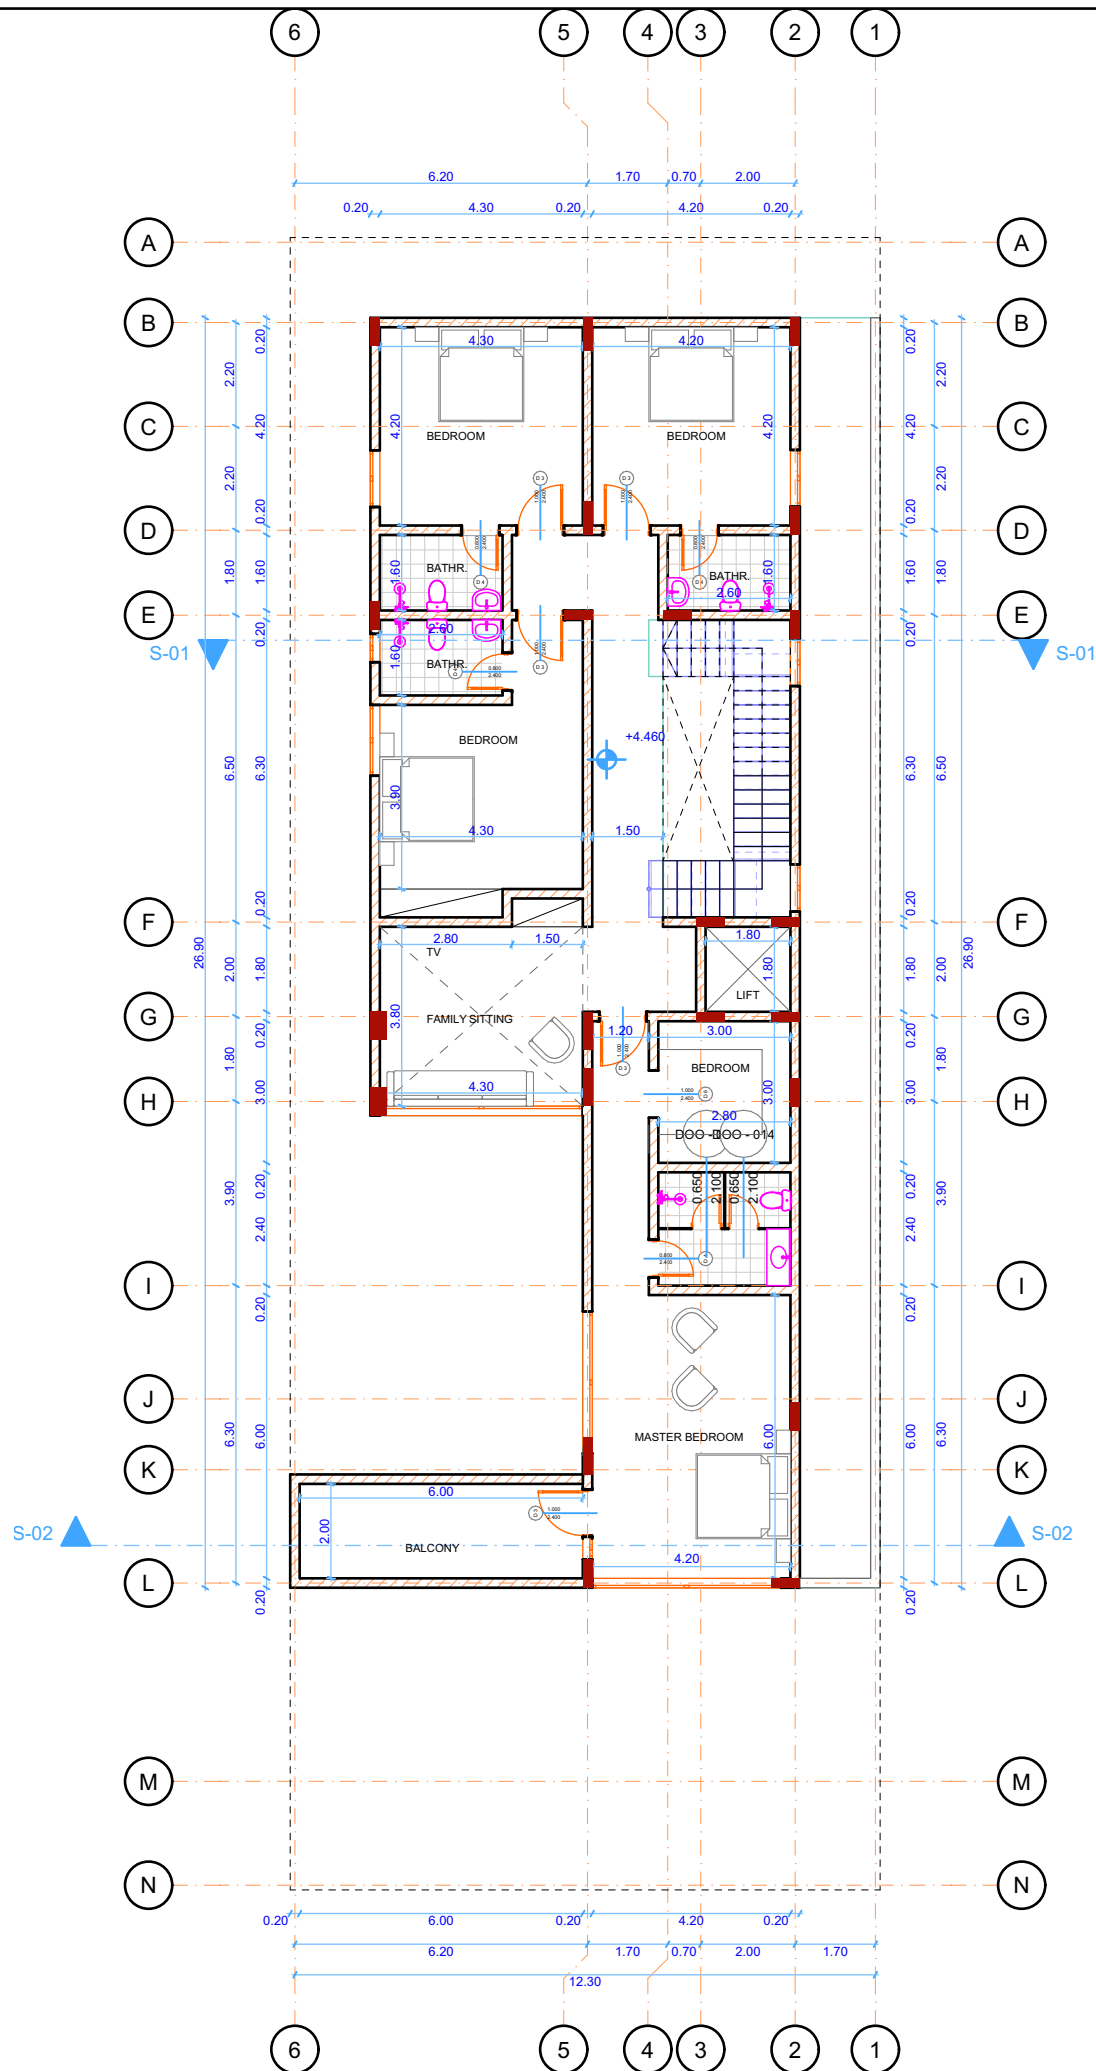

PROJECT : VILLA



MR. ABDLALLAH BIN RASHEED

NEIGHBOURHOOD	LOCATION
ALAQIQ	RIYADH

SHEET :

FIRST FLOOR PLAN

Designed	Drawn	Checked	Approved	Date
Project No.				Drawing No.
-	D	0	0	
REVISION NO.				

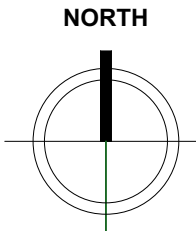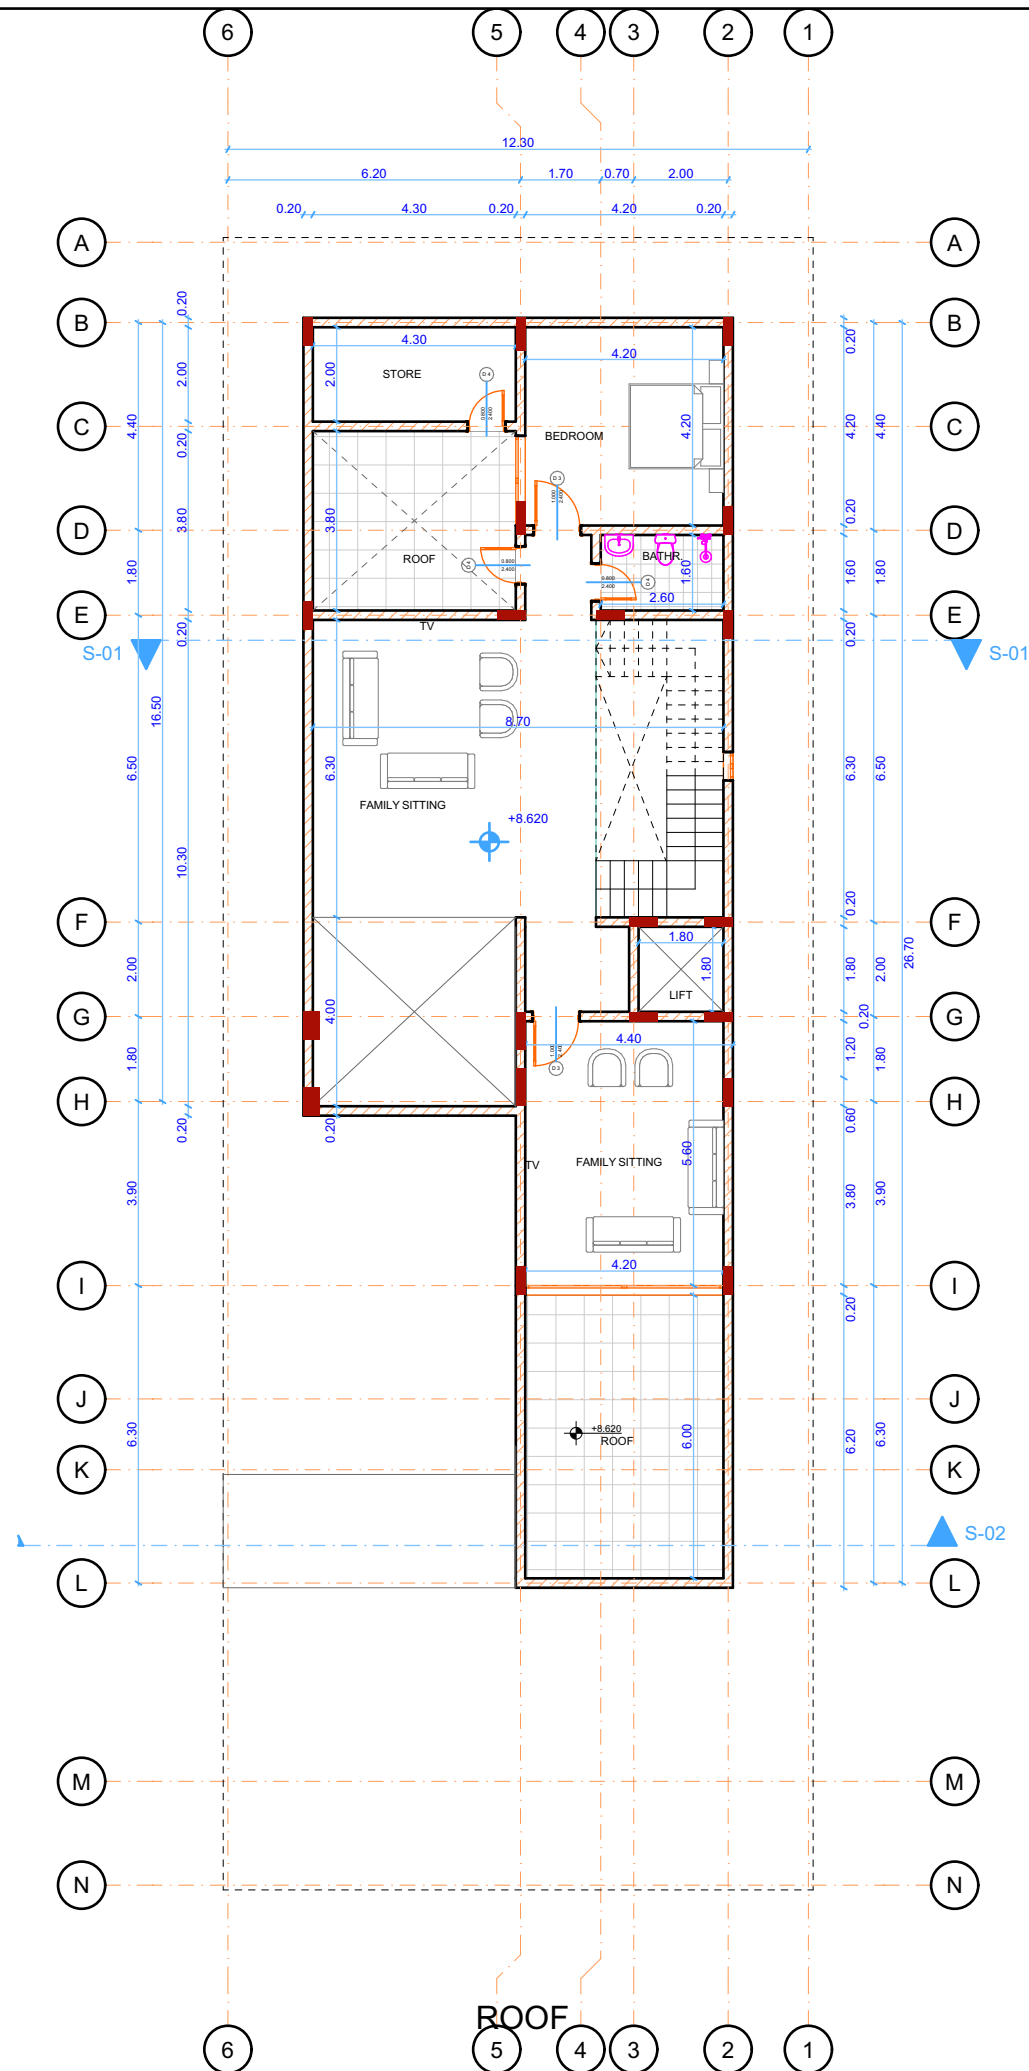

PROJECT : VILLA

MR. ABDLALLAH BIN RASHEED

NEIGHBOURHOOD

LOCATION



ALAIQ

RIYADH

SHEET :

ROOF ANNEX PLAN

Designed	Drawn	Checked	Approved	Date
Project No.			Drawing No.	
-	D	0	0	0
REVISION NO.				

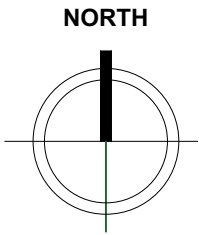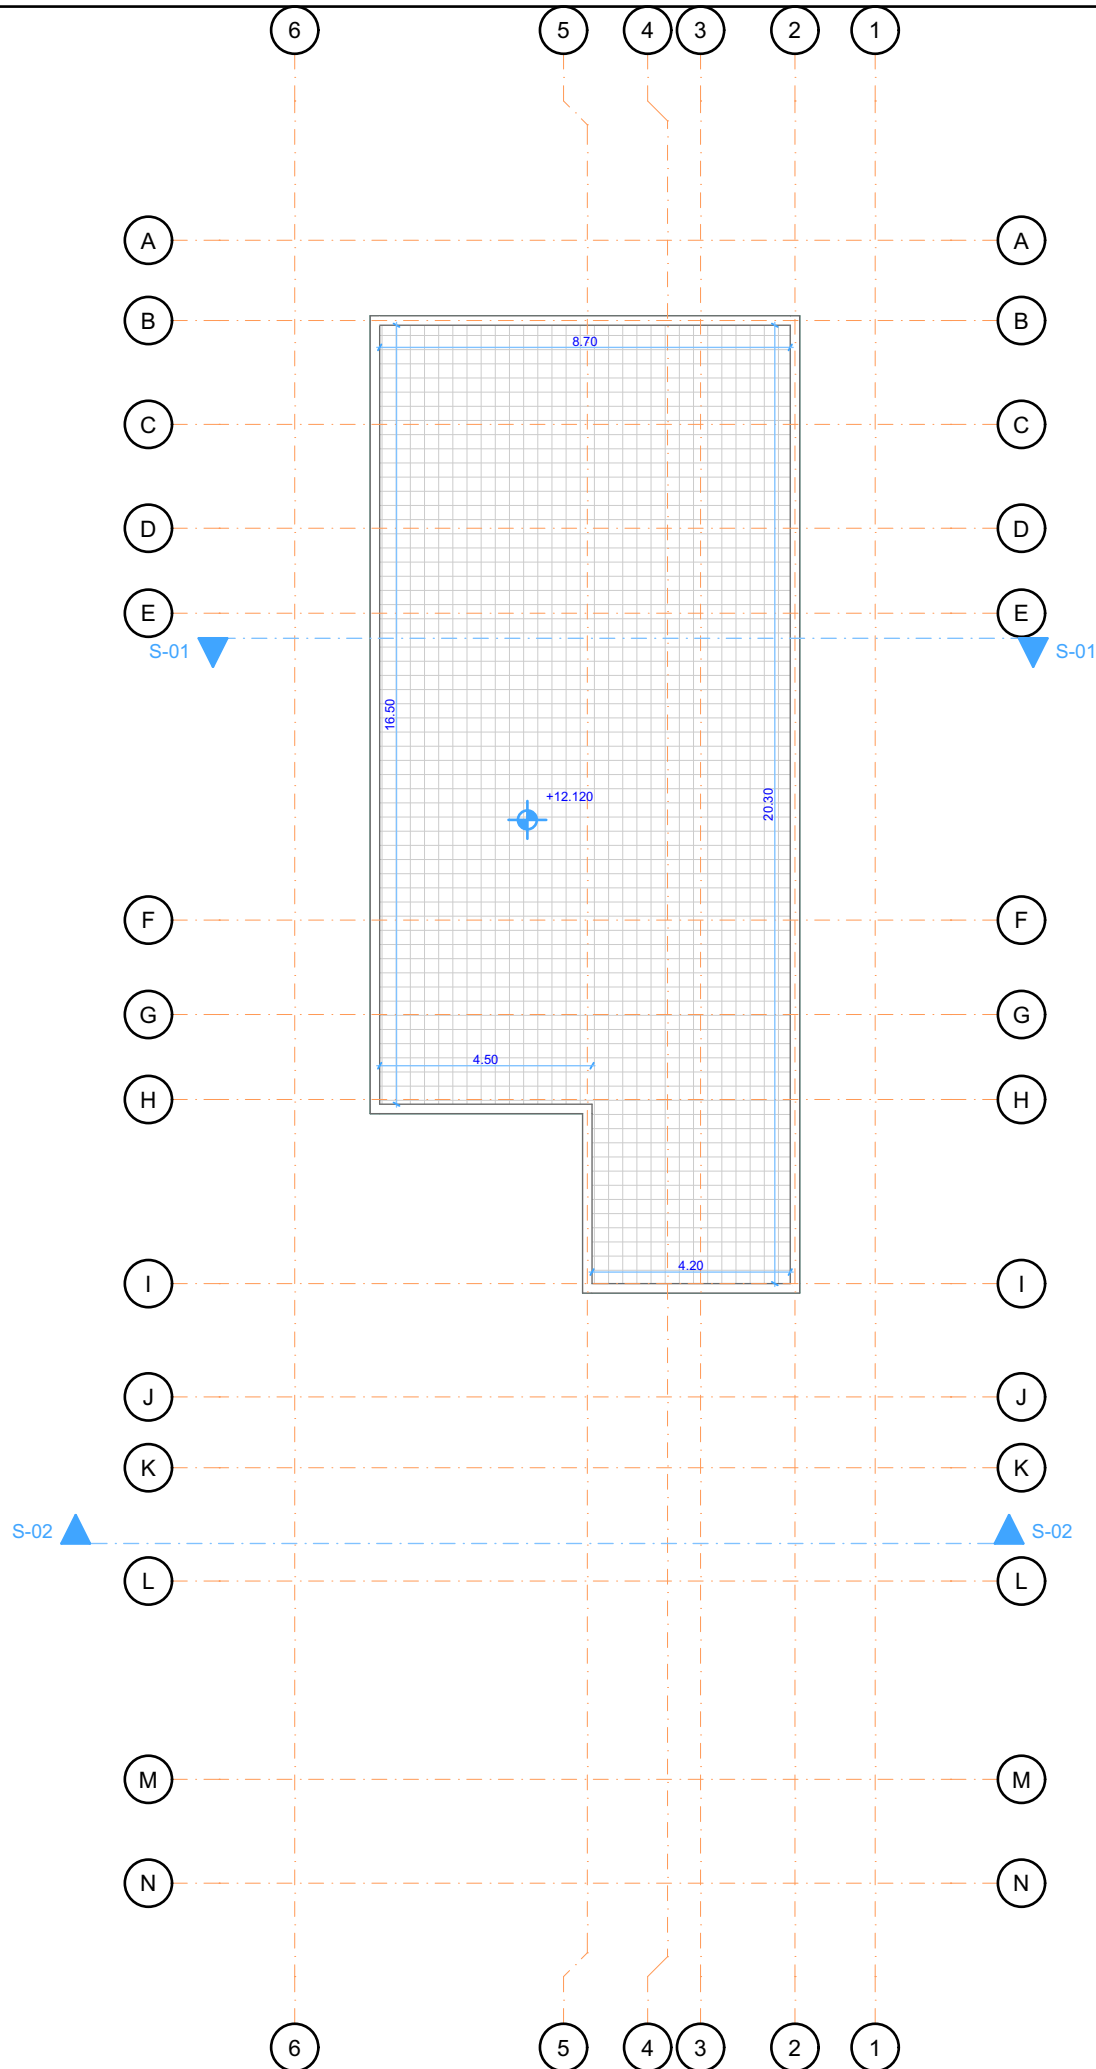

PROJECT : VILLA

MR. ABDLALLAH BIN RASHEED

NEIGHBOURHOOD

LOCATION



ALAQIQ

RIYADH

SHEET :

UPPER ROOF PLAN

Designed	Drawn	Checked	Approved	Date				
Project No.			Drawing No.					
-	D	0			0	0	1	-
REVISION NO.								

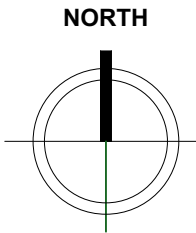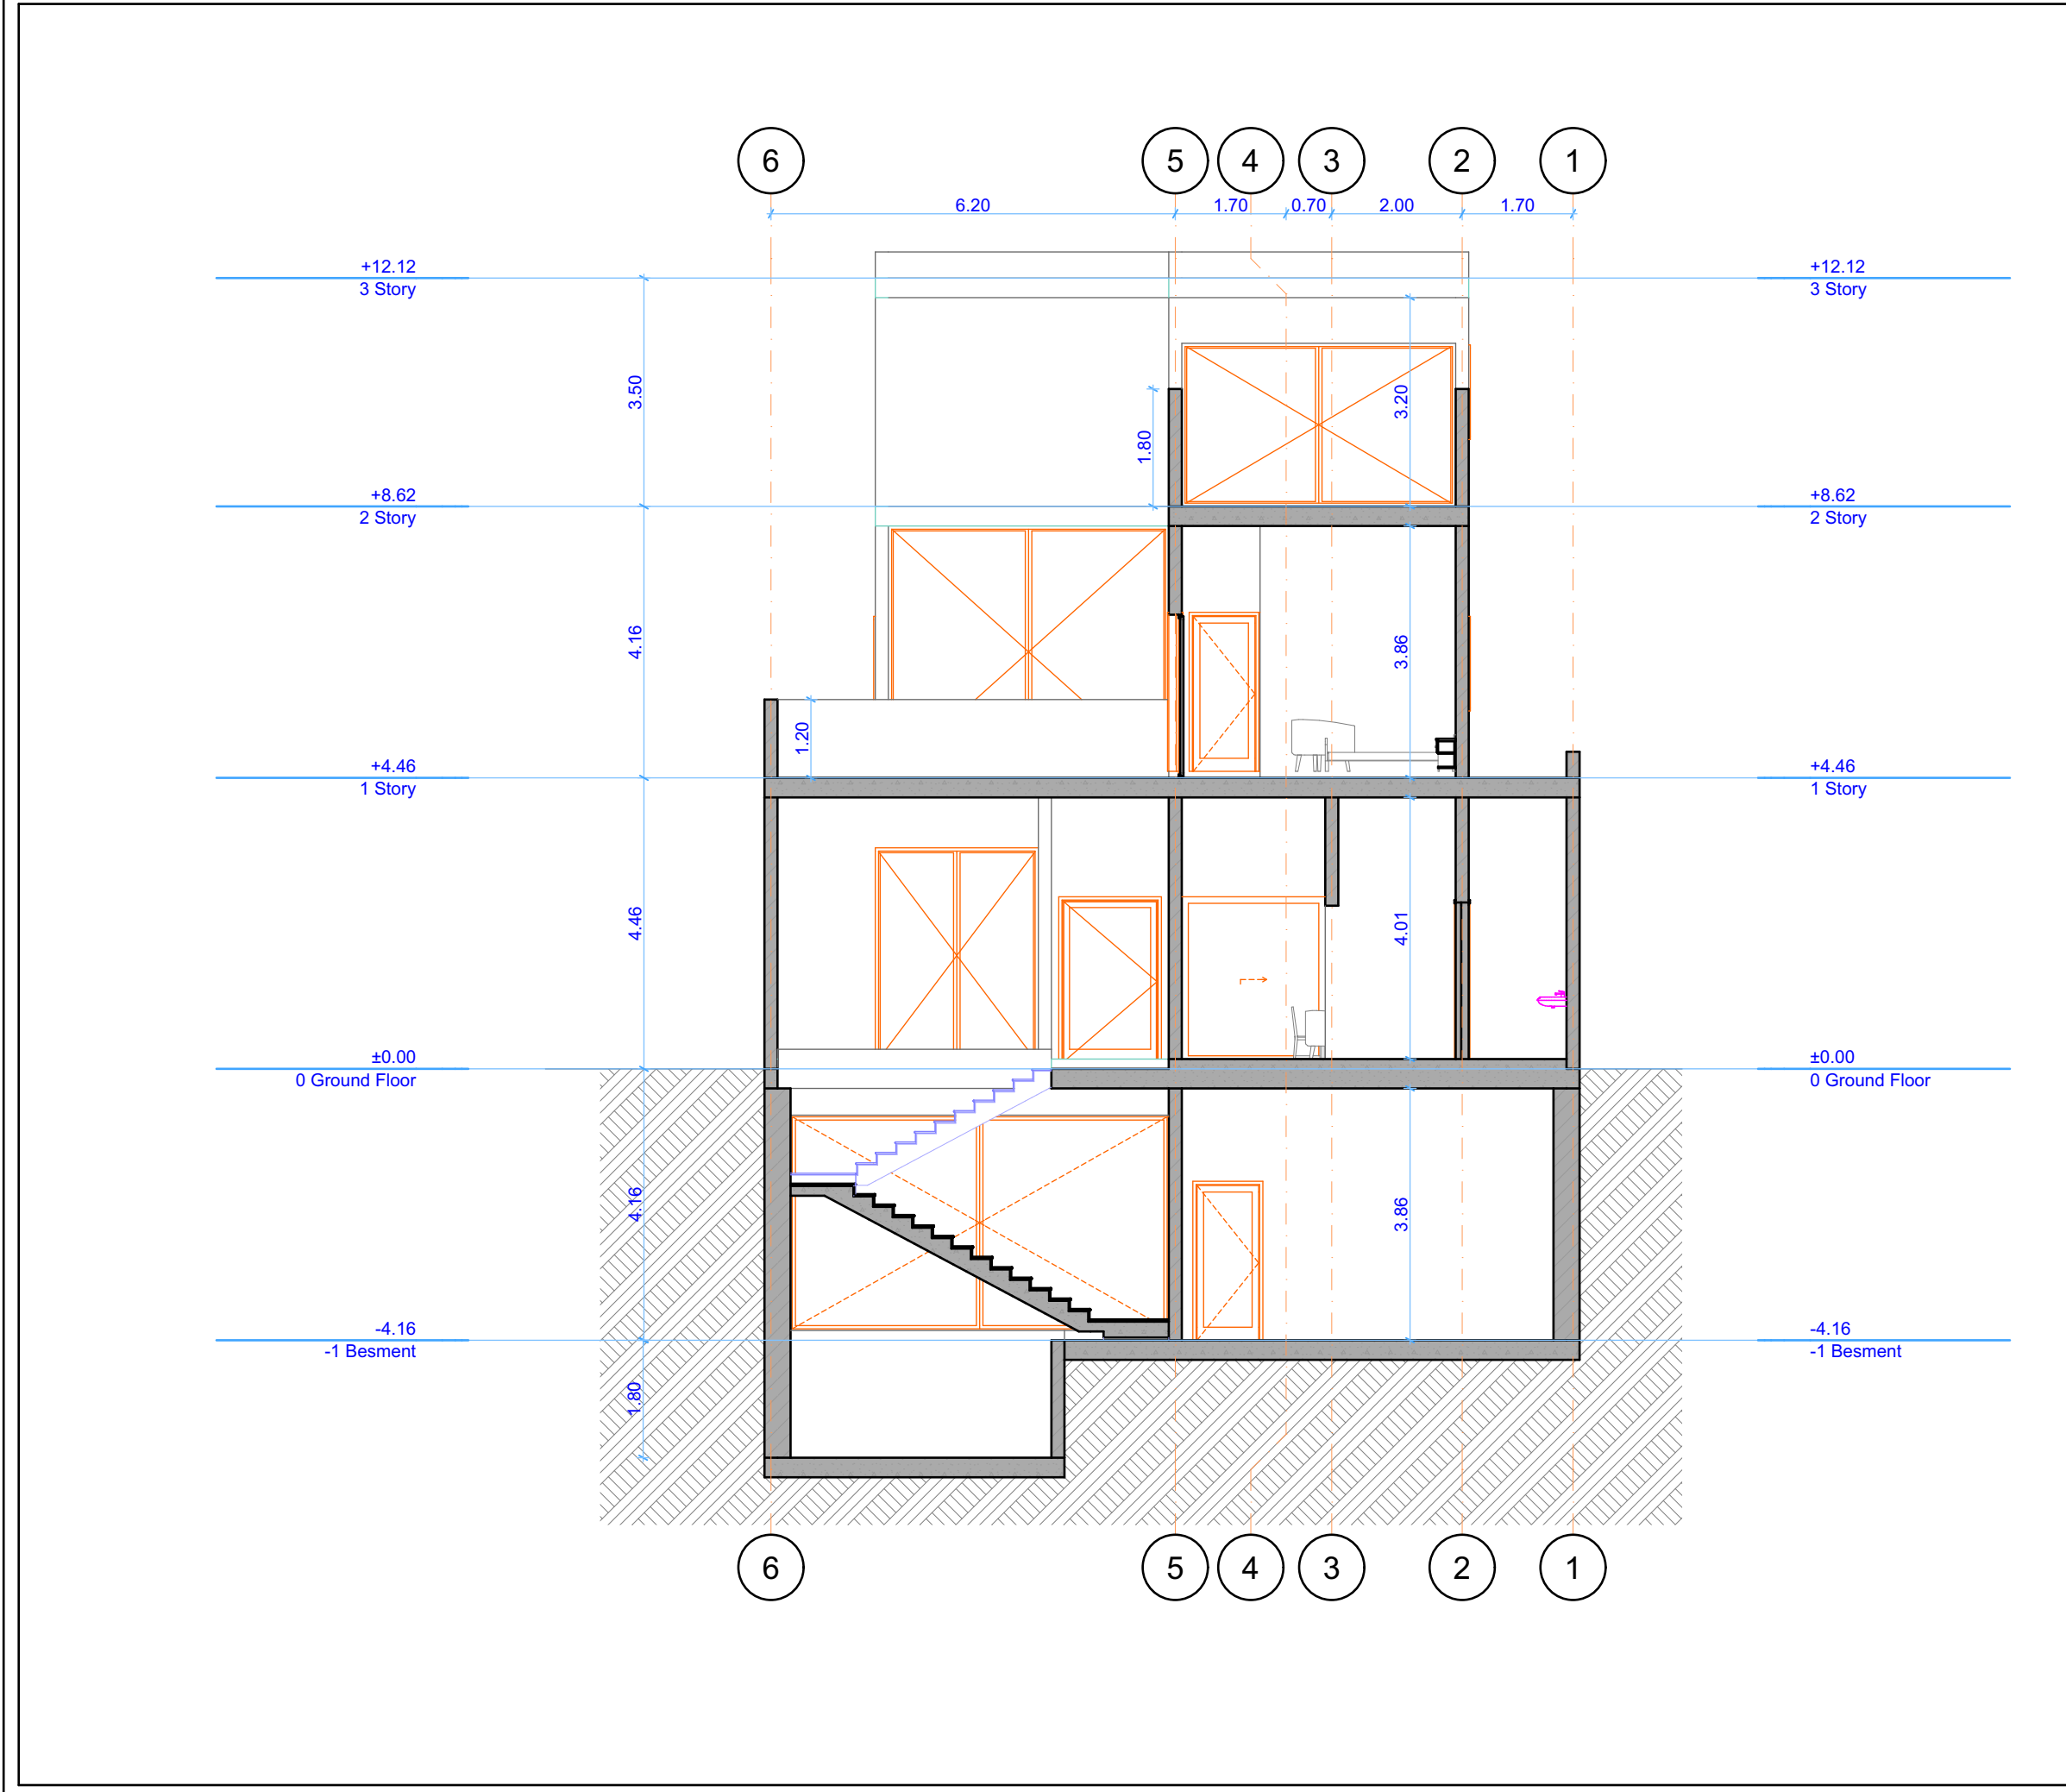

PROJECT : VILLA

MR. ABDLALLAH BIN RASHEED

NEIGHBOURHOOD

LOCATION

ALAIQ

RIYADH

SHEET :

SECTION 2

Designed	Drawn	Checked	Approved	Date
Project No.			Drawing No.	
-	D	0	0	0
REVISION NO.				