



جامعة صنعاء  
كلية الهندسة  
قسم العمارة  
سنة رابعة  
نقطة خاصة

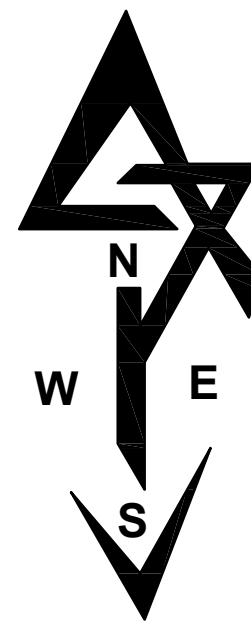


- خرسانه مسلحة
- حجر
- بلوك
- رمل
- خرسانه عادية
- تسريع
- تربة مدكونة


|            |                                                      |             |         |
|------------|------------------------------------------------------|-------------|---------|
| تقديم      | احمد عبدالاله دهمش                                   |             |         |
| اسم اللوحة | تفاصيل<br>الطائرات                                   | نوع اللوحة  | تنفيذية |
| رقم اللوحة | A-8                                                  | مقياس الرسم | 1: 10   |
| اشرافه     | د. محمد الوهاب الخريفي<br>م. اروي جباري م. حسام امين |             |         |

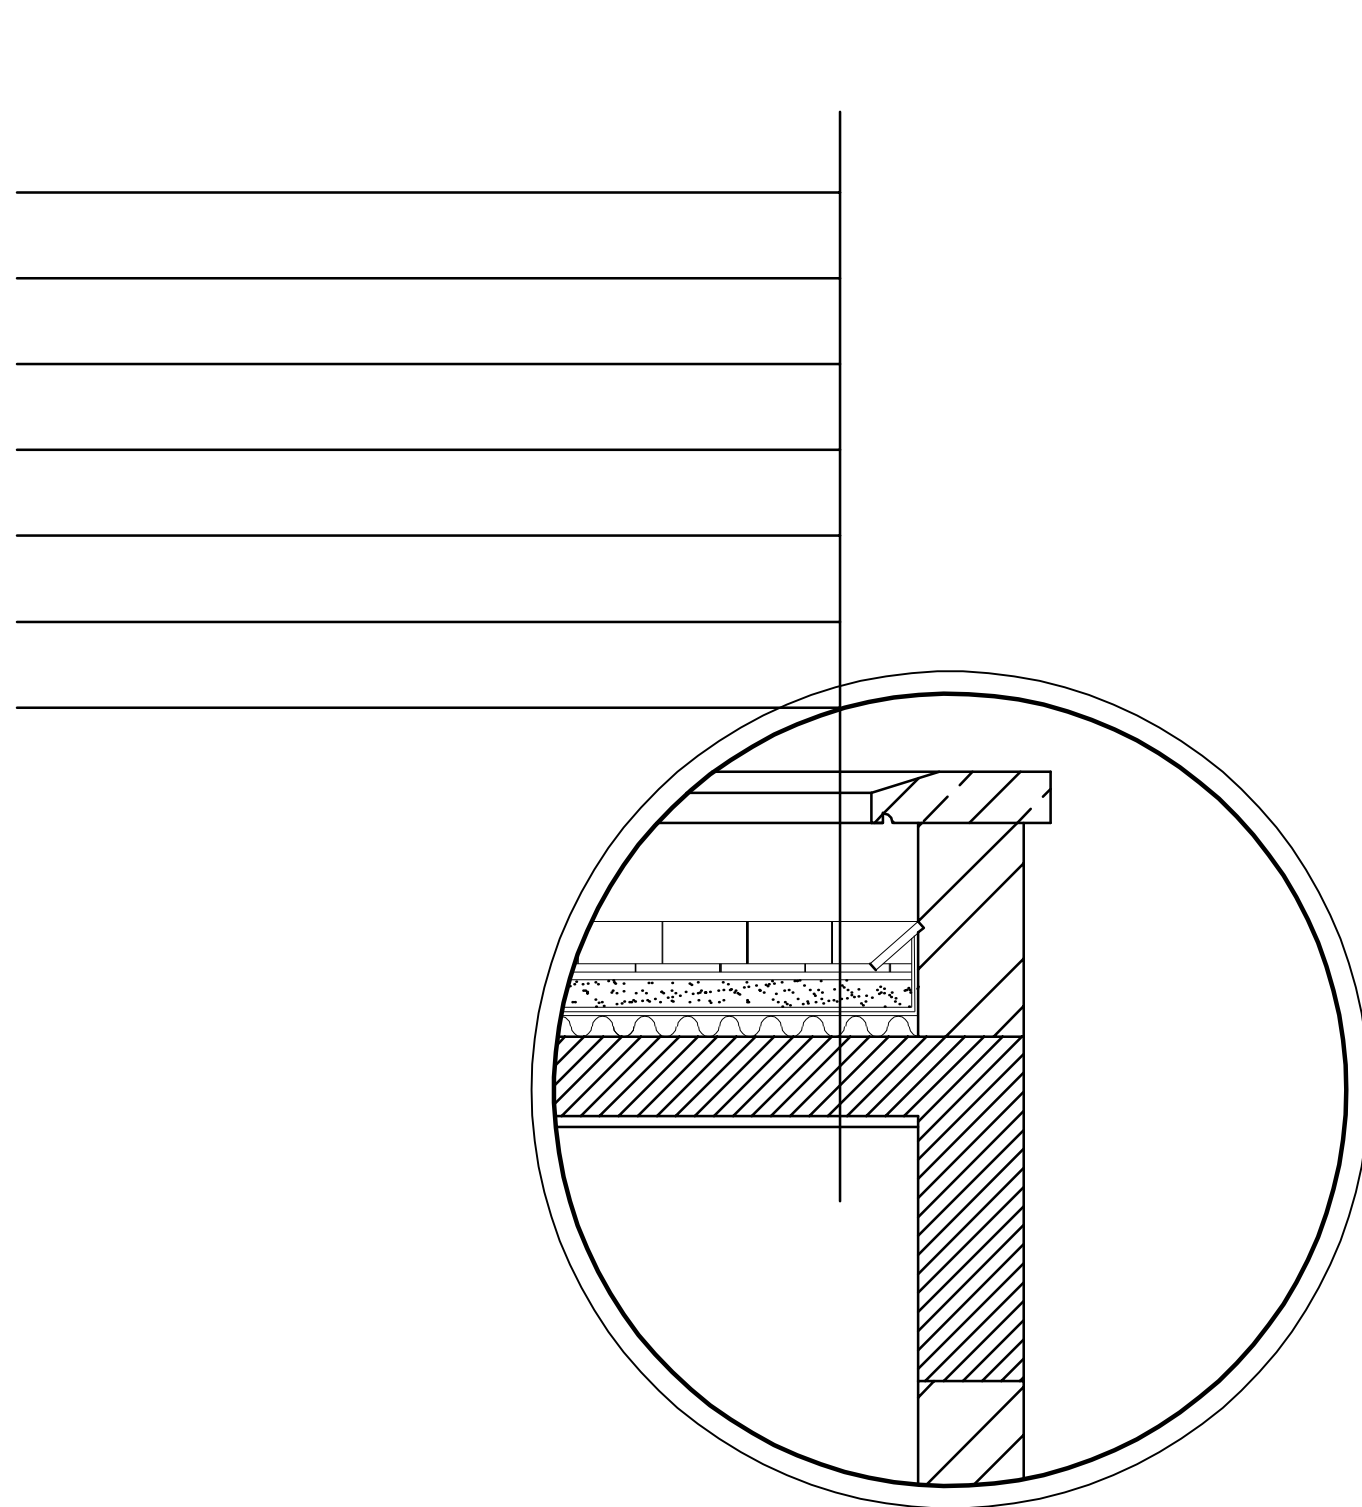


D9  
A-8

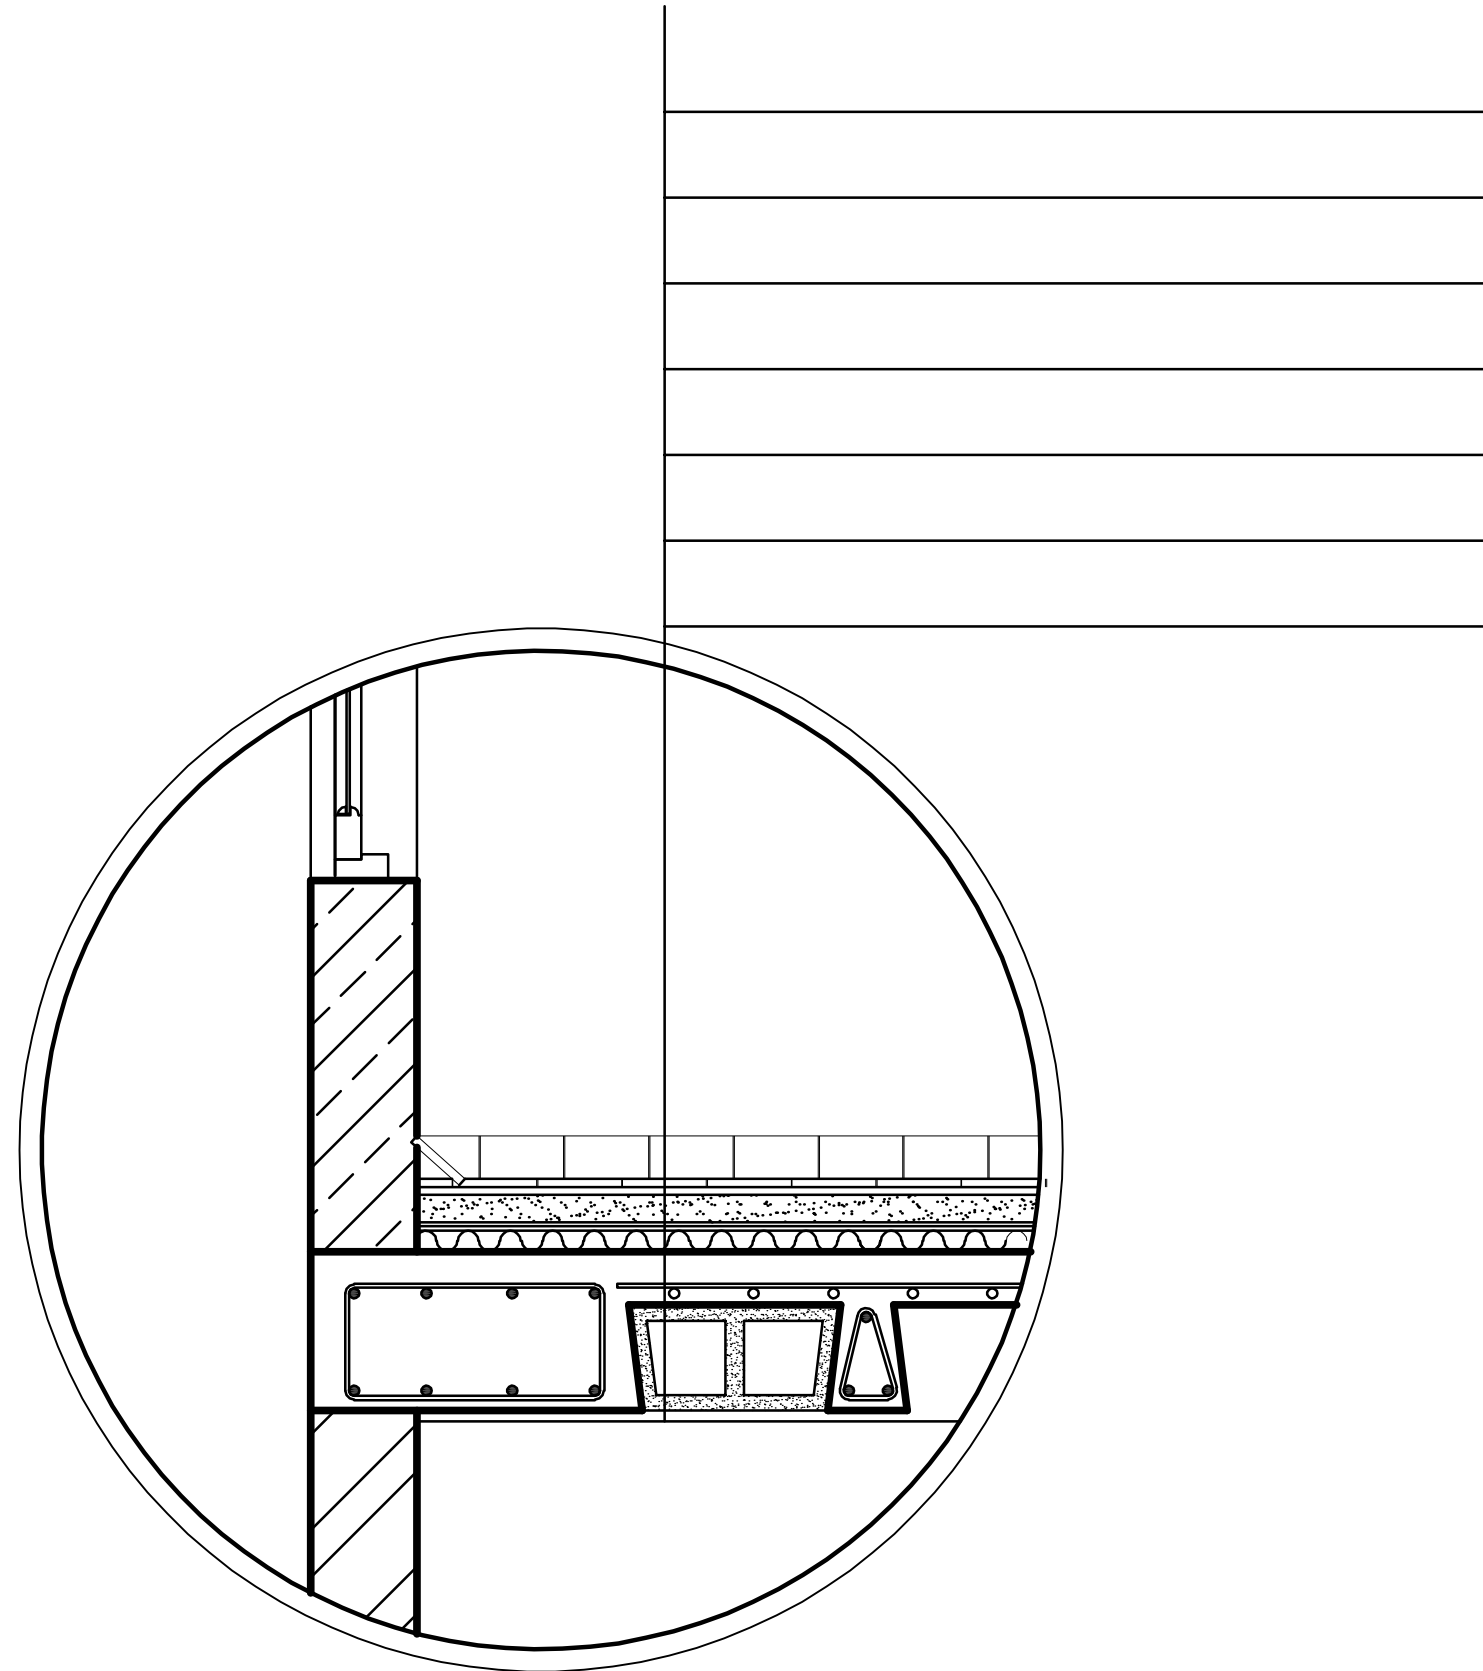


D11  
A-8

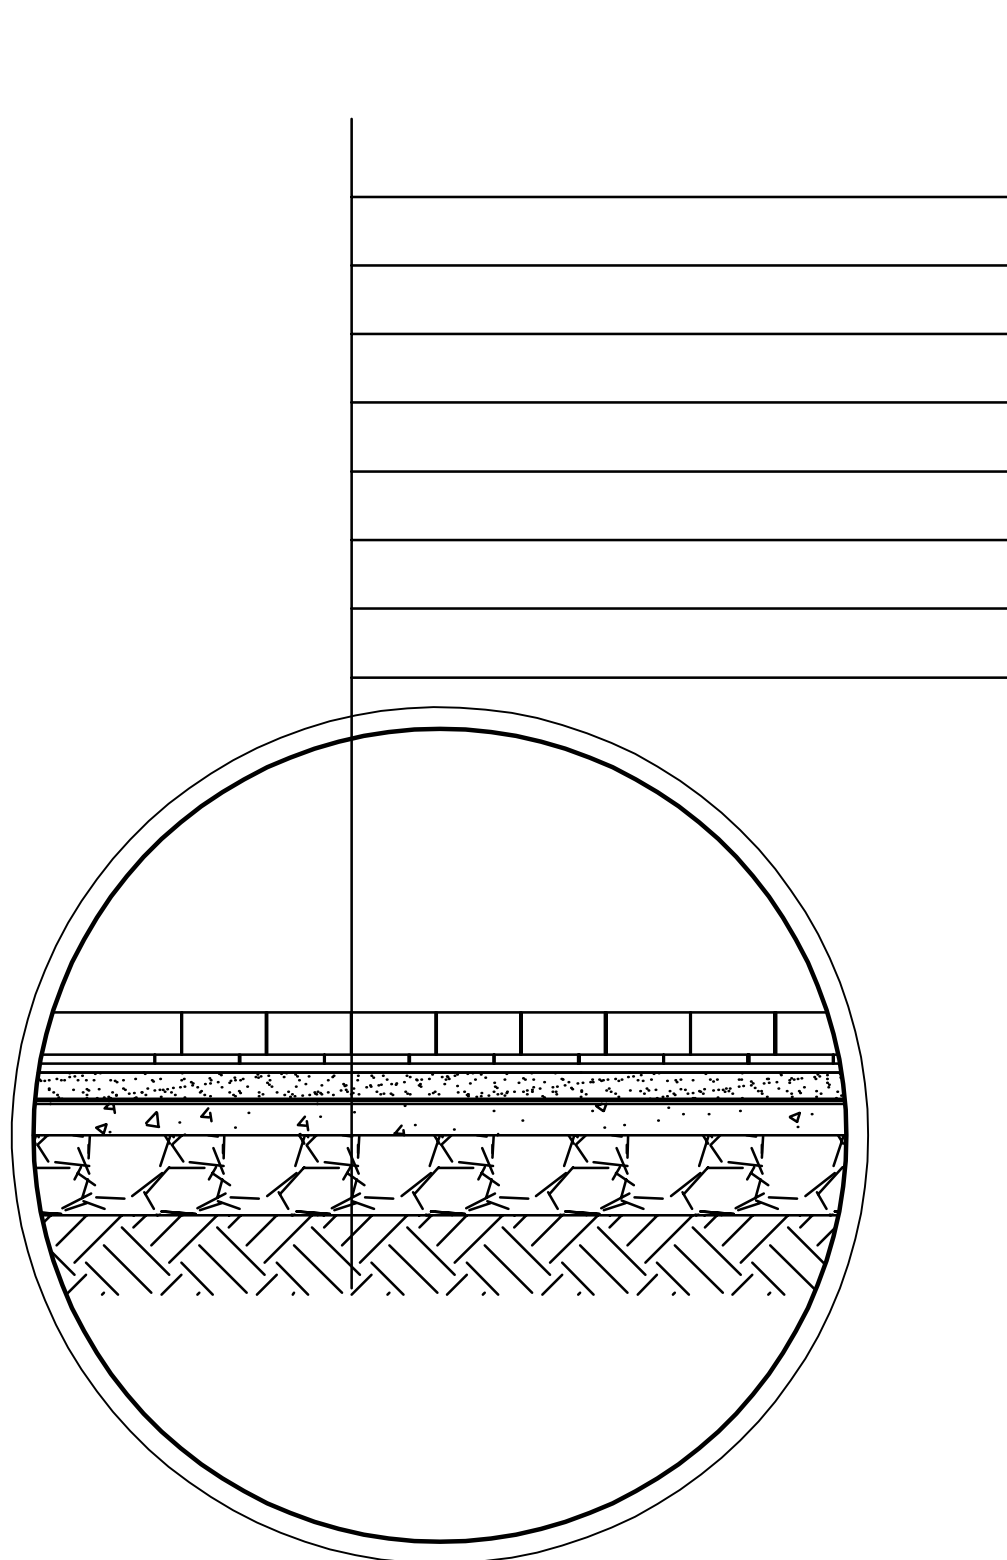


D8  
A-8

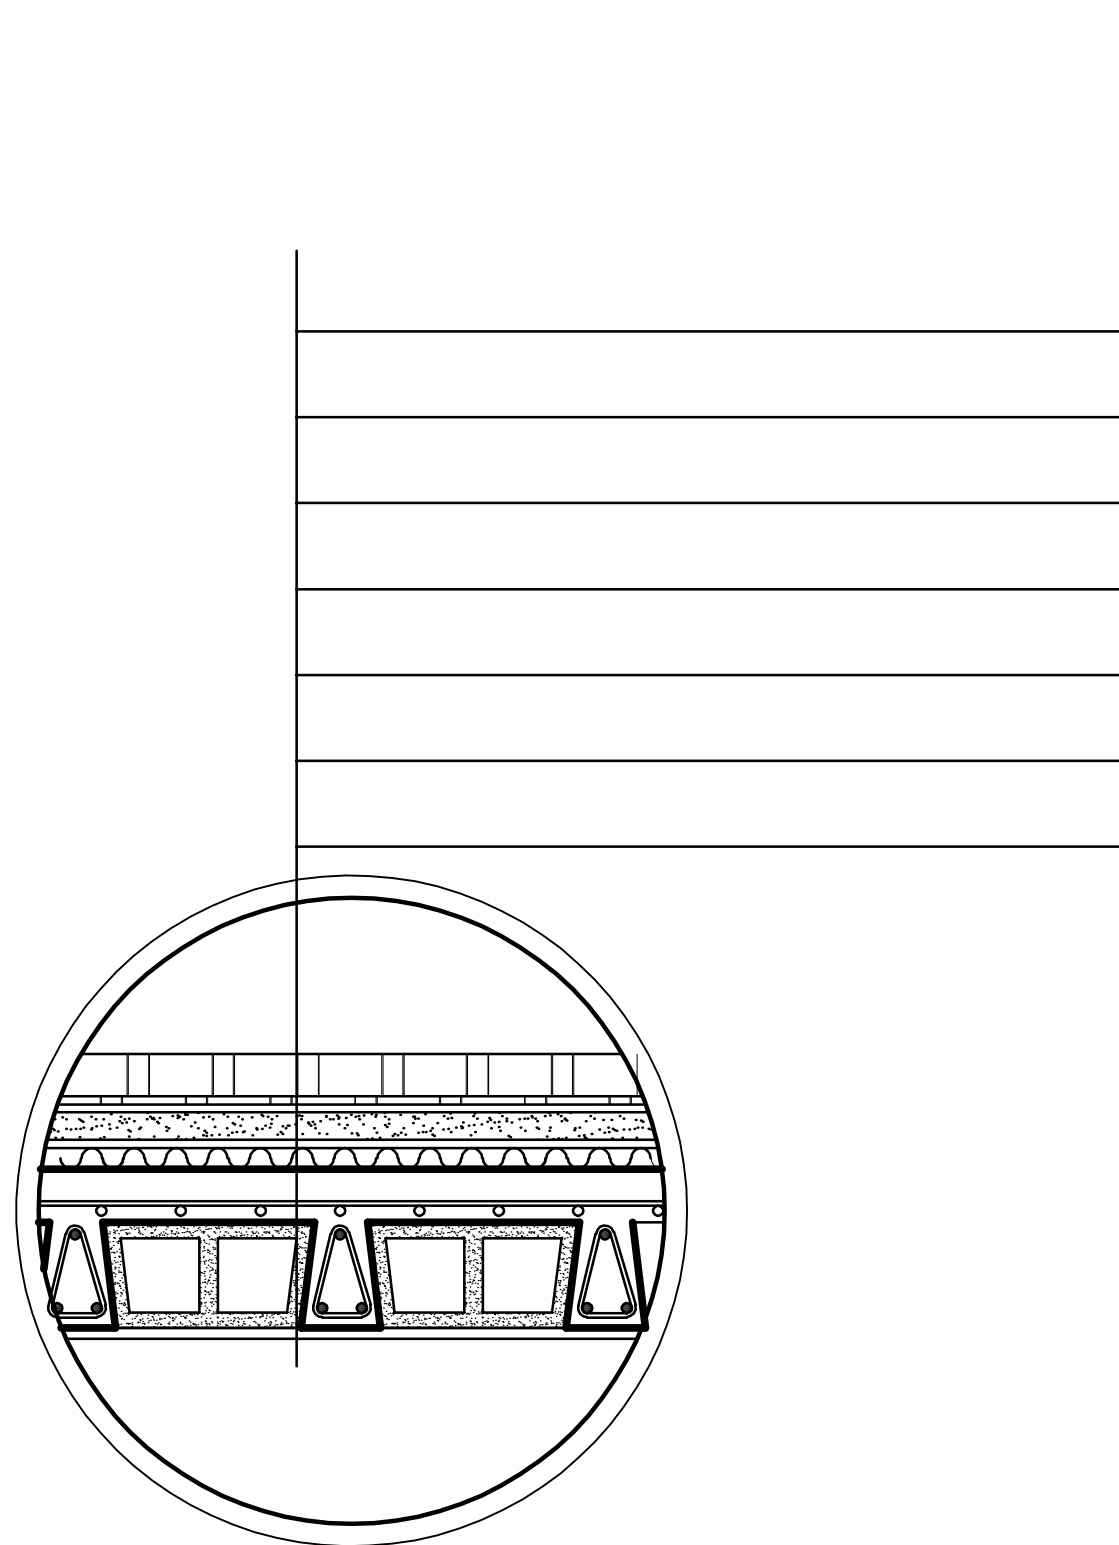


D7  
A-8

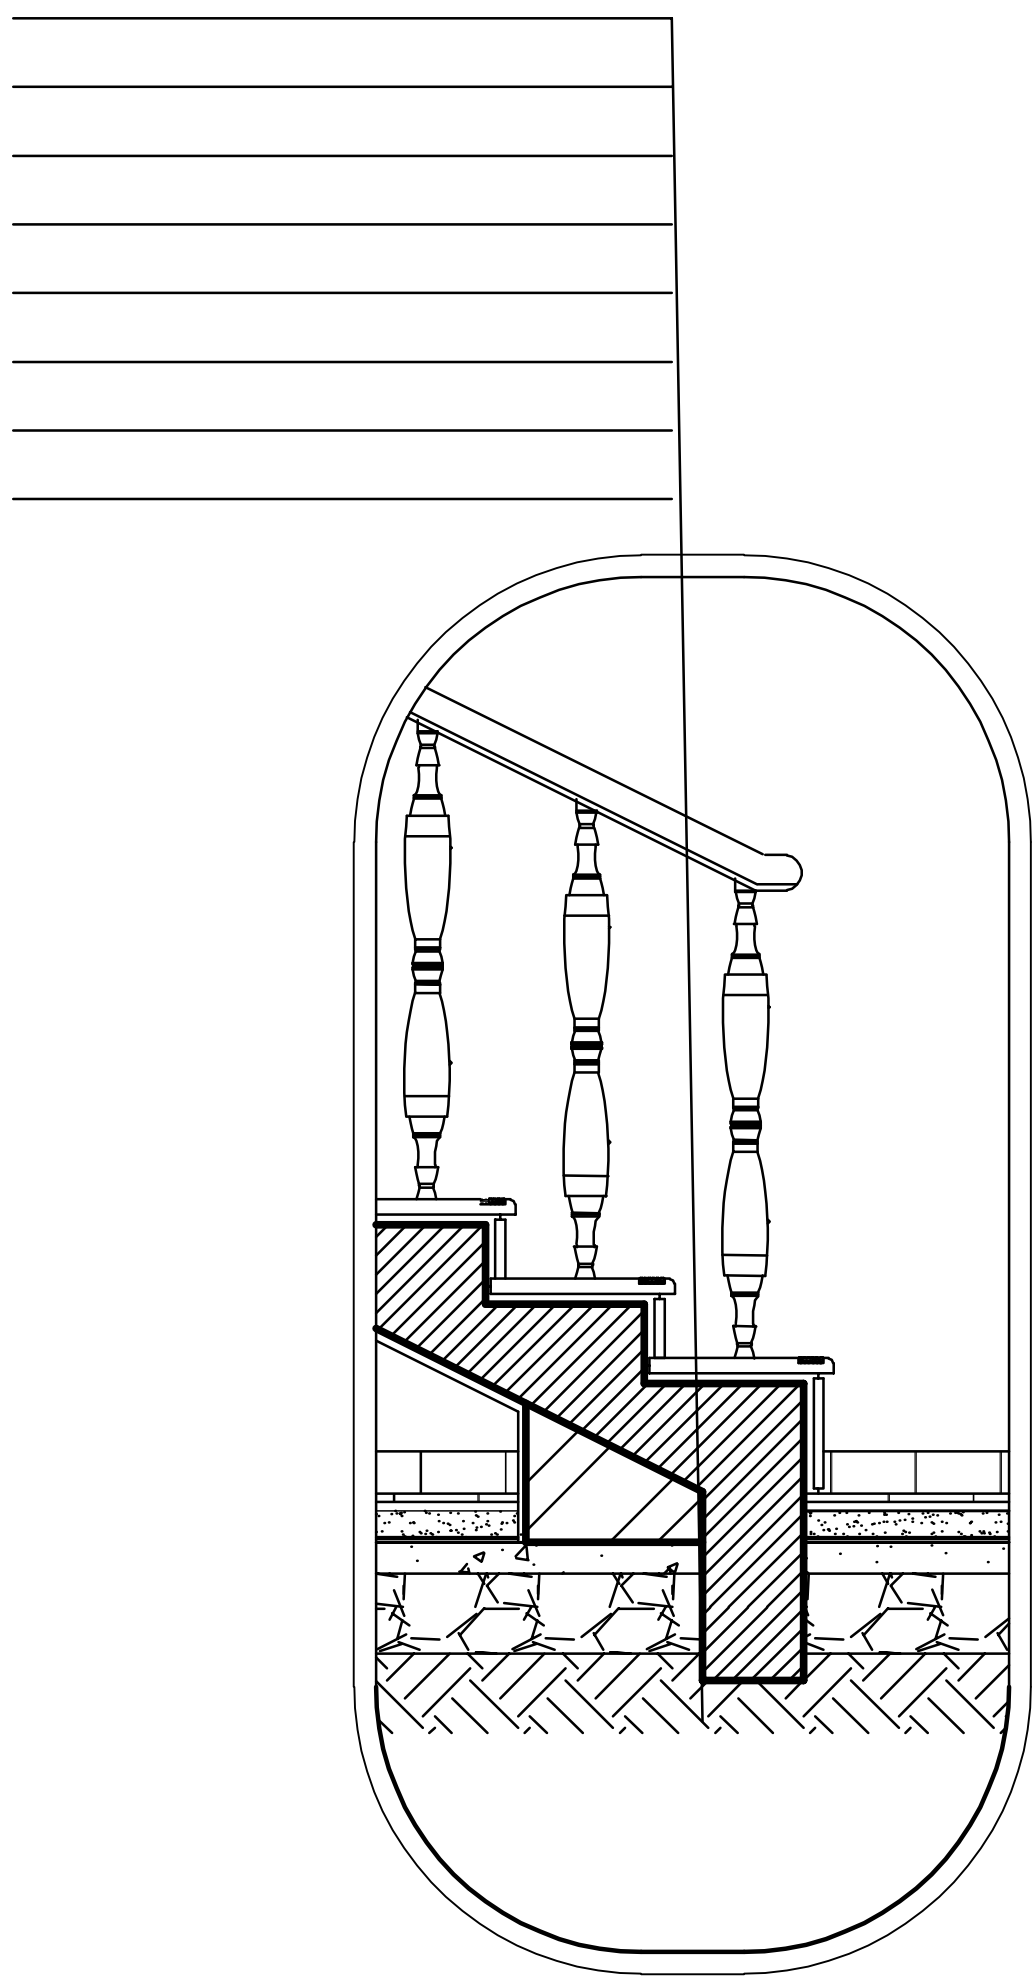


D10  
A-8

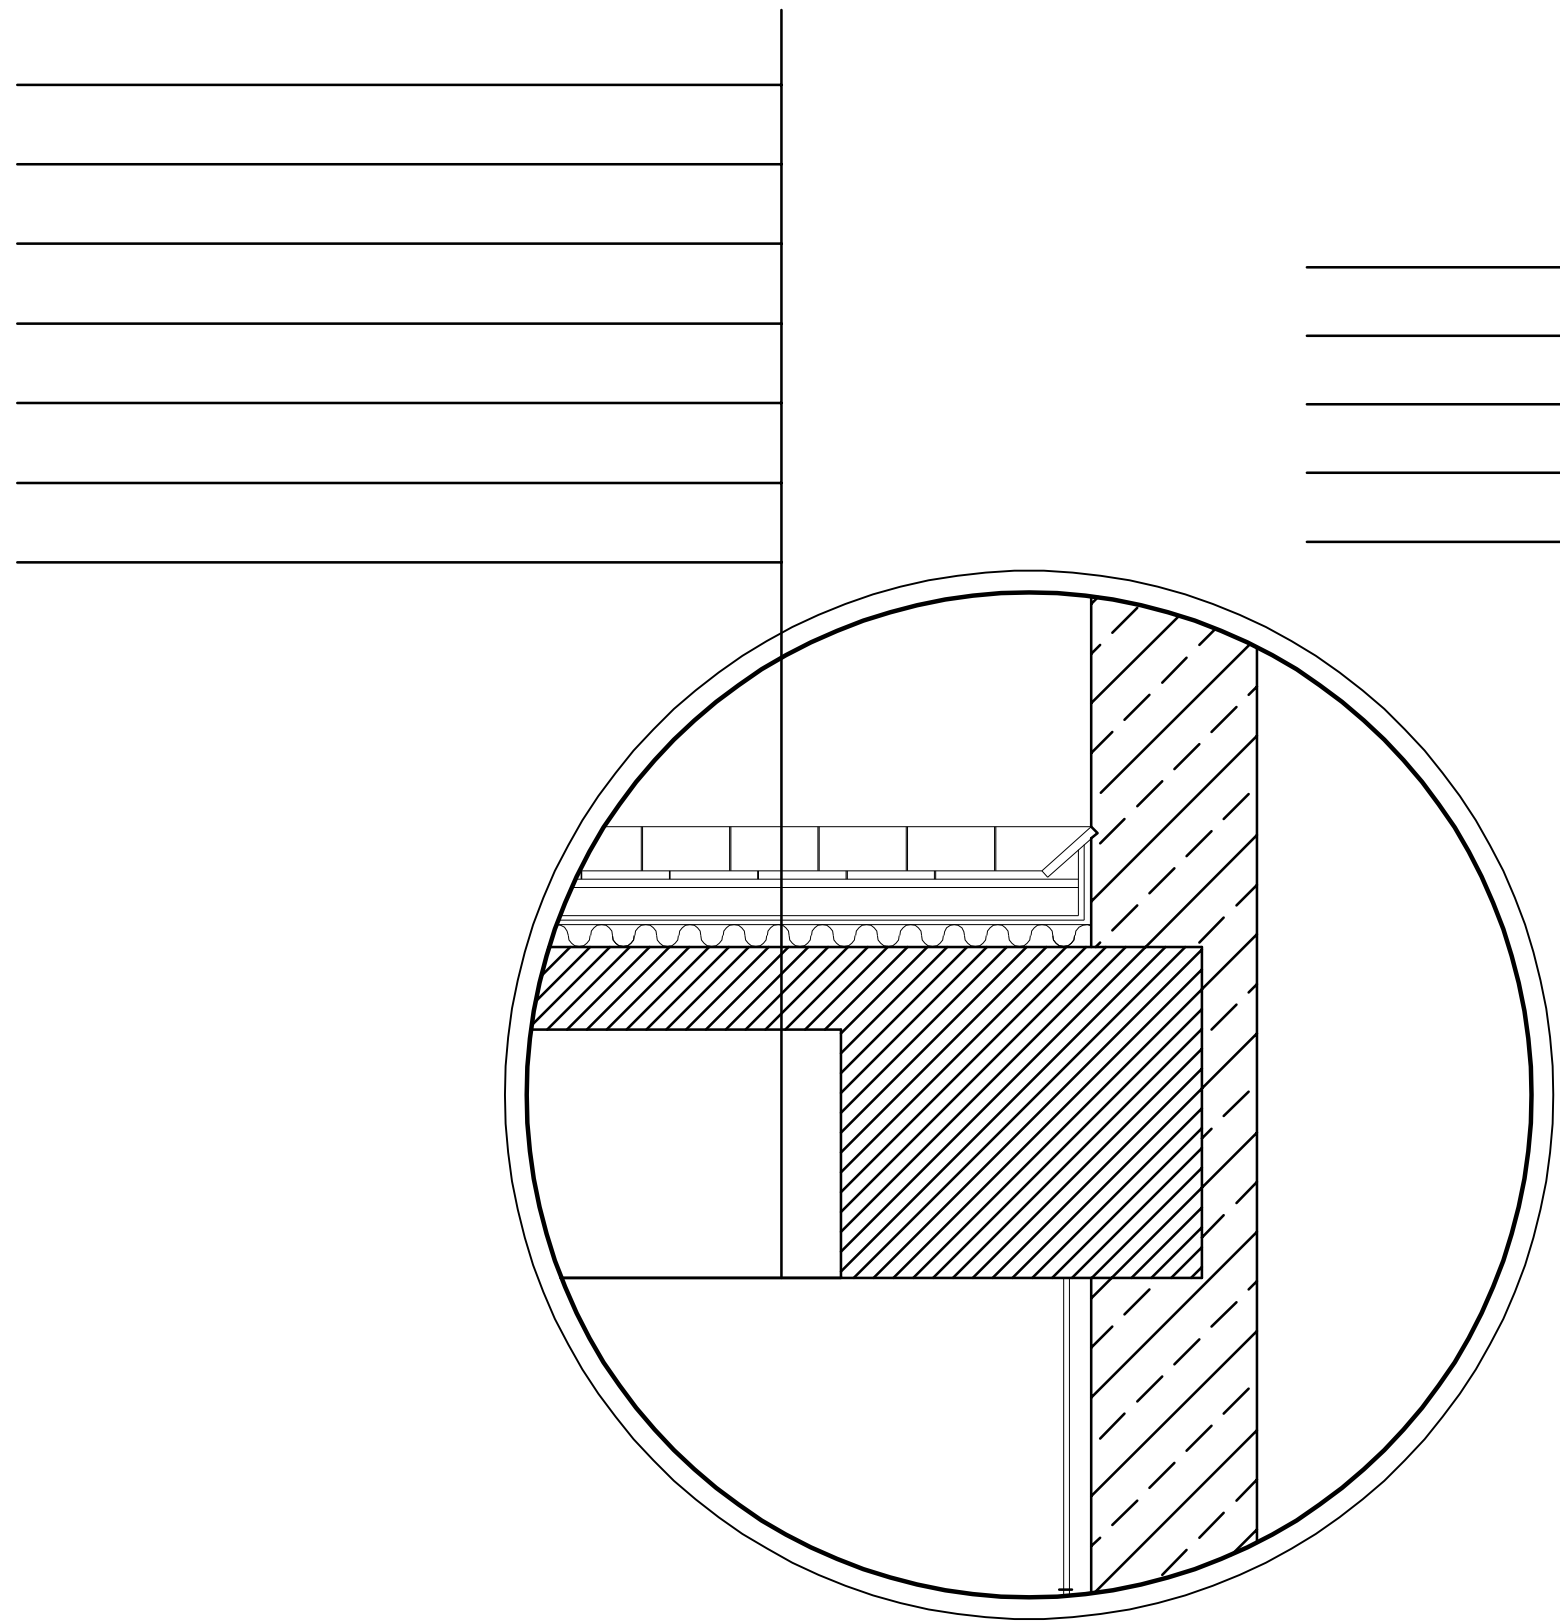

D1  
A-8

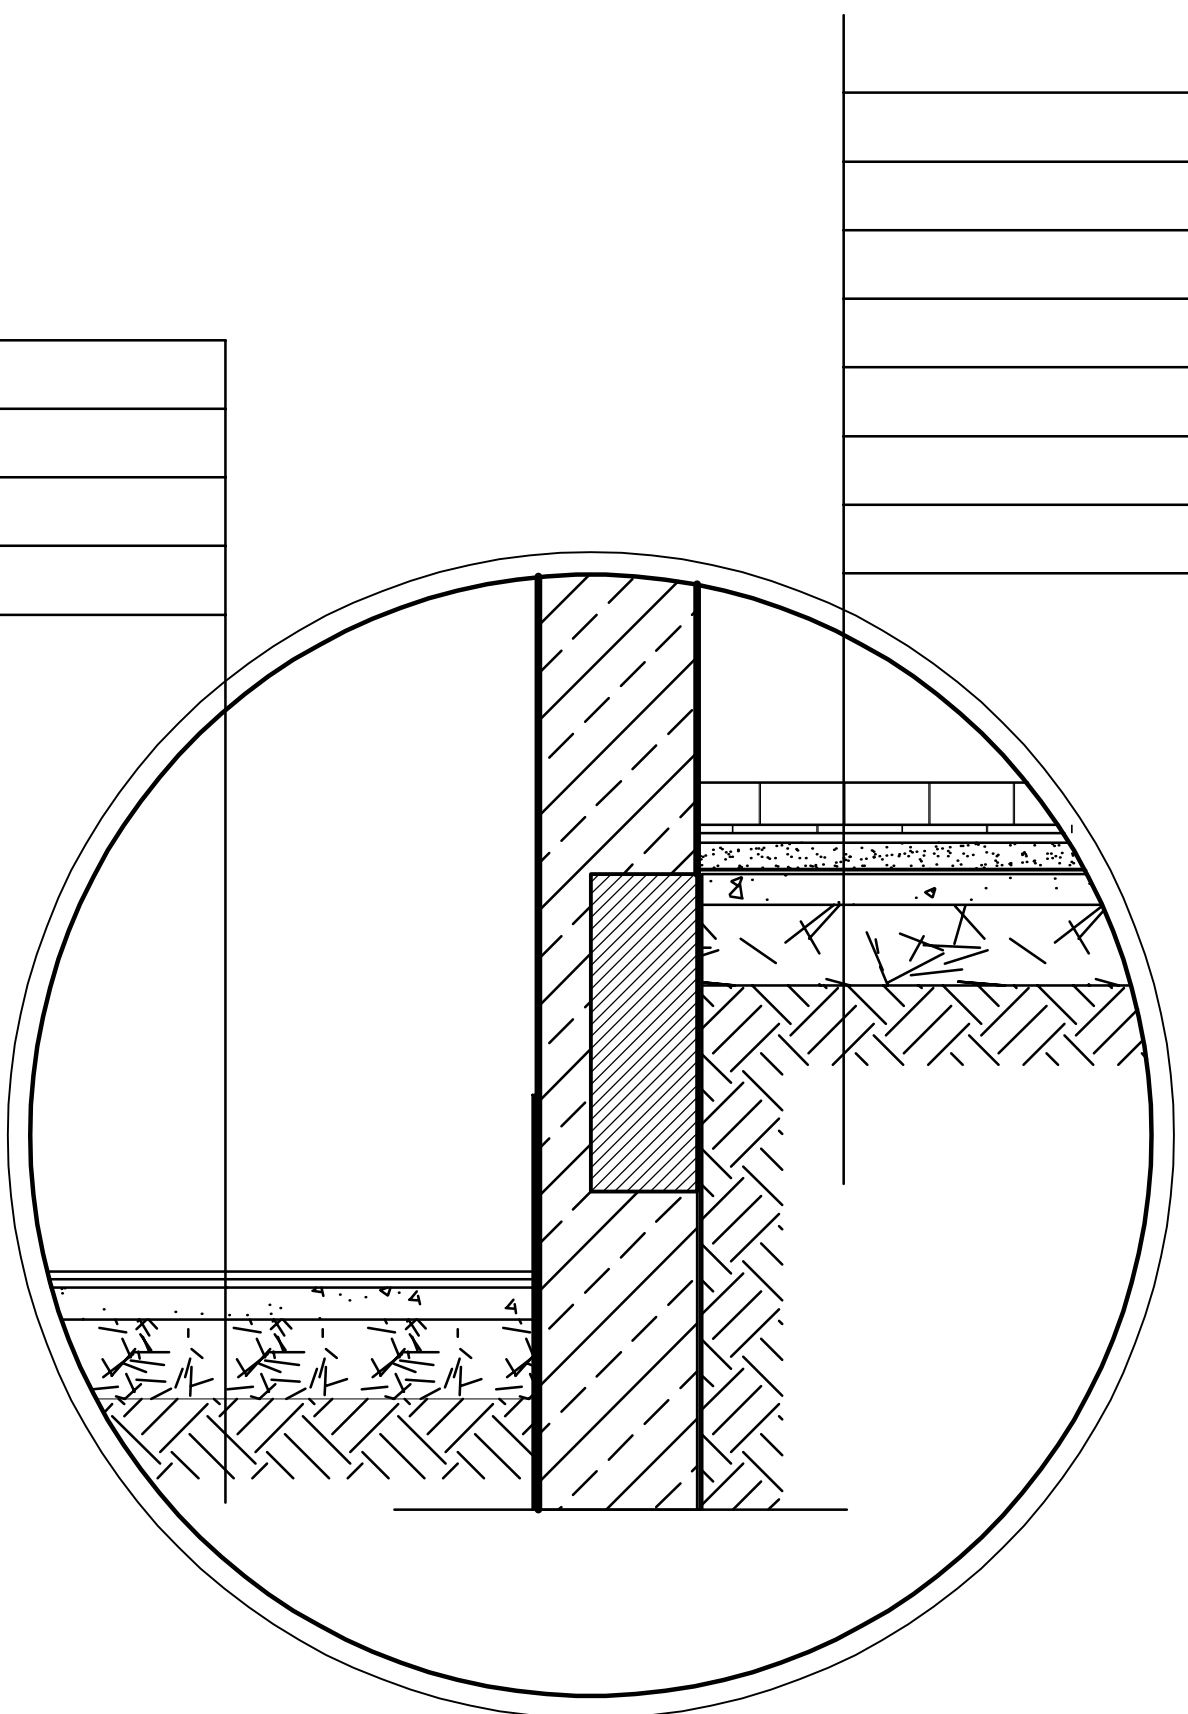

D6  
A-8

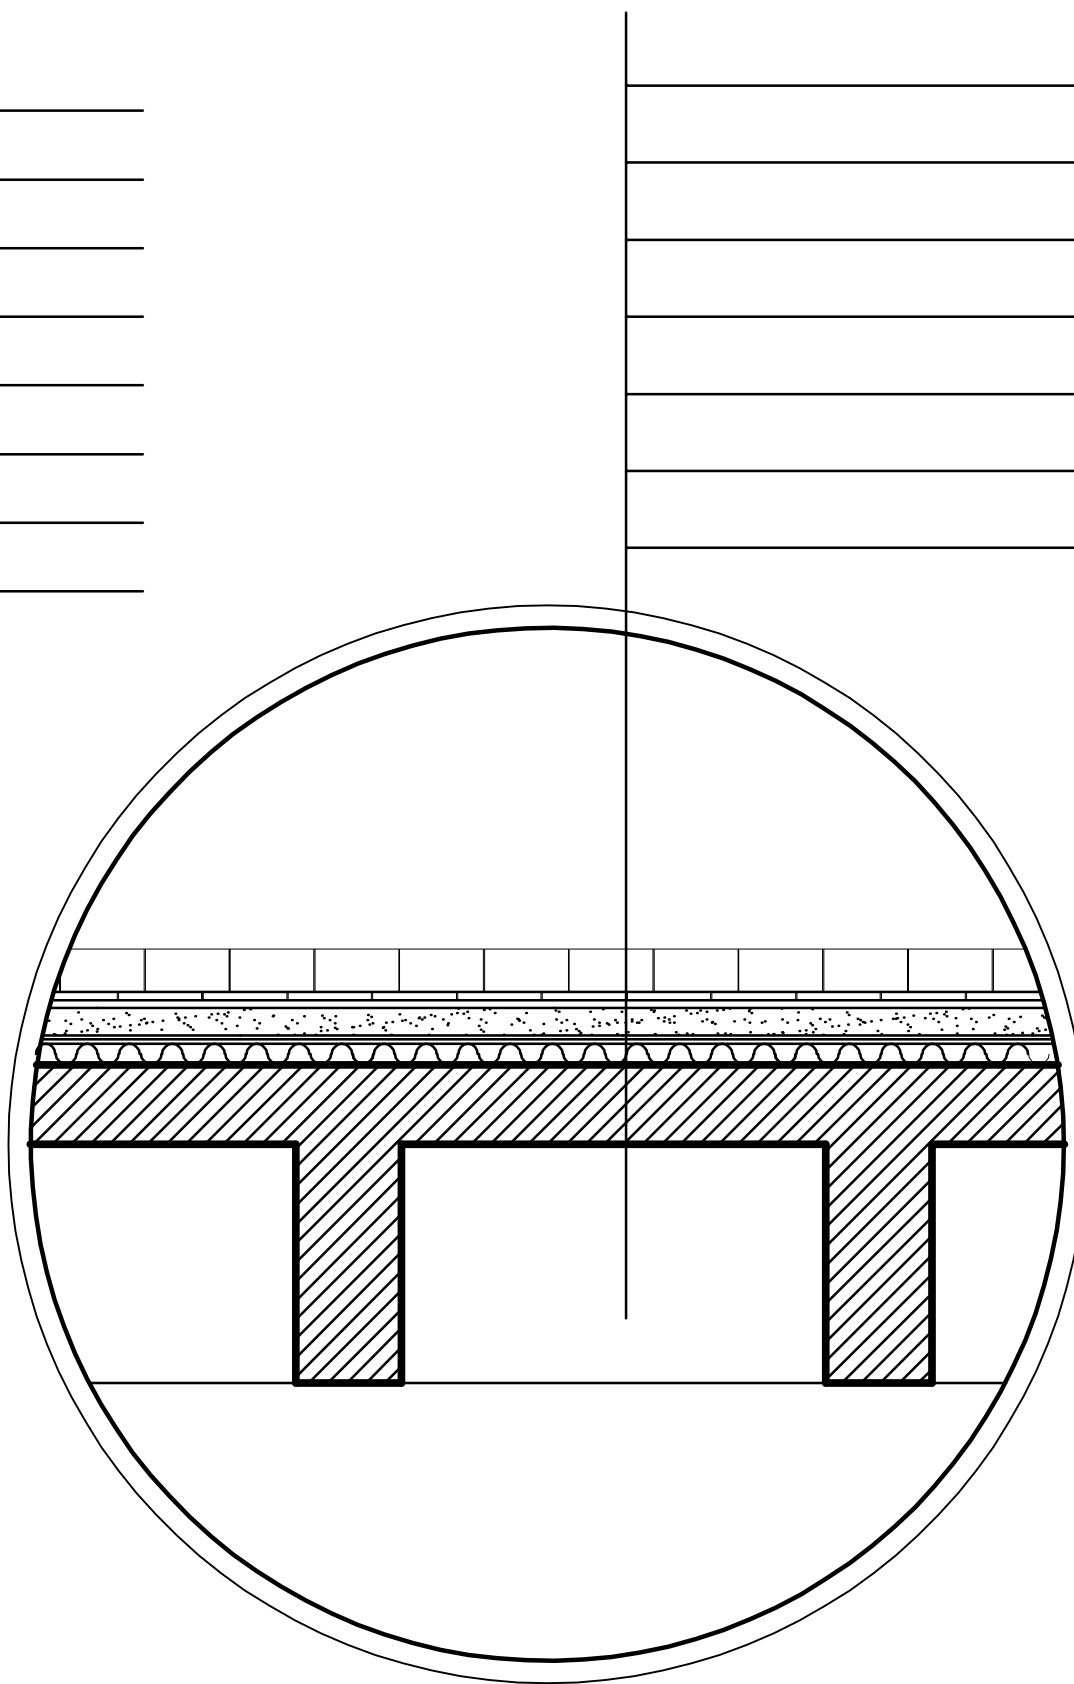

D2  
A-8