
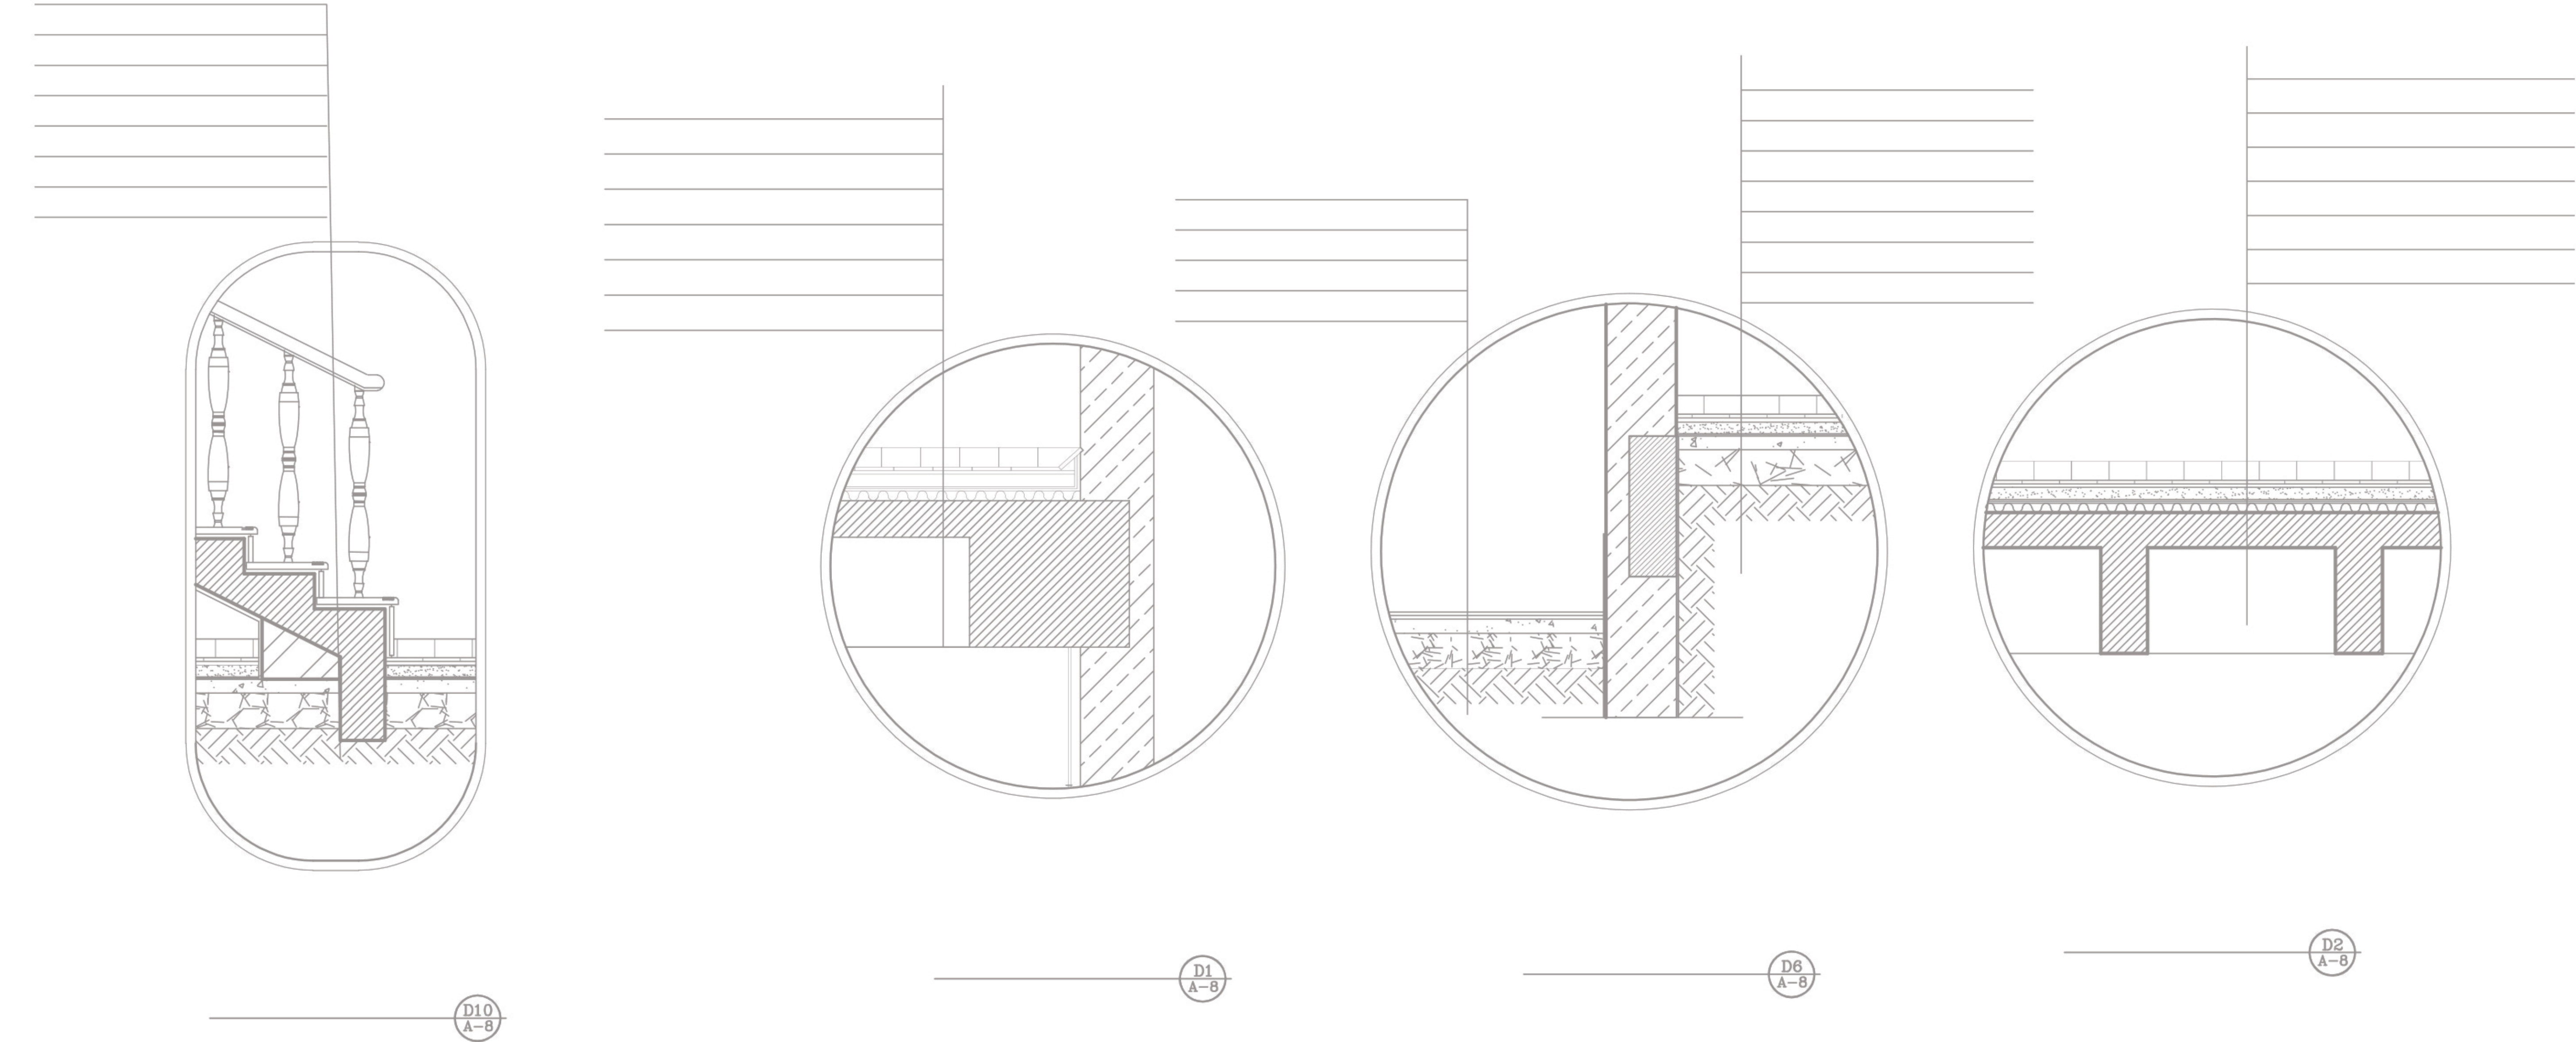


جامعة صنعاء
كلية الهندسة
قسم العمارة
سنة رابعة
نقطة خاصة

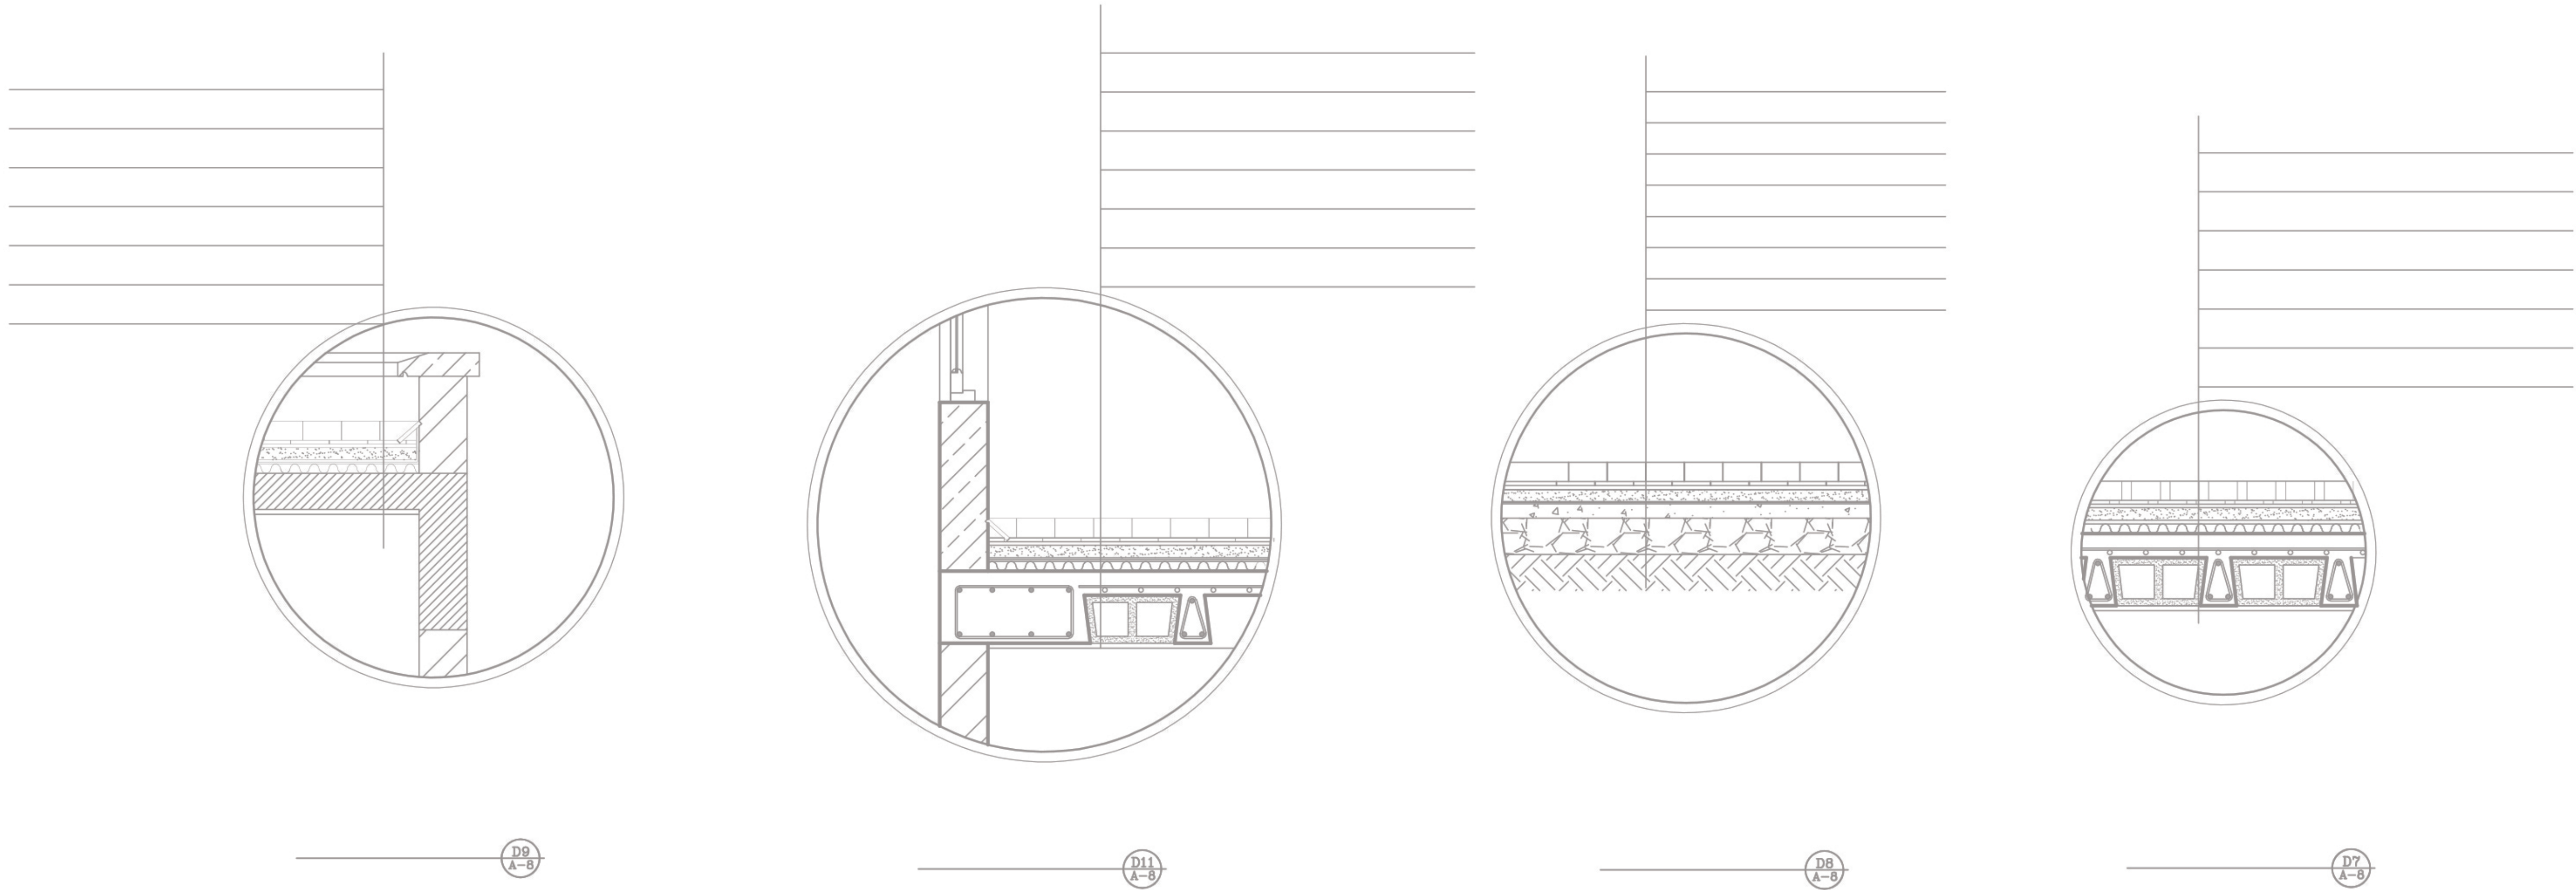

- خرسانه مسلحة
- حجر
- بلك
- رمل
- خرسانه عادية
- تسرجير
- تربة مدكوكة

احمد عبدالاله دهمش			تقديمه
اسم اللوحة	تفاصيل القطاعات	نوع اللوحة	تنقيح
رقم اللوحة	A-8	مقياس الرسم	1:10
اشرافه	د. محمد الوهاب القريشي م. اروي جباري م. حسام امين		