


جامعة صنعاء
كلية الهندسة
قسم العمارة
سنة رابعة
نقطة خاصة



جدول الرموز والمصطلحات الكهربائية

الرمز	التفاصيل
⚡	أمبير سنجل فيز و 10 مفاتيح اضاءة بقوة دائرتين وثلاث على التوالي
⚡	أمبير 10 مفاتيح اضاءة بقوة سنجل فيز دريكسون للسلالم
⚡	الجهزة اضاءة فلورسنت مزدوج بقدرة وات بالغطاء الأبيض 2*40
⚡	الجهزة اضاءة فلورسنت مربع بقدرة وات بعاكس من شرائح الالمنيوم 4*20
⚡	أجهزة اضاءة لايت سبوت دائري بقدرة 40 وات بالغطاء الابيض
⚡	أجهزة اضاءة موجهه سبوت لايت بقدرة وات بقاعدة متحركة 150
⚡	أجهزة اضاءة سبوت لايت بقدرة منخفضة لإضاءة درج المسرح
⚡	أمبير سنجل 13 مأخذ قوى كهربائية بقوة فيز بثلاث فتحات مع المفتاح
⚡	أمبير سنجل 15 مأخذ قوى كهربائية بقوة فيز بثلاث فتحات مع المفتاح
⚡	مدخل ميكرفون جداري مزدوج
⚡	مدخل ميكرفون ارضي مفرد
⚡	13 أمبير سنجل فيز بثلاث فتحات مع الغطاء مأخذ قوى كهربائية ارضي بقوة
⚡	مفتاح التحكم بالفصل والتشغيل
⚡	أمبير سنجل فيز 30 لوحات التكييف بقوة مأخذ تلفونات
⚡	لوحة توزيع فر عية بموجب المواصفات
⚡	لوحة توزيع فر عية خاصة بلاضاءة الخارجية وبموجب المواصفات
⚡	لوحة التوزيع الرئيسية وبموجب المواصفات
⚡	لوحة التحكم بالأجهزة الصوتية في المسرح بطول واحد (بولار) أعمدة اضاءة حدائقية نوع مع لمبة فلورسنت - متر
⚡	مع البليت والانكربولت - إقتصادية
⚡	سماعة علوية نوع بايونير 7000 وات
⚡	سماعة علوية نوع بايونير 3000 وات

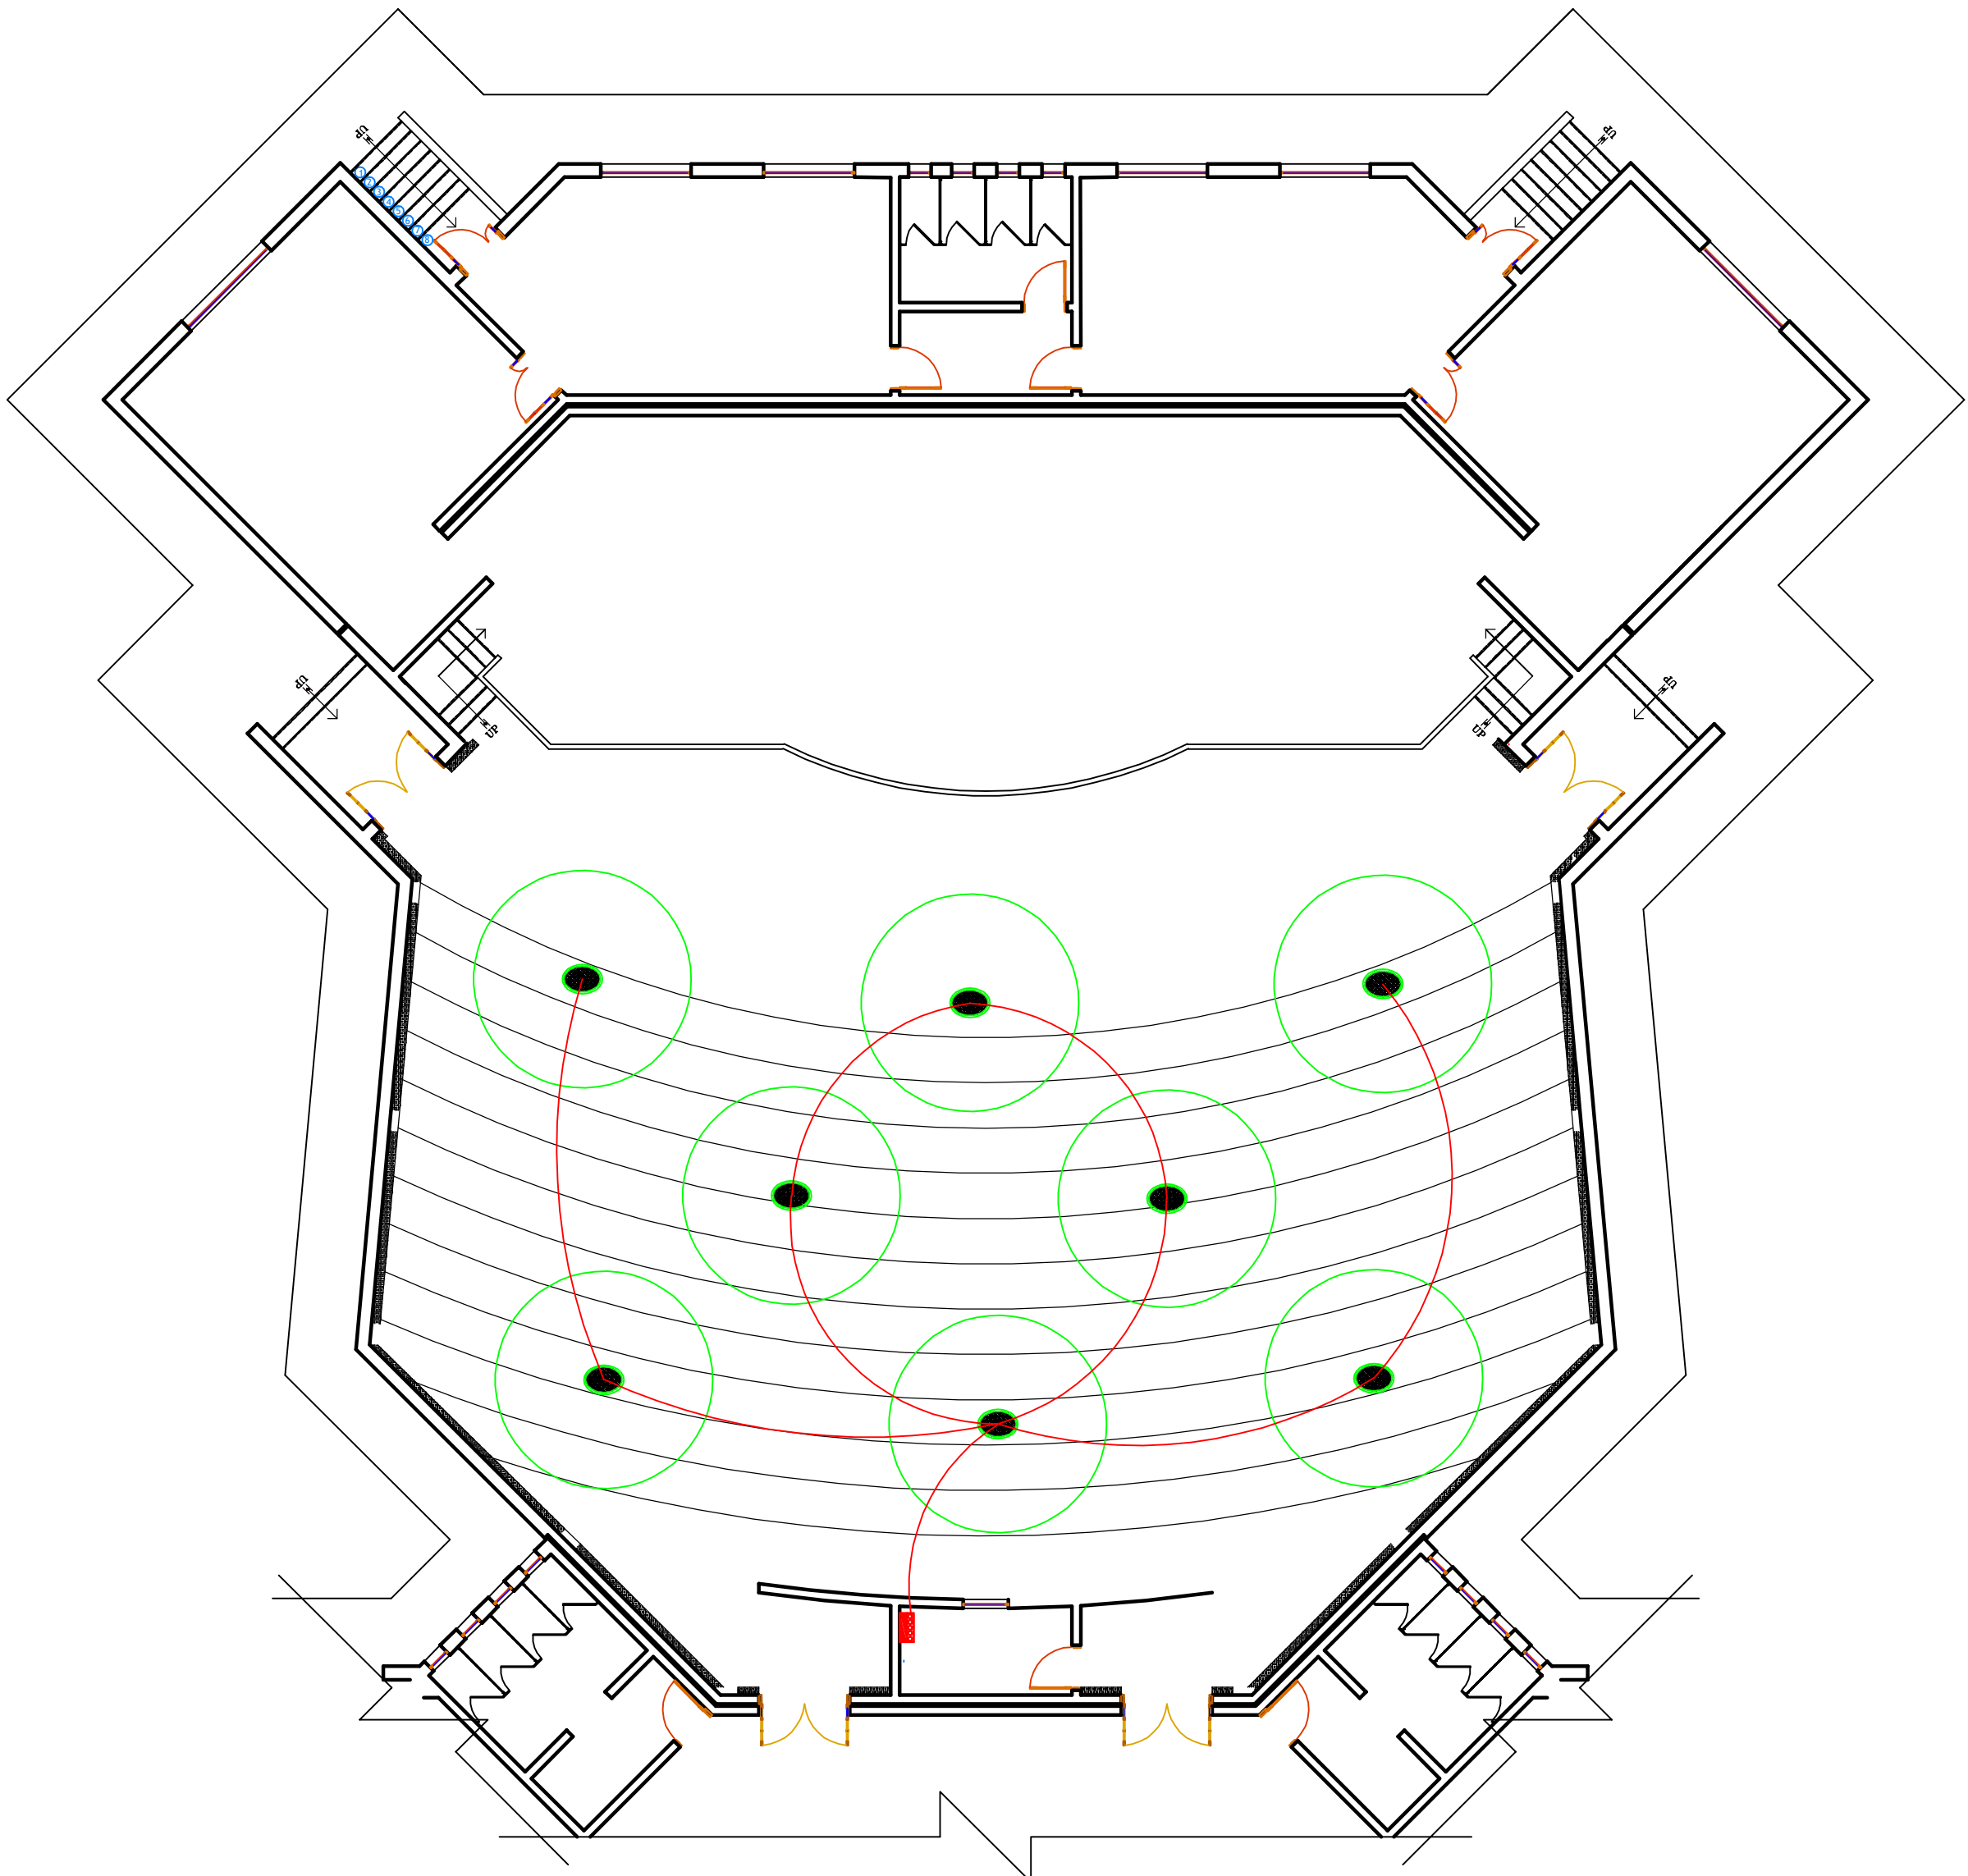

شعريانية صوتية المسرح
مقياس رسم 100/1

تقديم	احمد عبدالاله دهمش		
اسم اللوحة	شعريانية اضاءة المسرح	نوع اللوحة	تنفيذية
رقم اللوحة	A-7	مقياس الرسم	1:100
اشرافه	د. محمد الوهاب الترشدي م. اروي جباري م. حسام امين		