


جامعة صنعاء
كلية الهندسة
قسم العمارة
سنة رابعة
نقطة خاصة



جدول الرموز والمصطلحات الكهربائية

الرمز	التفاصيل
	أمبير سنجل فيزو 10 مفاتيح اضاءة بقوة دائرتين وثلاث على التوالي
	أمبير 10 مفاتيح اضاءة بقوة سنجل فيز دريكسون للسلام
	أجهزة اضاءة فلورسنت مزدوج بقدرة وات بالغطاء الأبيض 2*40
	أجهزة اضاءة فلورسنت مربع بقدرة وات بعكس من شرائح الألمنيوم 4*20
	أجهزة اضاءة لايت سيوت دائري بقدرة 40 وات بالغطاء الابيض
	أجهزة اضاءة موجهة سيوت لايت بقدرة وات بقاعدة متحركة 150
	أجهزة اضاءة سيوت لايت بقدرة منخفضة لإضاءة درج المسرح
	أمبير سنجل 13 مأخذ قوى كهربائية بقوة فيز بثلاث فتحات مع المفتاح
	أمبير سنجل 15 مأخذ قوى كهربائية بقوة فيز بثلاث فتحات مع المفتاح
	مدخل ميكرفون جداري مزدوج
	مدخل ميكرفون ارضي مفرد
	13 أمبير سنجل فيز بثلاث فتحات مع الغطاء مأخذ قوى كهربائية ارضي بقوة
	مفتاح التحكم بالفصل والتشغيل
	أمبير سنجل فيز 30 لوحات التكيف بقوة مأخذ تلفونات
	لوحة توزيع فرعية بموجب المواصفات
	لوحة توزيع فرعية خاصة بالضاءة الخارجية وبموجب المواصفات
	لوحة التوزيع الرئيسية وبموجب المواصفات
	لوحة التحكم بالأجهزة الصوتية في المسرح بطول واحد (بولار) أعمدة اضاءة حدائقية نوع مع لمبة فلورسنت - متر مع البليت والانكربولت - إقتصادية

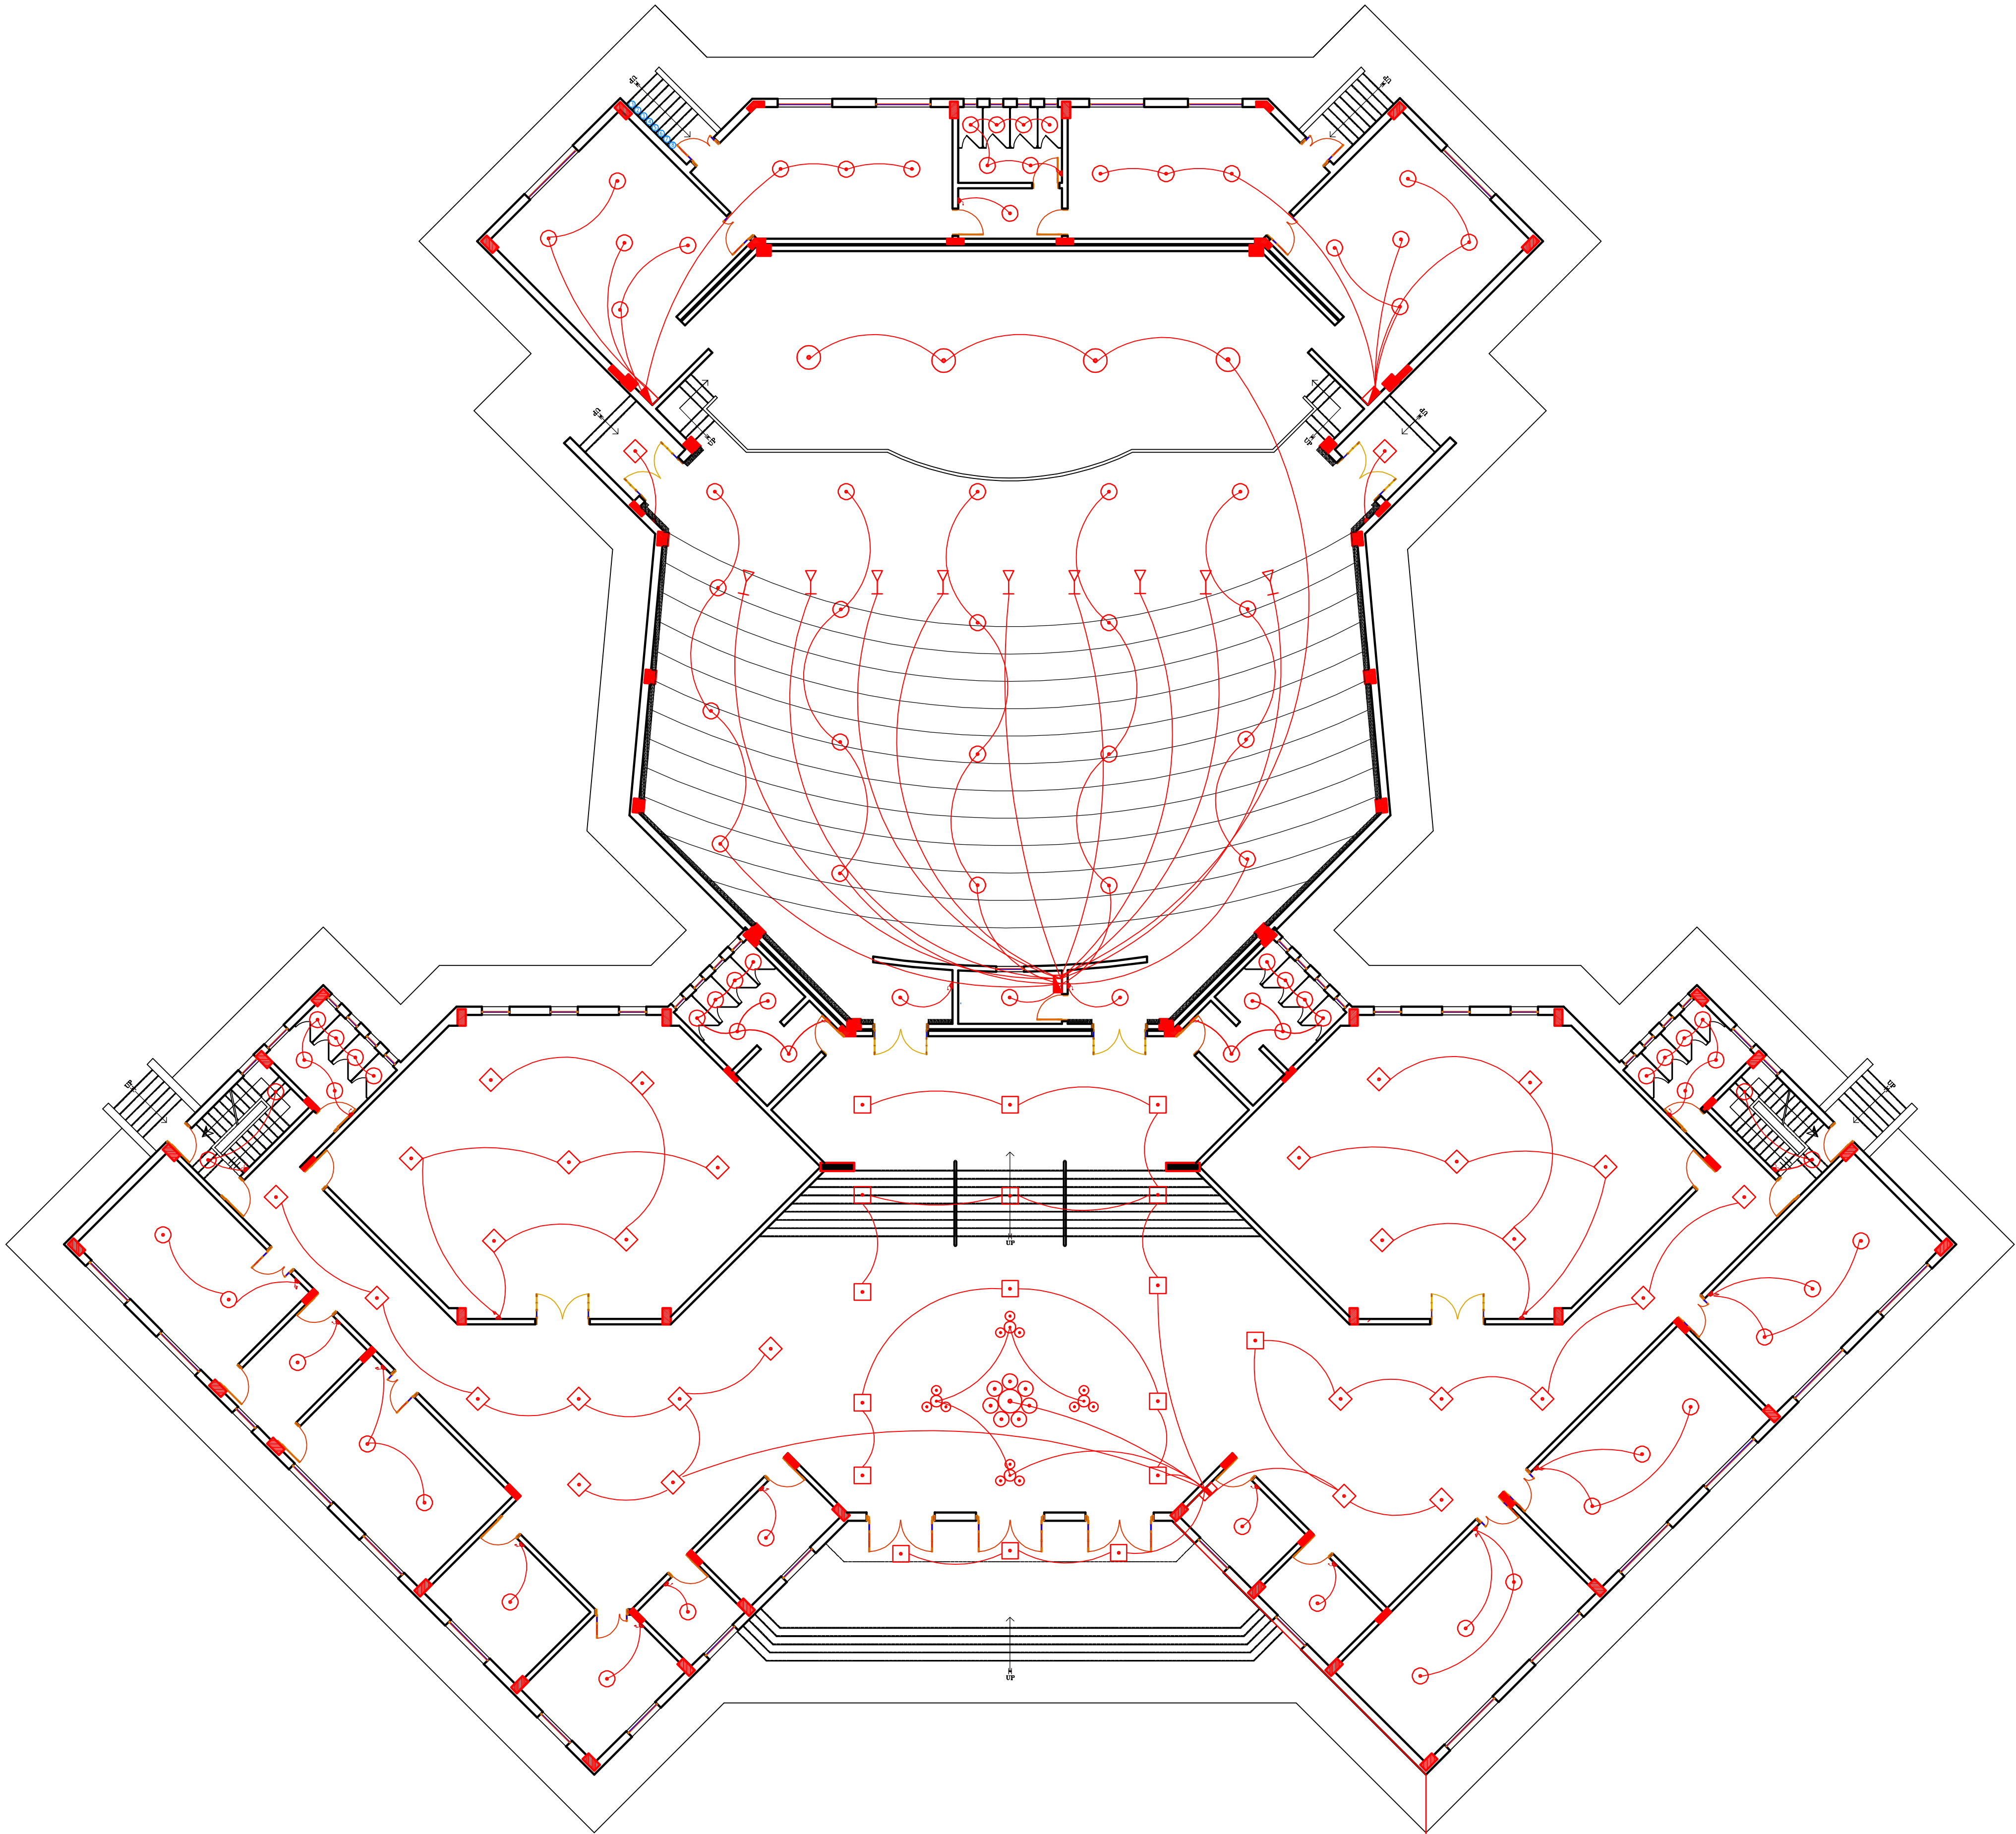

مقياس رسم 100/1
A-6

خط التغذية بالكهرباء

تقديم	احمد عبدالاله دهمش
اسم اللوحة	مخططية اضاءة
رقم اللوحة	A-6
مقياس الرسم	1:100
اشرافه	د. محمد الوهابي الشرفي م. اروي جباري م. حسام امين