


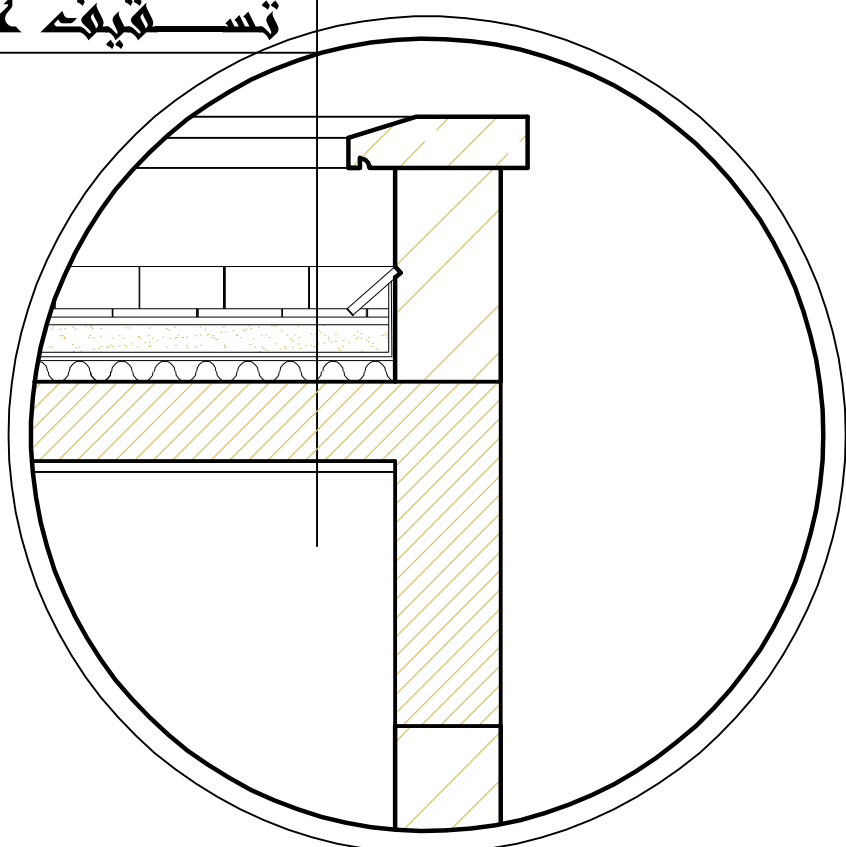


وزرة موزايكو 2*30*15 cm
بلاط موزايكو 2*25*25 cm
مونه اسمنتية 2 cm
رمل تسويه 5 cm
عازل للرطوبة 1 cm
عازل حرارة 5 cm
تسقيف عادي 15 cm




التفصيلة رقم 8
مقياس رسم 10/1

وزرة موزايكو 2*30*15 cm
بلاط موزايكو 2*25*25 cm
مونه اسمنتية 2 cm
رمل تسويه 5 cm
عازل للرطوبة 2 mm
عازل حرارة 5 cm
تسقيف موردي 30 cm

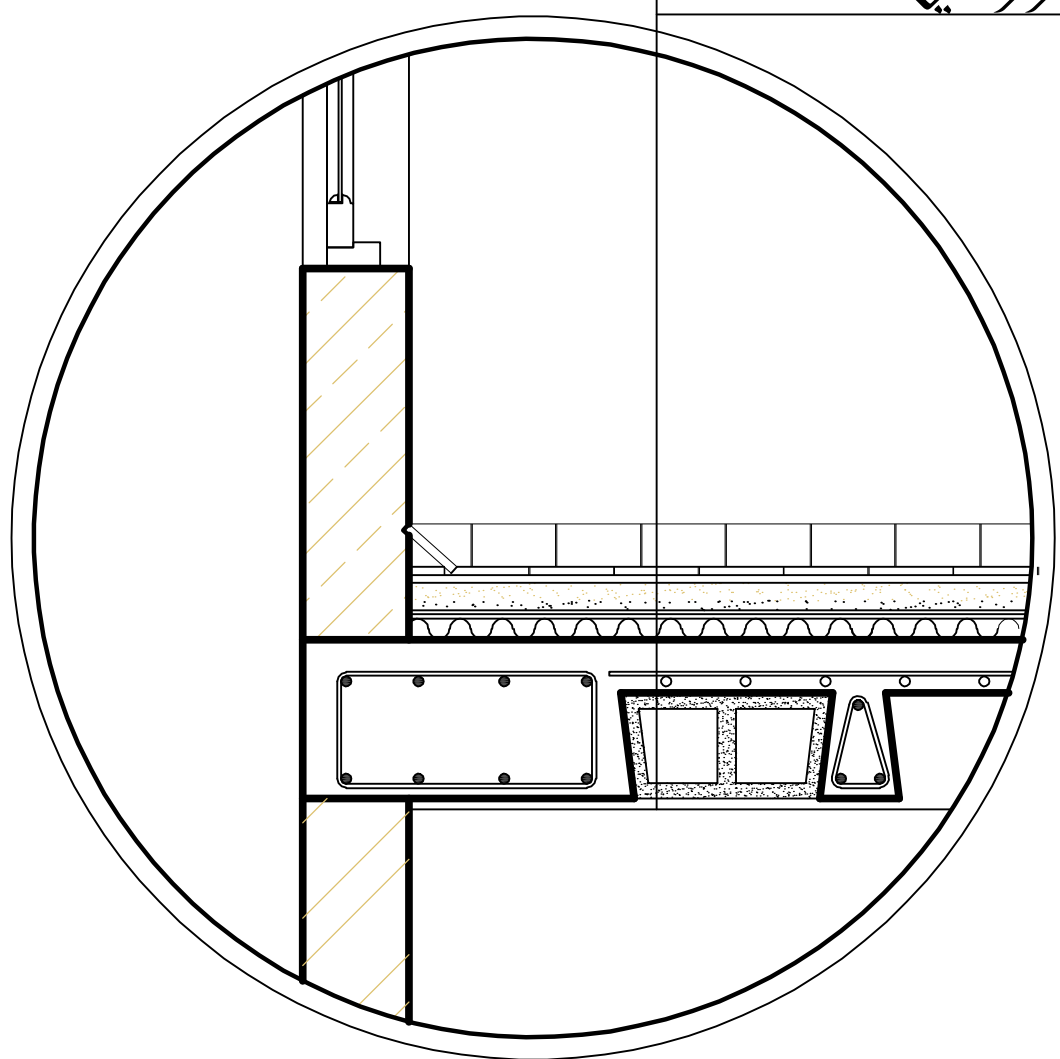


التفصيلة رقم 10
مقياس رسم 10/1

وزرة سيراميك 1*30*15 cm
بلاط موزايكو 2*25*25 cm
مونه اسمنتية 2 cm
رمل تسويه 5 cm
عازل للرطوبة 2 mm
خرسانه عادية 15 cm
كسر حجر 15 cm
تربه مدكوكه

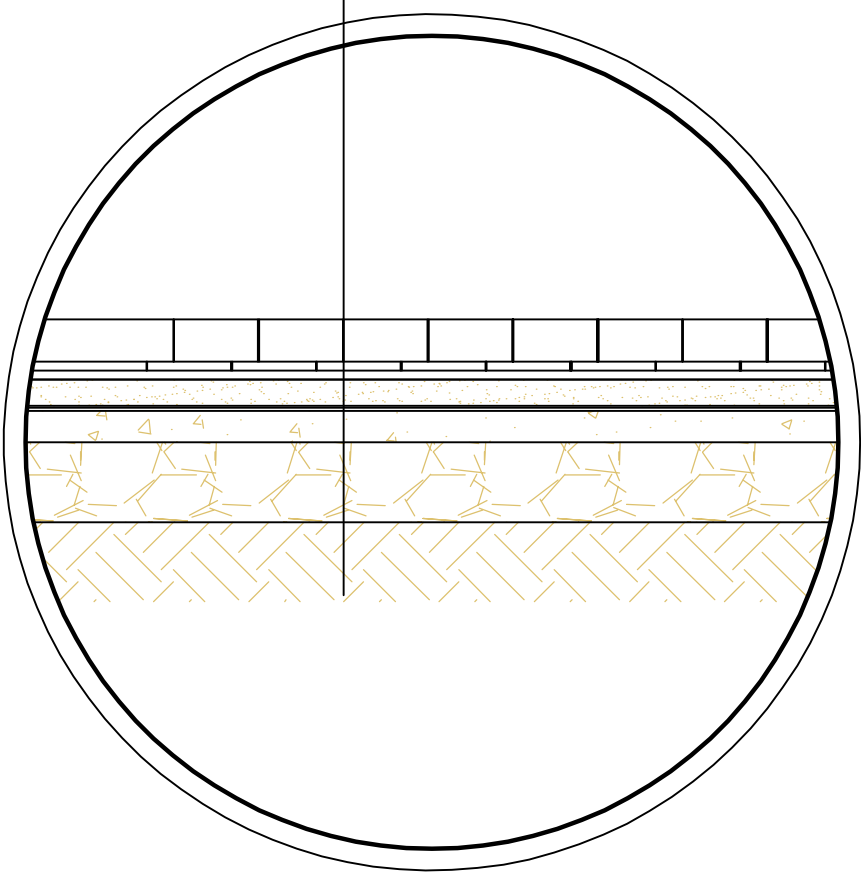


التفصيلة رقم 7
مقياس رسم 10/1

وزرة موزايكو 2*30*15 cm
بلاط موزايكو 2*25*25 cm
مونه اسمنتية 2 cm
رمل تسويه 5 cm
عازل للرطوبة 2 mm
عازل حرارة 5 cm
تسقيف موردي 30 cm

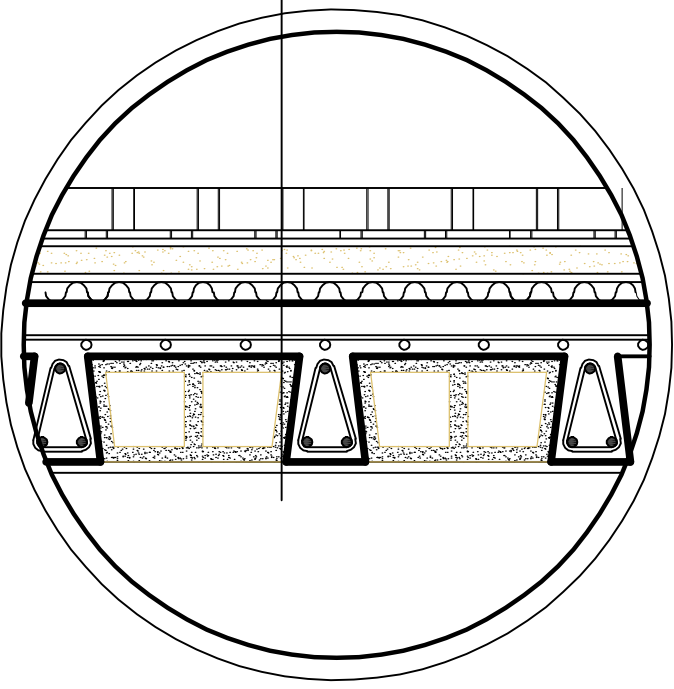


التفصيلة رقم 6
مقياس رسم 10/1

وزرة سيراميك 1*30*15 cm
بلاط سيراميك 0.5*20*20cm
مونه اسمنتية 2 cm
عازل للرطوبة 2 mm
خرسانه عادية 15 cm
كسر حجر 15 cm
تربه مدكوكه

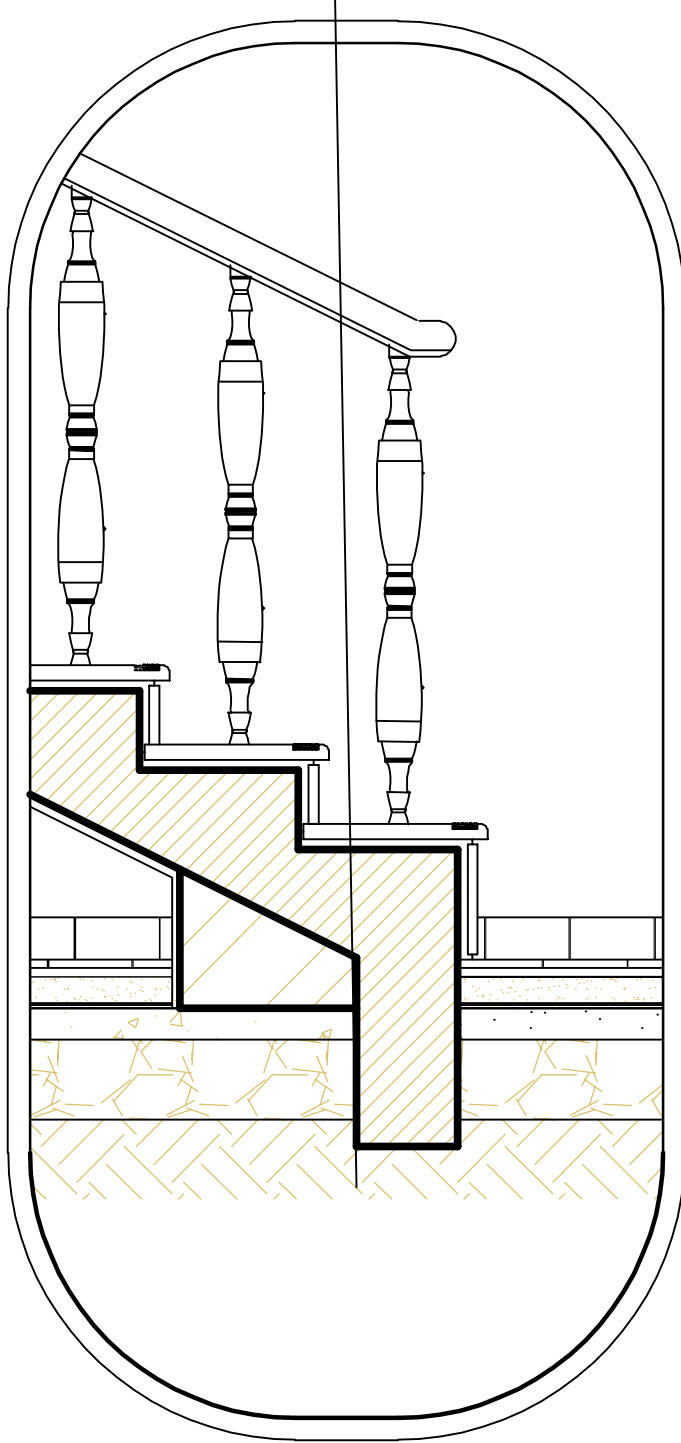


التفصيلة رقم 9
مقياس رسم 10/1

وزرة موزايكو 2*30*15 cm
بلاط موزايكو 2*25*25 cm
مونه اسمنتية 2 cm
رمل تسويه 5 cm
عازل للرطوبة 1 cm
عازل حرارة 5 cm
تسقيف شبكي 60 cm

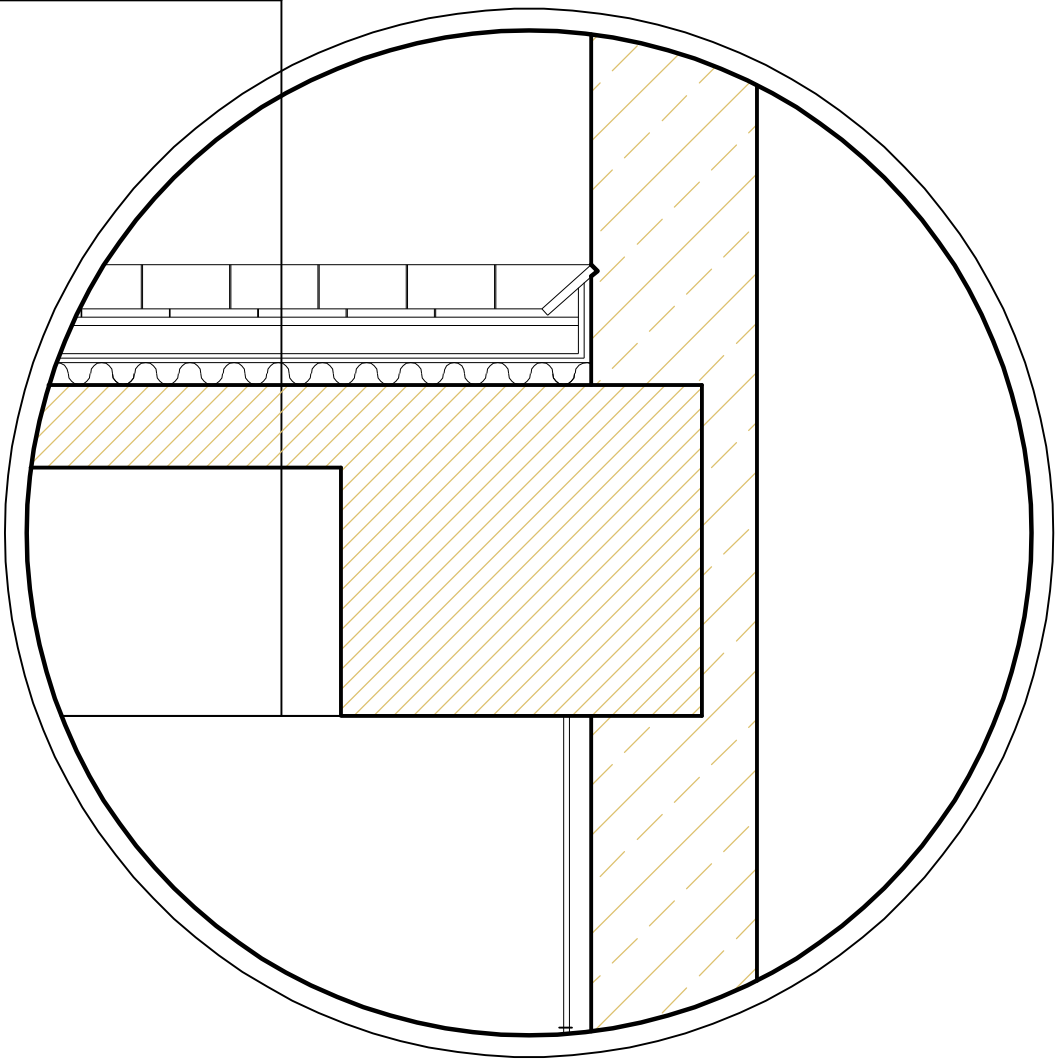


التفصيلة رقم 1
مقياس رسم 10/1

بلاط موزايكو 2*25*25 cm
مونه اسمنتية 2 cm
خرسانه عادية 15 cm
كسر حجر 15 cm
تربه مدكوكه

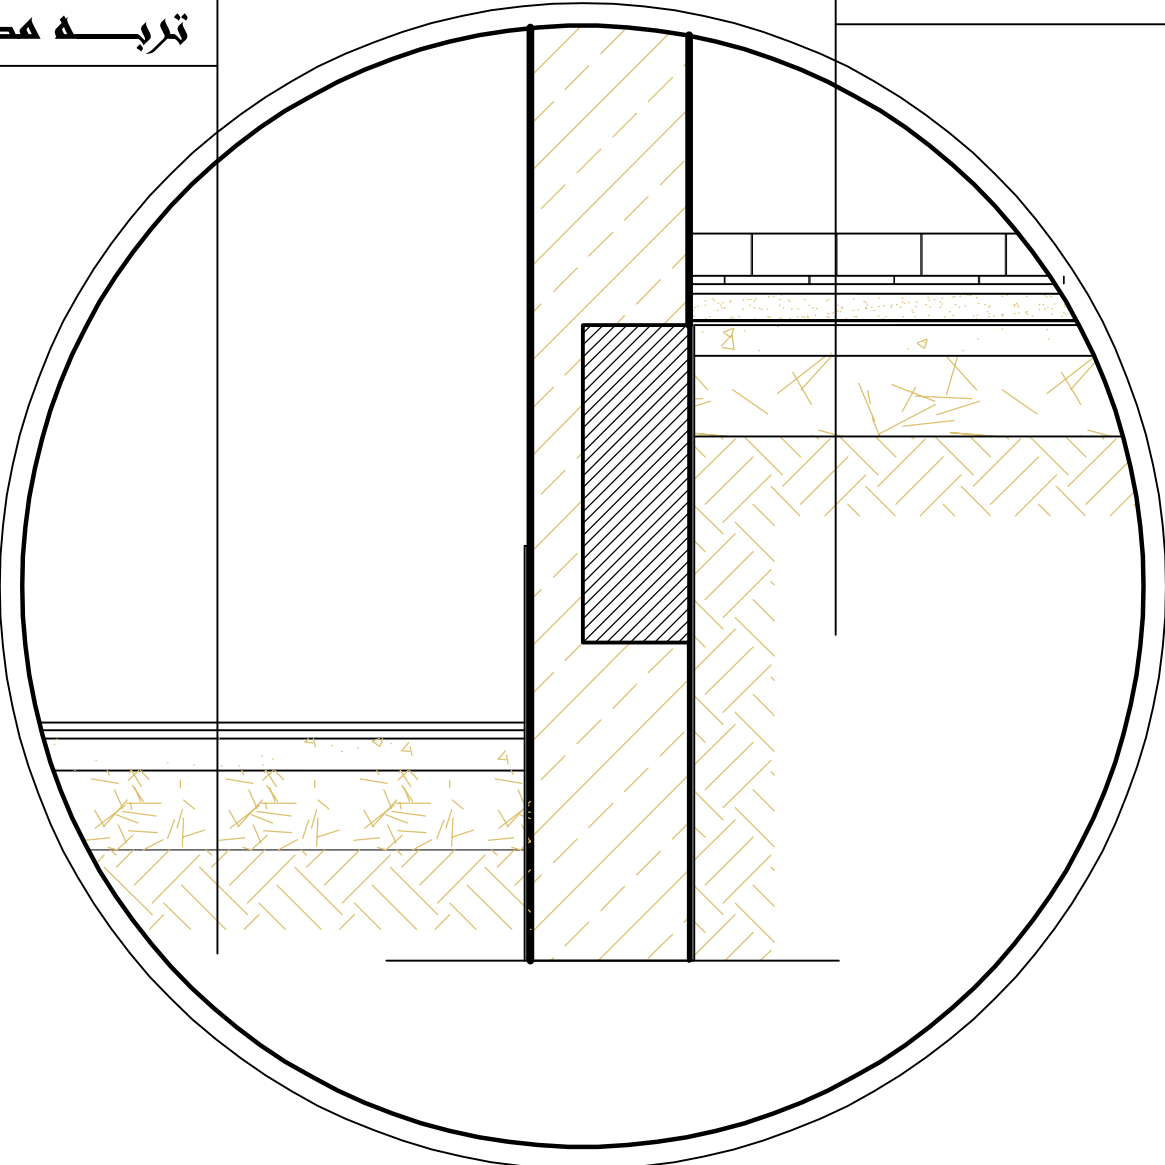

التفصيلة رقم 5
مقياس رسم 10/1

وزرة سيراميك 1*30*15 cm
بلاط سيراميك 0.5*20*20cm
مونه اسمنتية 2 cm
رمل تسويه 5 cm
عازل للرطوبة 2 mm
خرسانه عادية 15 cm
كسر حجر 15 cm
تربه مدكوكه

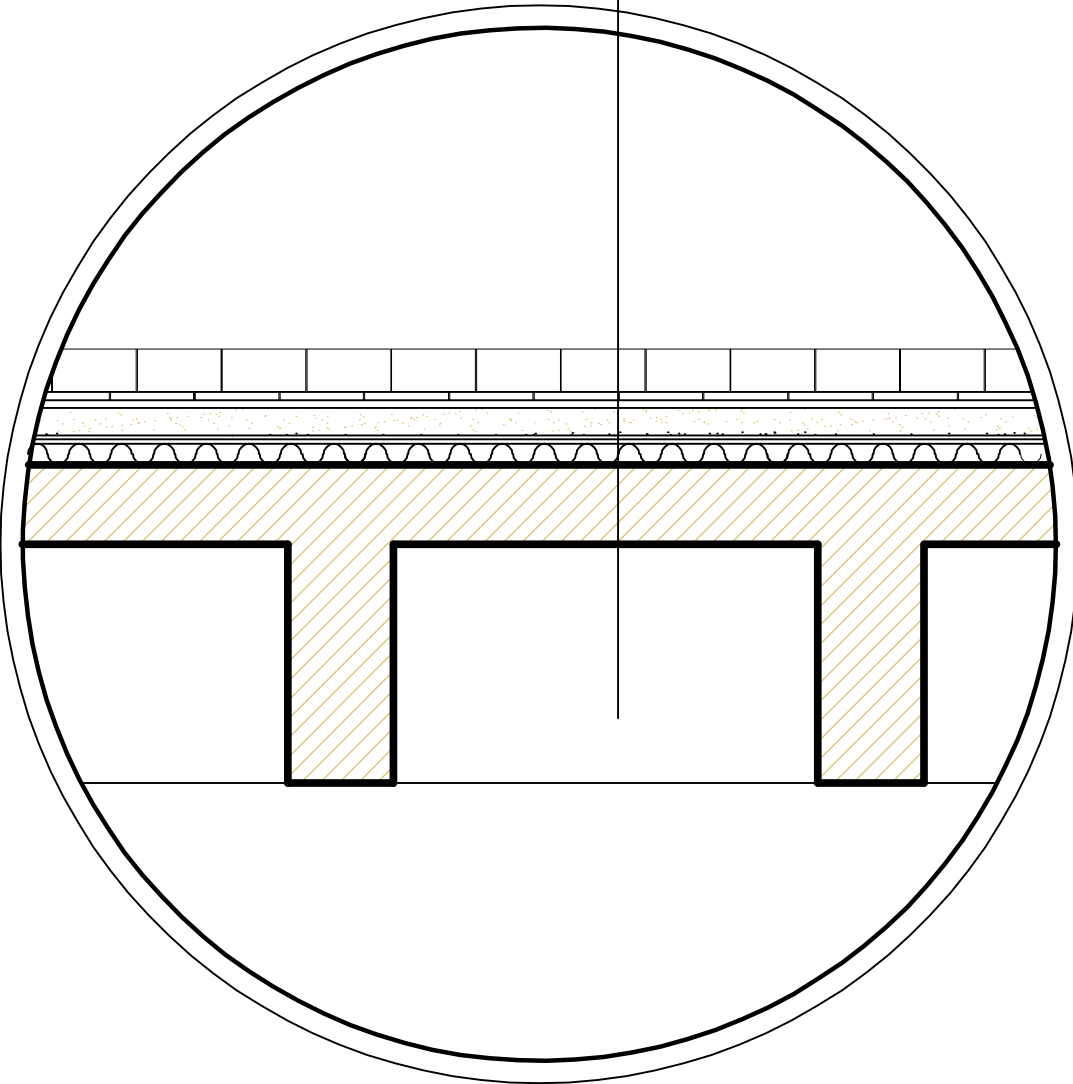

التفصيلة رقم 2
مقياس رسم 10/1

وزرة موزايكو 2*30*15 cm
بلاط موزايكو 2*25*25 cm
مونه اسمنتية 2 cm
رمل تسويه 5 cm
عازل للرطوبة 2 mm
عازل حرارة 5 cm
تسقيف شبكي 60 cm

- خرسانه مسلحة
- حجر
- بلك
- رمل
- خرسانه عادية
- كسر حجر
- تربه مدكوكه

تقديم	احمد عبدالاله دهمش		
اسم اللوحة	تفاصيل الغطاء	نوع اللوحة	تنفيذية
رقم اللوحة	A-8	مقياس الرسم	1:10
اشرافه	د. محمد الوهاب الخريفي م. اروي جباري م. حسام امين		