



قطعة رقم ١/٥٢٩

قطعة رقم ١/٥٣١ و ٢/٥٣١

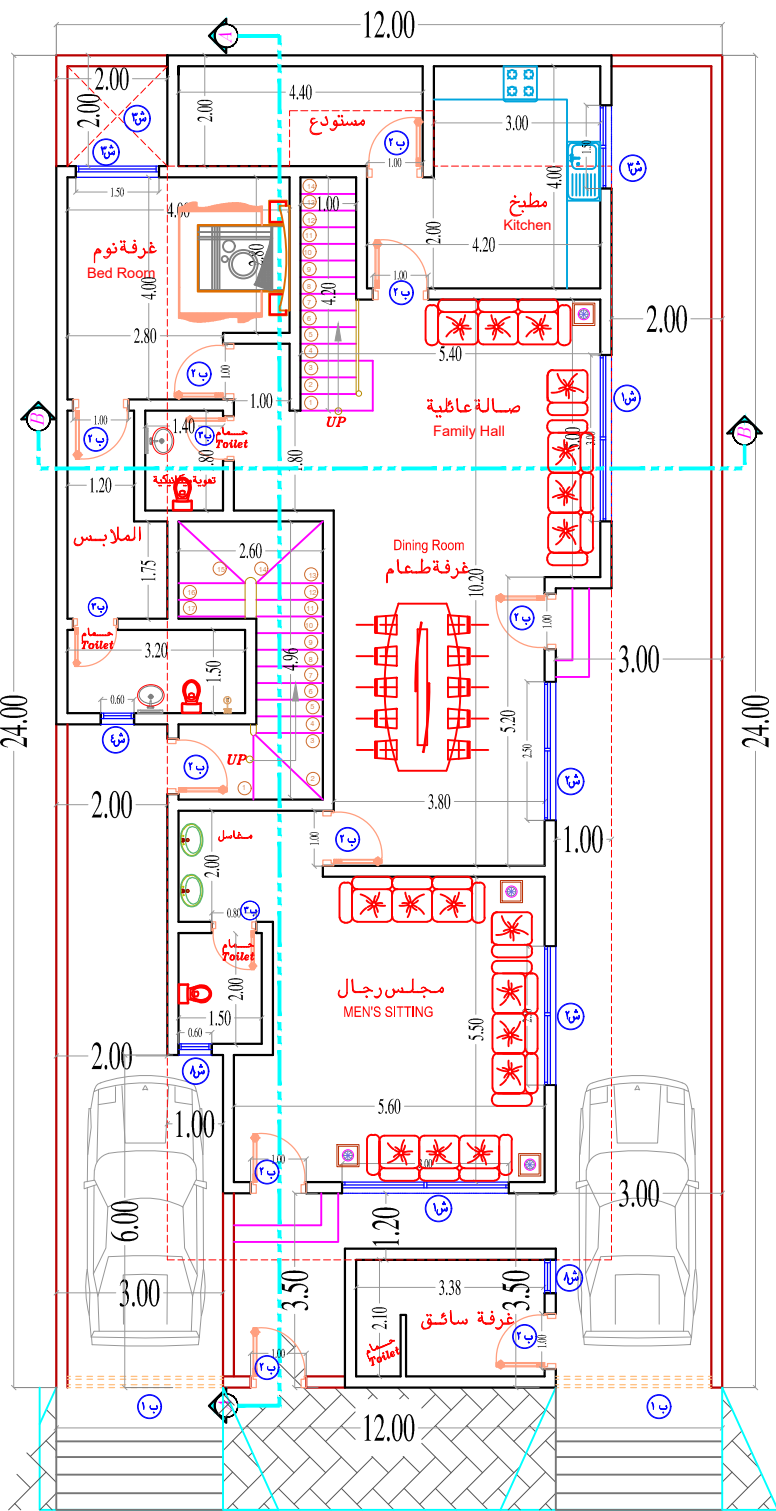


شارع عرض ١٢م

قطعة رقم ١/٥٣٢

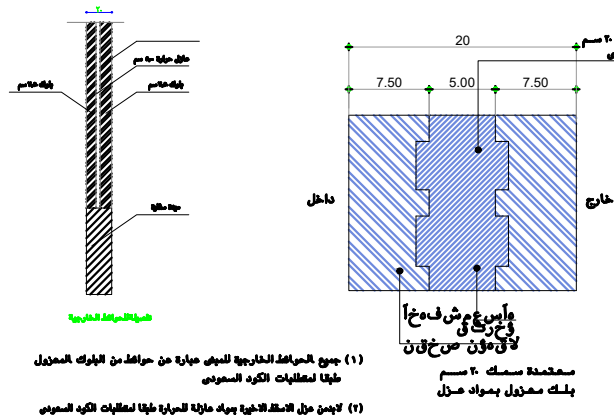

الشمال

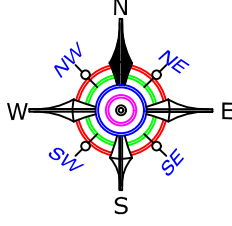

جدول فتحات ابواب

رقم نموذج	طول	عرض	ارتفاع الجلسة	التوصيف
ب ١	2.80	3.00	—	باب سيارة
رقم نموذج	طول	عرض	ارتفاع الجلسة	التوصيف
ب ٢	2.40	1.00	—	باب مدخل الدخول من غرفة واحدة من من الحديقة المشرفة مع لوكسان ٦م
رقم نموذج	طول	عرض	ارتفاع الجلسة	التوصيف
ب ٣	2.40	0.80	—	باب خشب سويده حشرات مسمومين يتحاشن مقامهم للزبانية

جدول فتحات الشبايك

رقم نموذج	طول	عرض	ارتفاع الجلسة	التوصيف
ش ١	2.40	3.00	0.40	شباك خفيف من قطعات الاسبستوم ملون فارغ زجاج مزدوج ملون عاكس بسبك ٦م
رقم نموذج	طول	عرض	ارتفاع الجلسة	التوصيف
ش ٢	2.40	2.50	0.40	شباك خفيف من قطعات الاسبستوم ملون فارغ زجاج مزدوج ملون عاكس بسبك ٦م
رقم نموذج	طول	عرض	ارتفاع الجلسة	التوصيف
ش ٣	2.40	1.50	0.40	شباك خفيف من قطعات الاسبستوم ملون فارغ زجاج مزدوج ملون عاكس بسبك ٦م
رقم نموذج	طول	عرض	ارتفاع الجلسة	التوصيف
ش ٤	2.40	0.60	0.40	شباك خفيفة واحد من قطعات الاسبستوم ملون فارغ زجاج مزدوج ملون عاكس بسبك ٦م
رقم نموذج	طول	عرض	ارتفاع الجلسة	التوصيف
ش ٥	1.80	3.00	1.20	شباك خفيفة واحد من قطعات الاسبستوم ملون فارغ زجاج مزدوج ملون عاكس بسبك ٦م
رقم نموذج	طول	عرض	ارتفاع الجلسة	التوصيف
ش ٦	1.80	1.50	1.20	شباك خفيفة واحد من قطعات الاسبستوم ملون فارغ زجاج مزدوج ملون عاكس بسبك ٦م
رقم نموذج	طول	عرض	ارتفاع الجلسة	التوصيف
ش ٧	1.80	0.80	1.20	شباك خفيفة واحد من قطعات الاسبستوم ملون فارغ زجاج مزدوج ملون عاكس بسبك ٦م
رقم نموذج	طول	عرض	ارتفاع الجلسة	التوصيف
ش ٨	1.80	0.60	1.20	شباك خفيفة واحد من قطعات الاسبستوم ملون فارغ زجاج مزدوج ملون عاكس بسبك ٦م

الدور الارضى