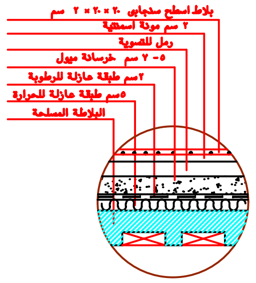

تفصيلة بلاطة السقف العلوى (٣)

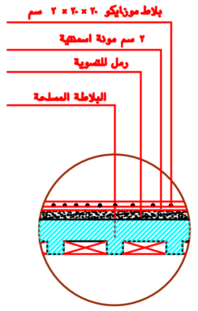

تفصيلة بلاطة سقف الارضى (٢)

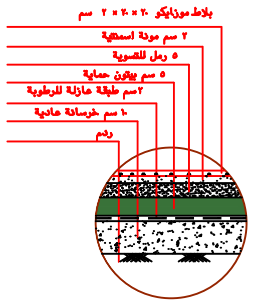

تفصيلة الارضيات (١)

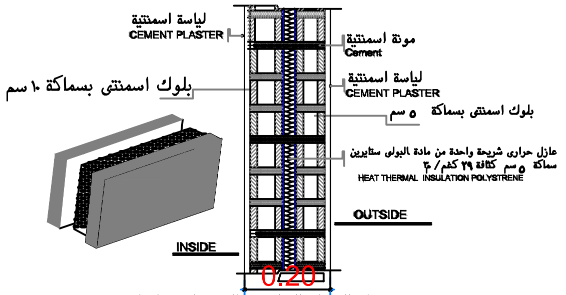

تفصيلة الجدار الخارجى المعزول حراريا
DETAIL OF THERMAL INSULATED
OUTSIDE WALL

تفصيلة توضح طريقة عزل الجدران

طبقا للكود السعودى الجديد-قسم ترشيد الطاقة
SBC 602

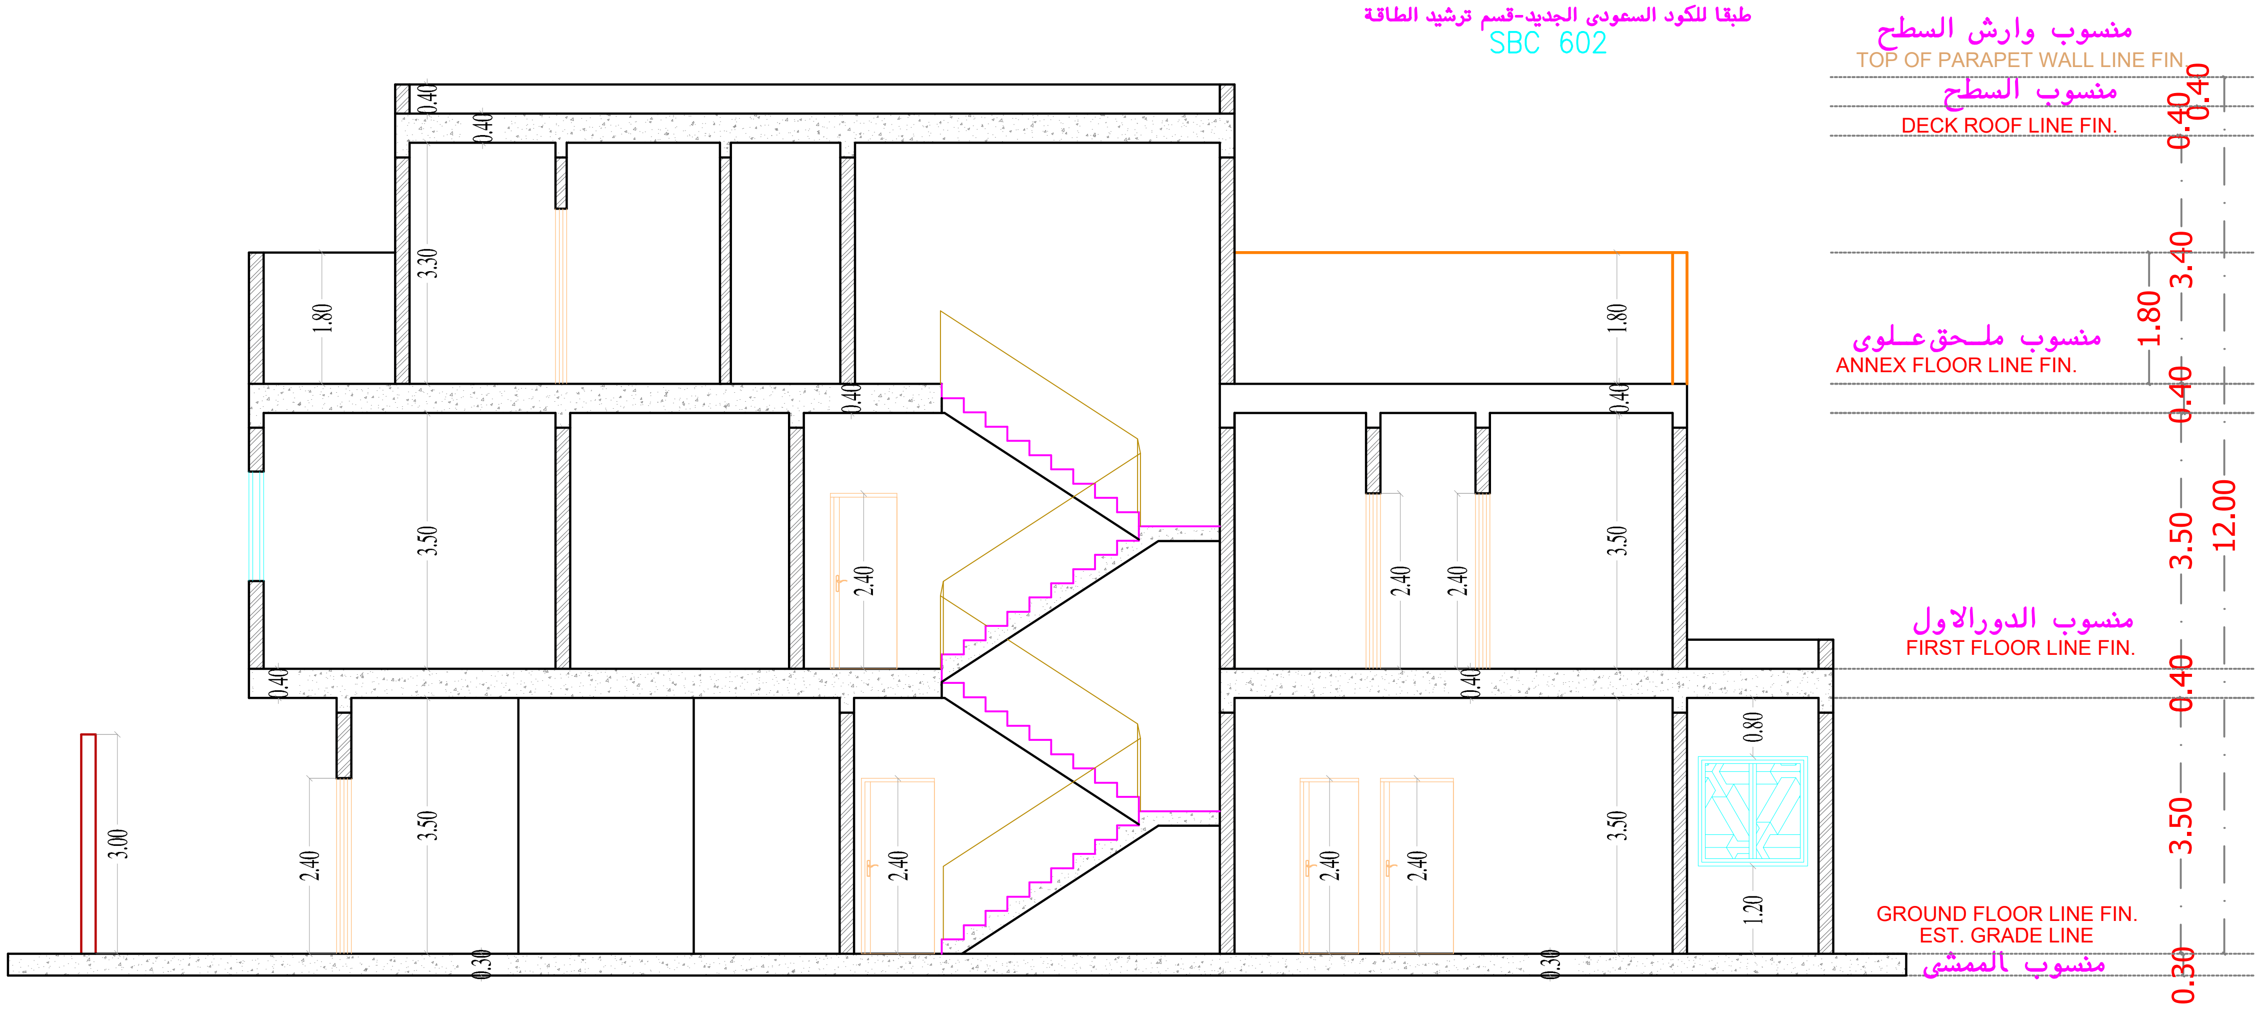

القطاع ١