


جدول الابواب				
نموذج	عرض	ارتفاع	جلسة	ملاحظات
ب ١	٣.٠٠	٢.٨٠	—	باب جراج سيارة
ب ٢	١.٦٠	٢.٨٠	—	باب حديد المدخل فيلا
ب ٣	١.٦٠	٢.٨٠	—	باب من الخشب الكيس درفة واحدة
ب ٤	١.٦٠	٢.٨٠	—	باب من الخشب الكيس درفة واحدة
ب ٥	١.٦٠	٢.٨٠	—	باب من الخشب الكيس درفة واحدة
ب ٦	١.٦٠	٢.٨٠	—	باب من الخشب الكيس درفة واحدة
ب ٧	١.٦٠	٢.٨٠	—	باب من الخشب الكيس درفة واحدة

جدول شبابيك				
نموذج	عرض	ارتفاع	جلسة	ملاحظات
ش ١	٢.٠٠	٣.٠٠	—	شباك من الالمنيوم
ش ٢	١.٥٠	٣.٠٠	—	شباك من الالمنيوم
ش ٣	١.٥٠	١.٤٠	—	شباك من الالمنيوم
ش ٤	١.٣٥	١.٤٠	—	شباك من الالمنيوم
ش ٥	١.٣٥	١.٤٠	—	شباك من الالمنيوم
ش ٦	١.٣٠	١.٤٠	—	شباك من الالمنيوم
ش ٧	١.٣٠	١.٤٠	—	شباك من الالمنيوم
ش ٨	١.٣٠	١.٤٠	—	شباك من الالمنيوم
ش ٩	١.٥٠	٢.٧٦	—	شباك من الالمنيوم

ملاحظات معماري

- تشطيب ارضيات المدخل والموزعات ترابيع رخام ٤٠x٤٠ سم
- تشطيب ارضيات الغرف و الصالات بلاط موازيكو كسر رخام ٦٠x٦٠ سم
- تشطيب ارضيات الحمامات و المطابخ بلاط سيراميك
- تشطيب حوائط الحمامات و المطابخ بلاط سيراميك
- الدرج من الرخام الاسود للقامة بسمك ٢ سم واللانة من الرخام الابيض بسمك ٣ سم
- درايزين السلم حديد كريتال مشطول
- جميع مقابض وكوالين الابواب من ماركة Yale الايطالية
- خزان المياه العلوي تعمل له فتحة طوية تقاس ٦٠x٦٠ سم وتغطي بطعام من الصاج

لمنظف المنزل و نظف على كرات نظيفة معلقة وضادامادة المبيكة المانعة للزحف والرطوبة

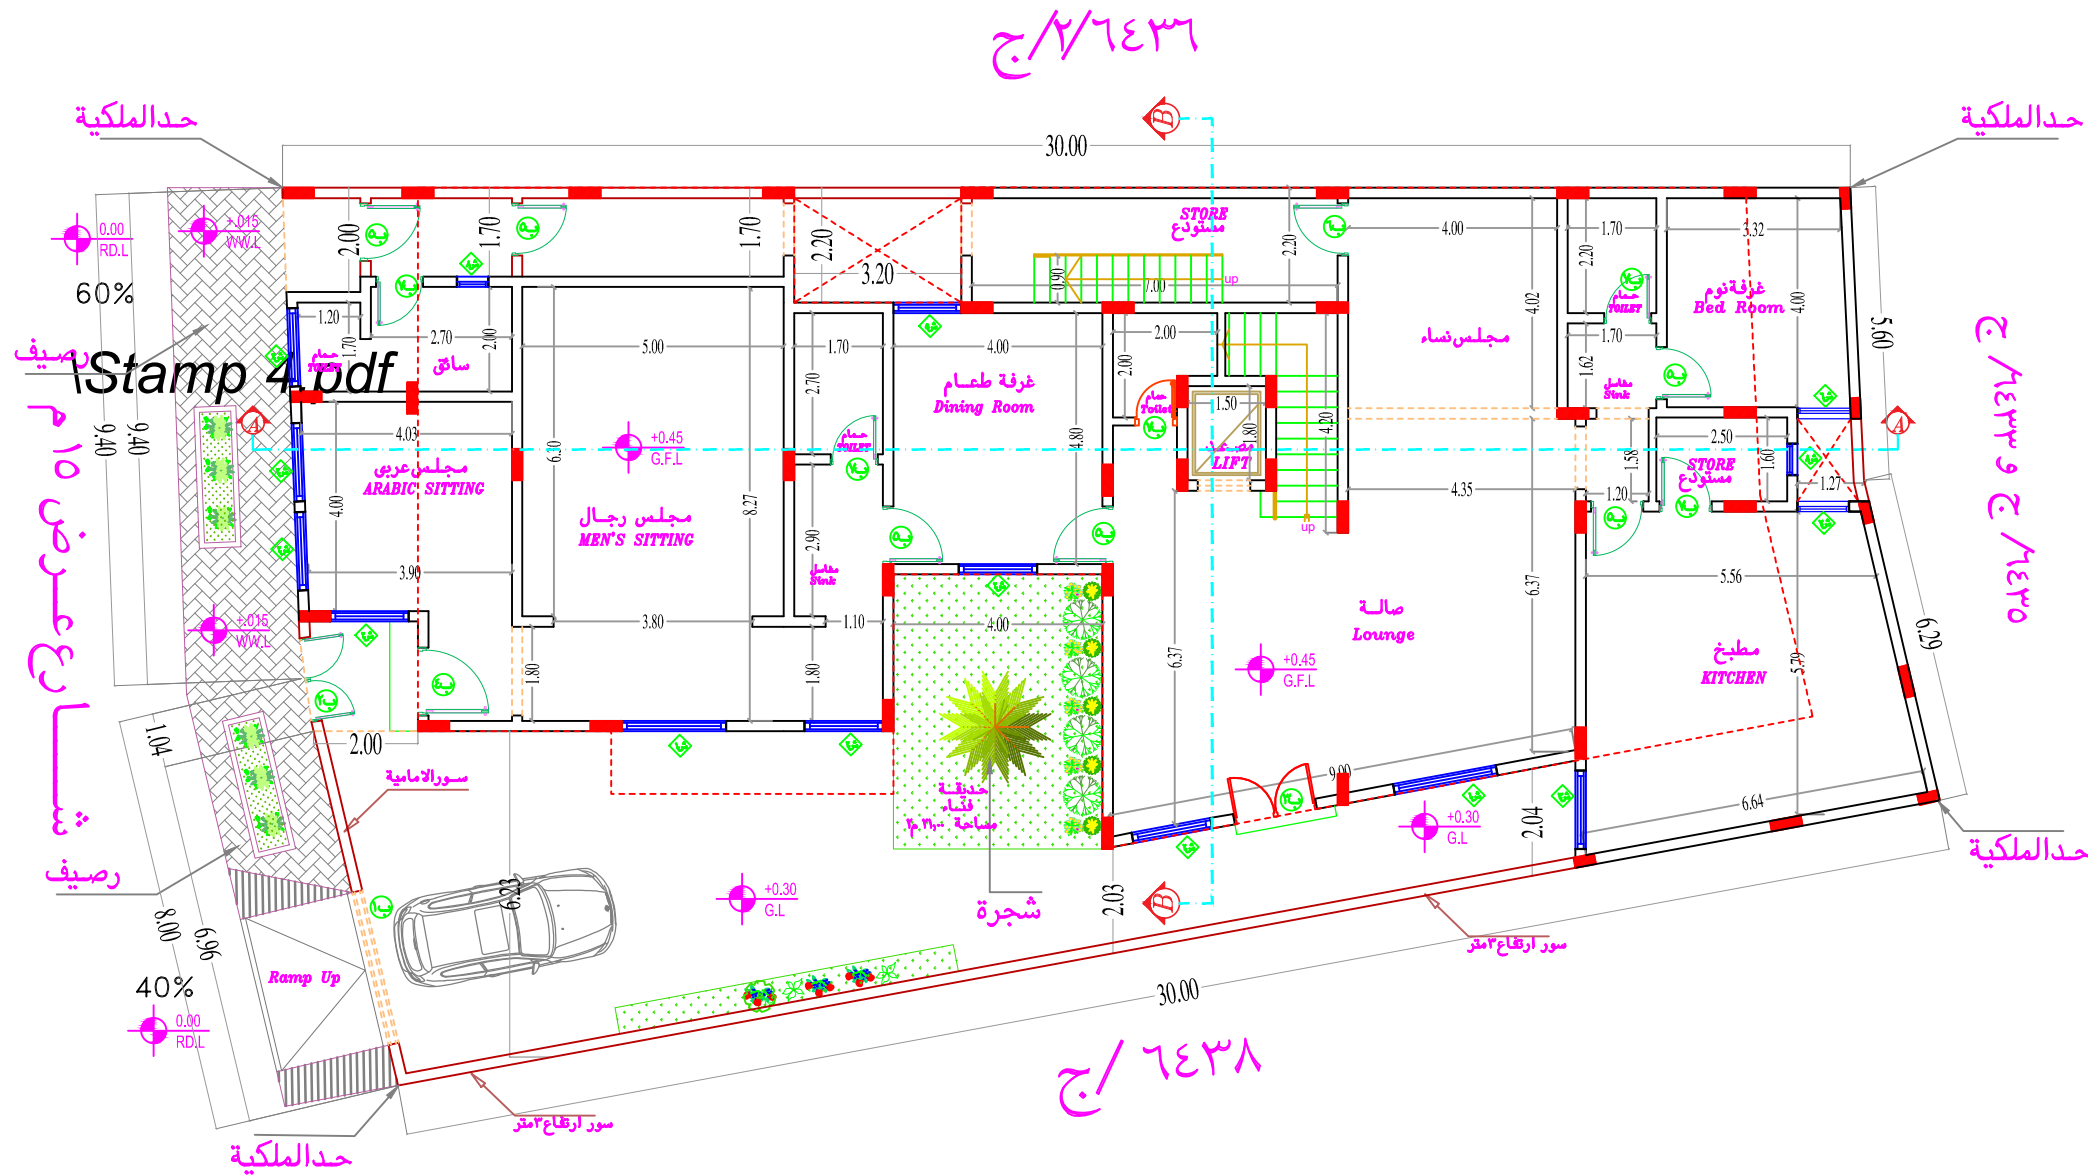

الدور الارضى