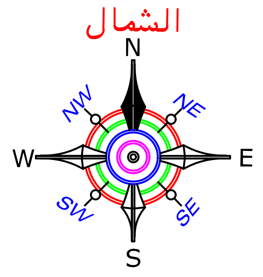

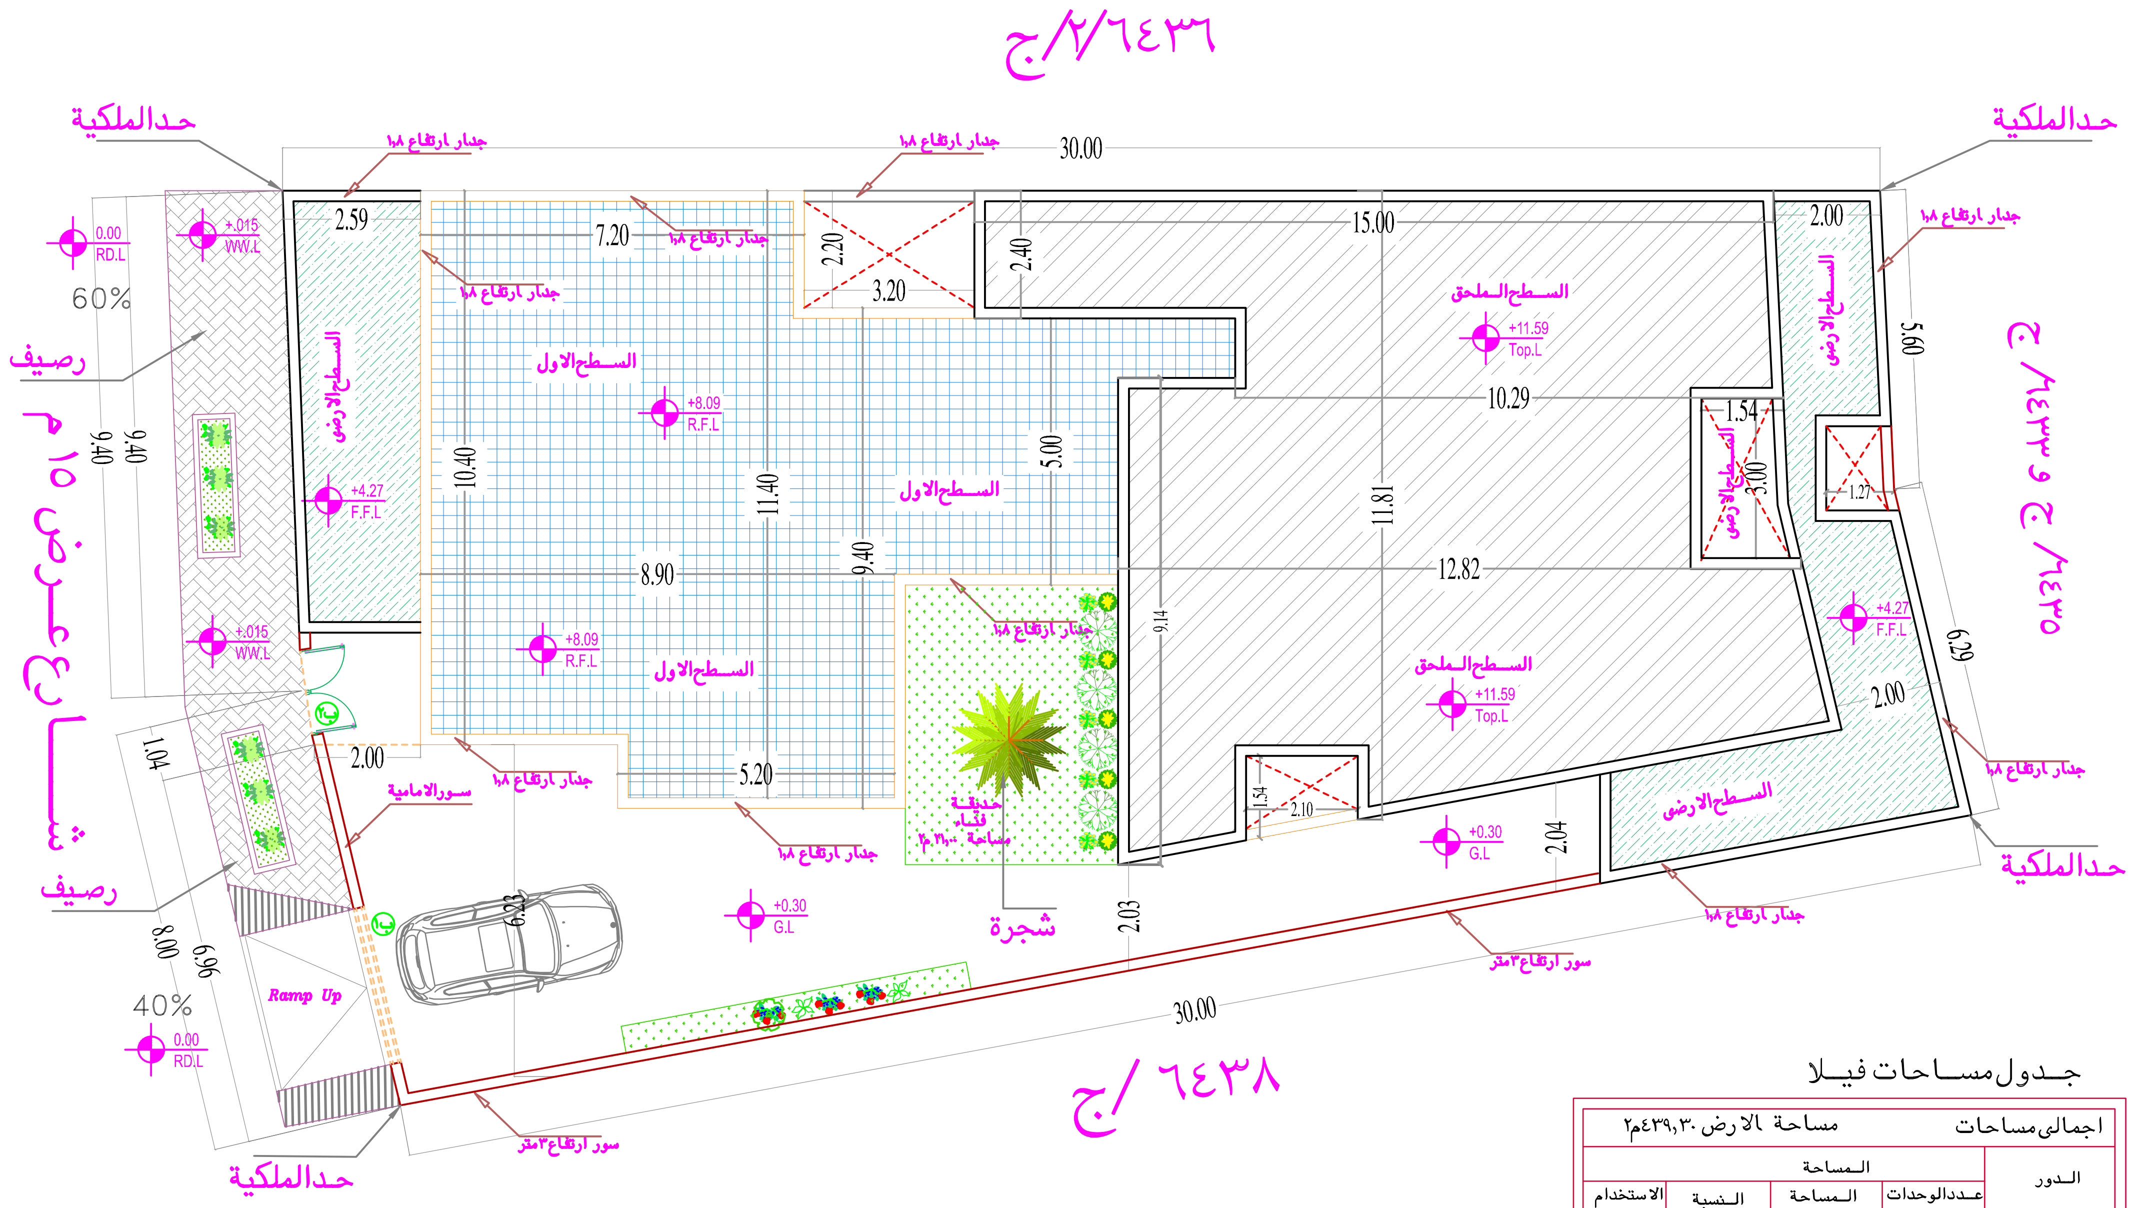

جدول مساحات فيلا

اجمالى مساحات	مساحة الارض ٤٣٩٫٣٠م٢			
الدور	المساحة			
	عددالوحدات	المساحة	النسبة	الاستخدام
الدورالارضى	١	٢٩٨٫٥٠ م٢	٦٧٫٧٤ ٪	سكنى
الدورالاول	.	٢٦٦٫٠٠ م٢	٦١٫٥٠ ٪	سكنى
الدورالملحق	.	١٣٣٫٠٠ م٢	٥٠٪من الاول	سكنى
الاسوار ٨٩٫٣٠ مط	كمية الحفر ٦٦١٫٠٠م٣			

جدول ارتدادات

الجهة	شمال	جنوب	شرق	غرب
الابعاد	٣٠٫٠٠م	٣٠٫٠٠م	١١٫٨٩م	١٧٫٤٠ م
الارتداد	٠٫٠٠م	٢٫٠٣م	٢٫٠٠م	٢٫٠٠م
الجار	ج/٢/٦٤٣٦	٦٤٣٨ /ج	٦٤٣٥/ ج و ٦٤٣٣/ ج	شارع عرض ١٥ م

الموقع العام