


جدول الابواب			
نموذج	عرض	ارتفاع	ملاحظات
ب ١	٣,٠٠	٢,٨٠	باب جراج سيارة
ب ٢	١,٦٠	٢,٨٠	باب حديد المدخل فيلا
ب ٣	١,٦٠	٢,٨٠	باب من الخشب الكيس درفة واحدة
ب ٤	١,٦٠	٢,٨٠	باب من الخشب الكيس درفة واحدة
ب ٥	١,٦٠	٢,٤٠	باب من الخشب الكيس درفة واحدة
ب ٦	١,٠٠	٢,٤٠	باب من الخشب الكيس درفة واحدة
ب ٧	٩٠	٢,٤٠	باب من الخشب الكيس درفة واحدة

جدول شيايبك			
نموذج	عرض	ارتفاع	ملاحظات
ش ١	٢,٠٠	٣,٠٠	شباك من الالمنيوم
ش ٢	١,٥٠	٣,٠٠	شباك من الالمنيوم
ش ٣	١,٥٠	١,٤٠	شباك من الالمنيوم
ش ٤	١,٣٥	١,٤٠	شباك من الالمنيوم
ش ٥	١,٣٠	١,٤٠	شباك من الالمنيوم
ش ٦	١,٠٠	١,٤٠	شباك من الالمنيوم
ش ٧	١,٠٠	١,٤٠	شباك من الالمنيوم
ش ٨	٦٠	١,٤٠	شباك من الالمنيوم
ش ٩	١,٥٠	٢,٦٦	شباك من الالمنيوم

ملاحظات معمارية
(١) تشطيب ارضيات المدخل والموزعات ترابيع رخام ٤٠×٤٠ سم
(٢) تشطيب ارضيات الغرف و الصالات بلاط موزاييك كبر رخام ٦٠×٦٠ سم
(٣) تشطيب ارضيات الحمامات و المطابخ بلاط سيراميك
(٤) تشطيب حواضد الحمامات و المطابخ بلاط سيراميك
(٥) الدرج من الرخام الاسود للقامة بسك ٢ سم والنافذة من الرخام الابيض بسك ٢ سم
(٦) درابزين المسلم حديد كريبتال مشغول
(٧) جميع مقايض وكوالين الابواب من ماركة : itale : الايطالية
(٨) خزان المياه العلوي متصل لة فتحة علوية مقاس ٦٠×٦٠ سم وتغطي بغطاء من الصاج
ليطلق المزيج و تنفذ على كرات مطرية سلمة وضائفة السكة العامة للترنج والرطوبة

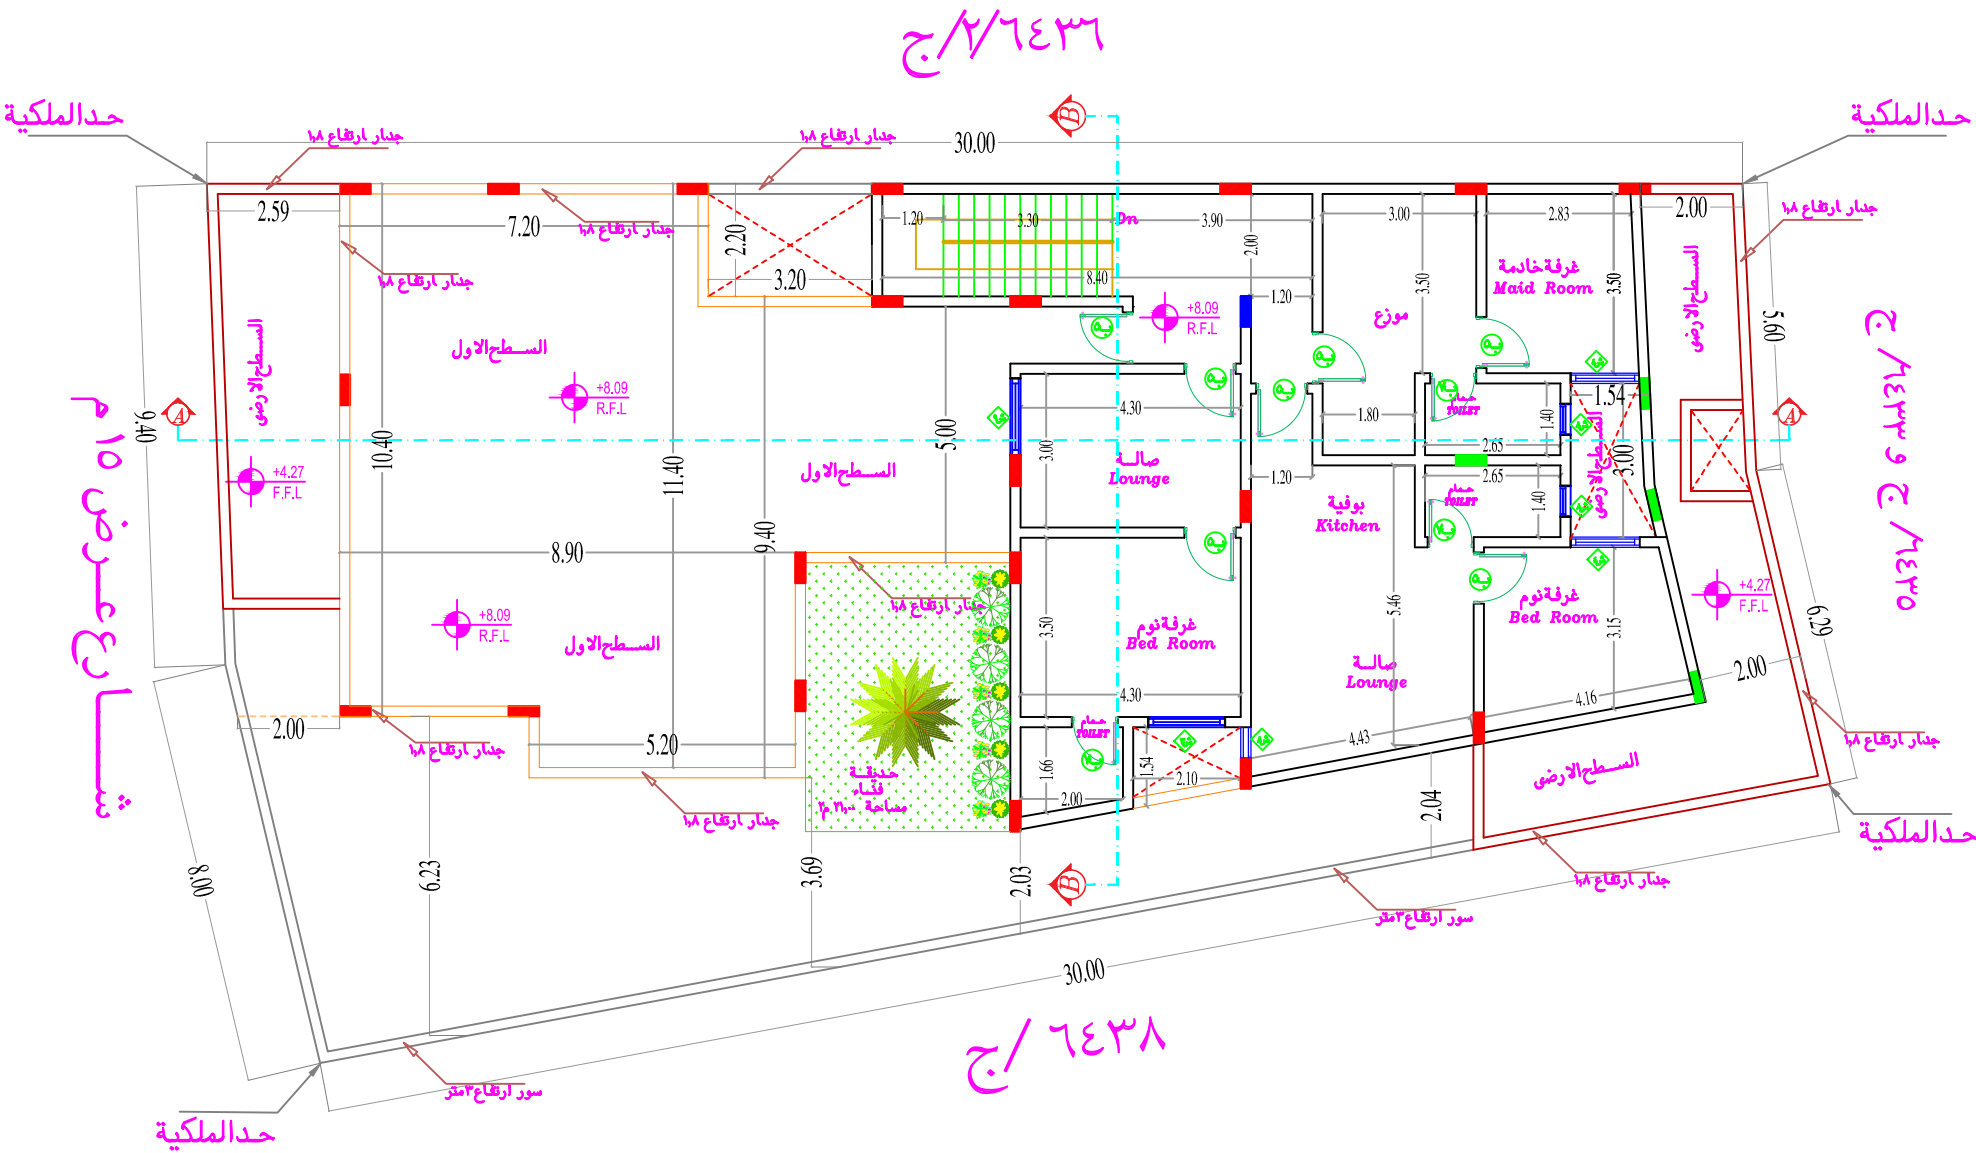

الدور الملحق