


جدول الابواب				
نموذج	عرض	ارتفاع	جلسة	ملاحظات
ب ١	٣,٠٠	٢,٨٠	—	باب جراج سيارة
ب ٢	١,٦٠	٢,٨٠	—	باب حديد المدخل فيلا
ب ٣	١,٦٠	٢,٨٠	—	باب من الخشب الكيس درفة واحدة
ب ٤	١,٣٠	٢,٨٠	—	باب من الخشب الكيس درفة واحدة
ب ٥	١,٦٠	٢,٤٠	—	باب من الخشب الكيس درفة واحدة
ب ٦	١,٣٠	٢,٤٠	—	باب من الخشب الكيس درفة واحدة
ب ٧	١,٩٠	٢,٤٠	—	باب من الخشب الكيس درفة واحدة

جدول شبابيك				
نموذج	عرض	ارتفاع	جلسة	ملاحظات
ش ١	٢,٣٠	٣,٠٠	١,٥٠	شباك من الالمنيوم
ش ٢	١,٥٠	٣,٠٠	١,٥٠	شباك من الالمنيوم
ش ٣	١,٥٠	١,٤٠	١,٢٠	شباك من الالمنيوم
ش ٤	١,٣٥	١,٤٠	١,٢٠	شباك من الالمنيوم
ش ٥	١,٣٠	١,٤٠	١,٢٠	شباك من الالمنيوم
ش ٦	١,٣٠	١,٤٠	١,٢٠	شباك من الالمنيوم
ش ٧	١,٣٠	١,٤٠	١,٢٠	شباك من الالمنيوم
ش ٨	١,٦٠	١,٤٠	١,٢٠	شباك من الالمنيوم
ش ٩	١,٥٠	٢,٦٦	١,٥٠	شباك من الالمنيوم

ملاحظات معماري
(١) تشطيب ارضيات المدخل والموزعات ترابيع رخام ٤٠x٤٠ سم
(٢) تشطيب ارضيات الغرف و الصالات بلاط موازيكو كسر رخام ٢٠x٢٠ سم
(٣) تشطيب ارضيات الحمامات و المطابخ بلاط سيراميك
(٤) تشطيب حواضد الحمامات و المطابخ بلاط سيراميك
(٥) الدرج من الرخام الاسود للنافه بسك ٢ سم والنافه من الرخام الابيض سمك ٣ سم
(٦) درابزين المسلم حديد كريتال مشغول
(٧) جميع مقابض وكوابل الابواب من ماركة Yale الايطالية
(٨) خزان المياه العلوي متصل لة فتحة علوية بمقاس ١٠٠ سم وتغطي بغطاء من الصاج
لمبائن المزوج و تنجز على كرات ملونة مملحة وضالمامة اليك المانعة للرشح والرطوبة

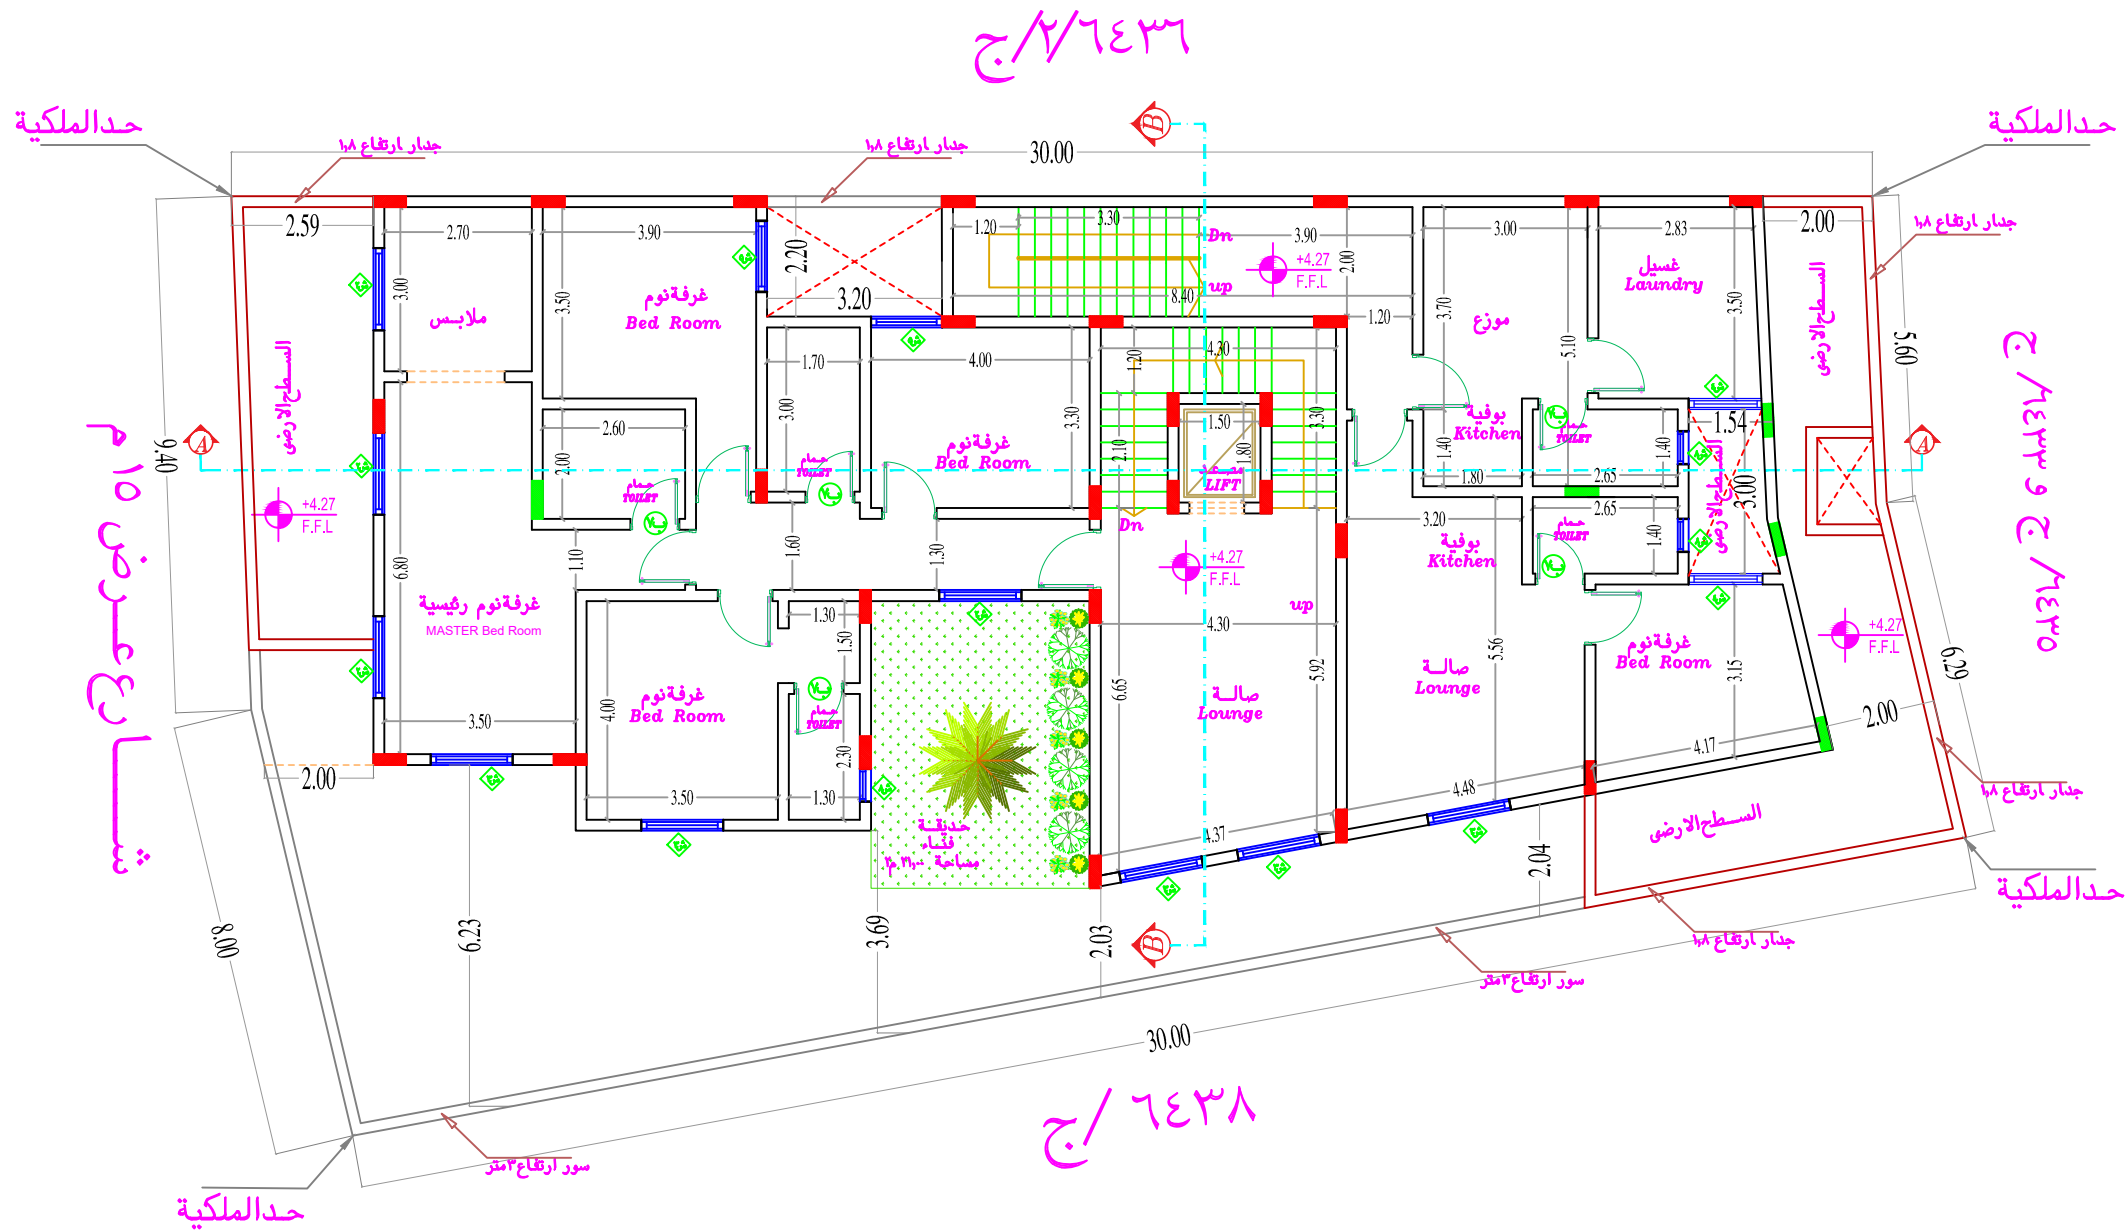

الدور الاول