

مكتب تمكين للهندسة
والمقاولات

T- 773977786 - 771017677 -

تصاميم واستشارات هندسية - مقاولات - حساب كميات -
رفع مساحي - ثري دي - تحليل حضري .

جدول التفصيلات
للواحيات الخارجية

الرمز	البيانات
1	حجر بيضاء جوفي مرقوم مع
2	مبسم كسب عطلين 2سم كل سدر عين
3	حجر بيضاء جوفي بدون رافه
4	حجر تحت ليزر مفرغ
5	تريزون حجر البض جوفي
6	المساقه بينهن 25 سم
7	حجر موش كامل
8	ترابزين اسفل وزجاج
9	نوافذ المنبوع وزجاج

تم اضافته عناصر جديده للواجهه في المخططات التنفيذيه وهي
غير موجوده في المخططات السابقه وذلك بتم اعتماد بشكل رئيسي
على المخططات التنفيذيه وتعليمات المهندس المعماري

المخططات التنفيذيه

المالك
الاخ / جبران المخرفي

المشروع
فيلا سكنيه


اسم الوحه
الواجهه الرئيسيه


تصميم

م/ عبد الله بينون
م/ نوح القاضي
م/ عبدالرحمن المغربي

معماري

التاريخ
الموافق الرسم
رقم الورقة

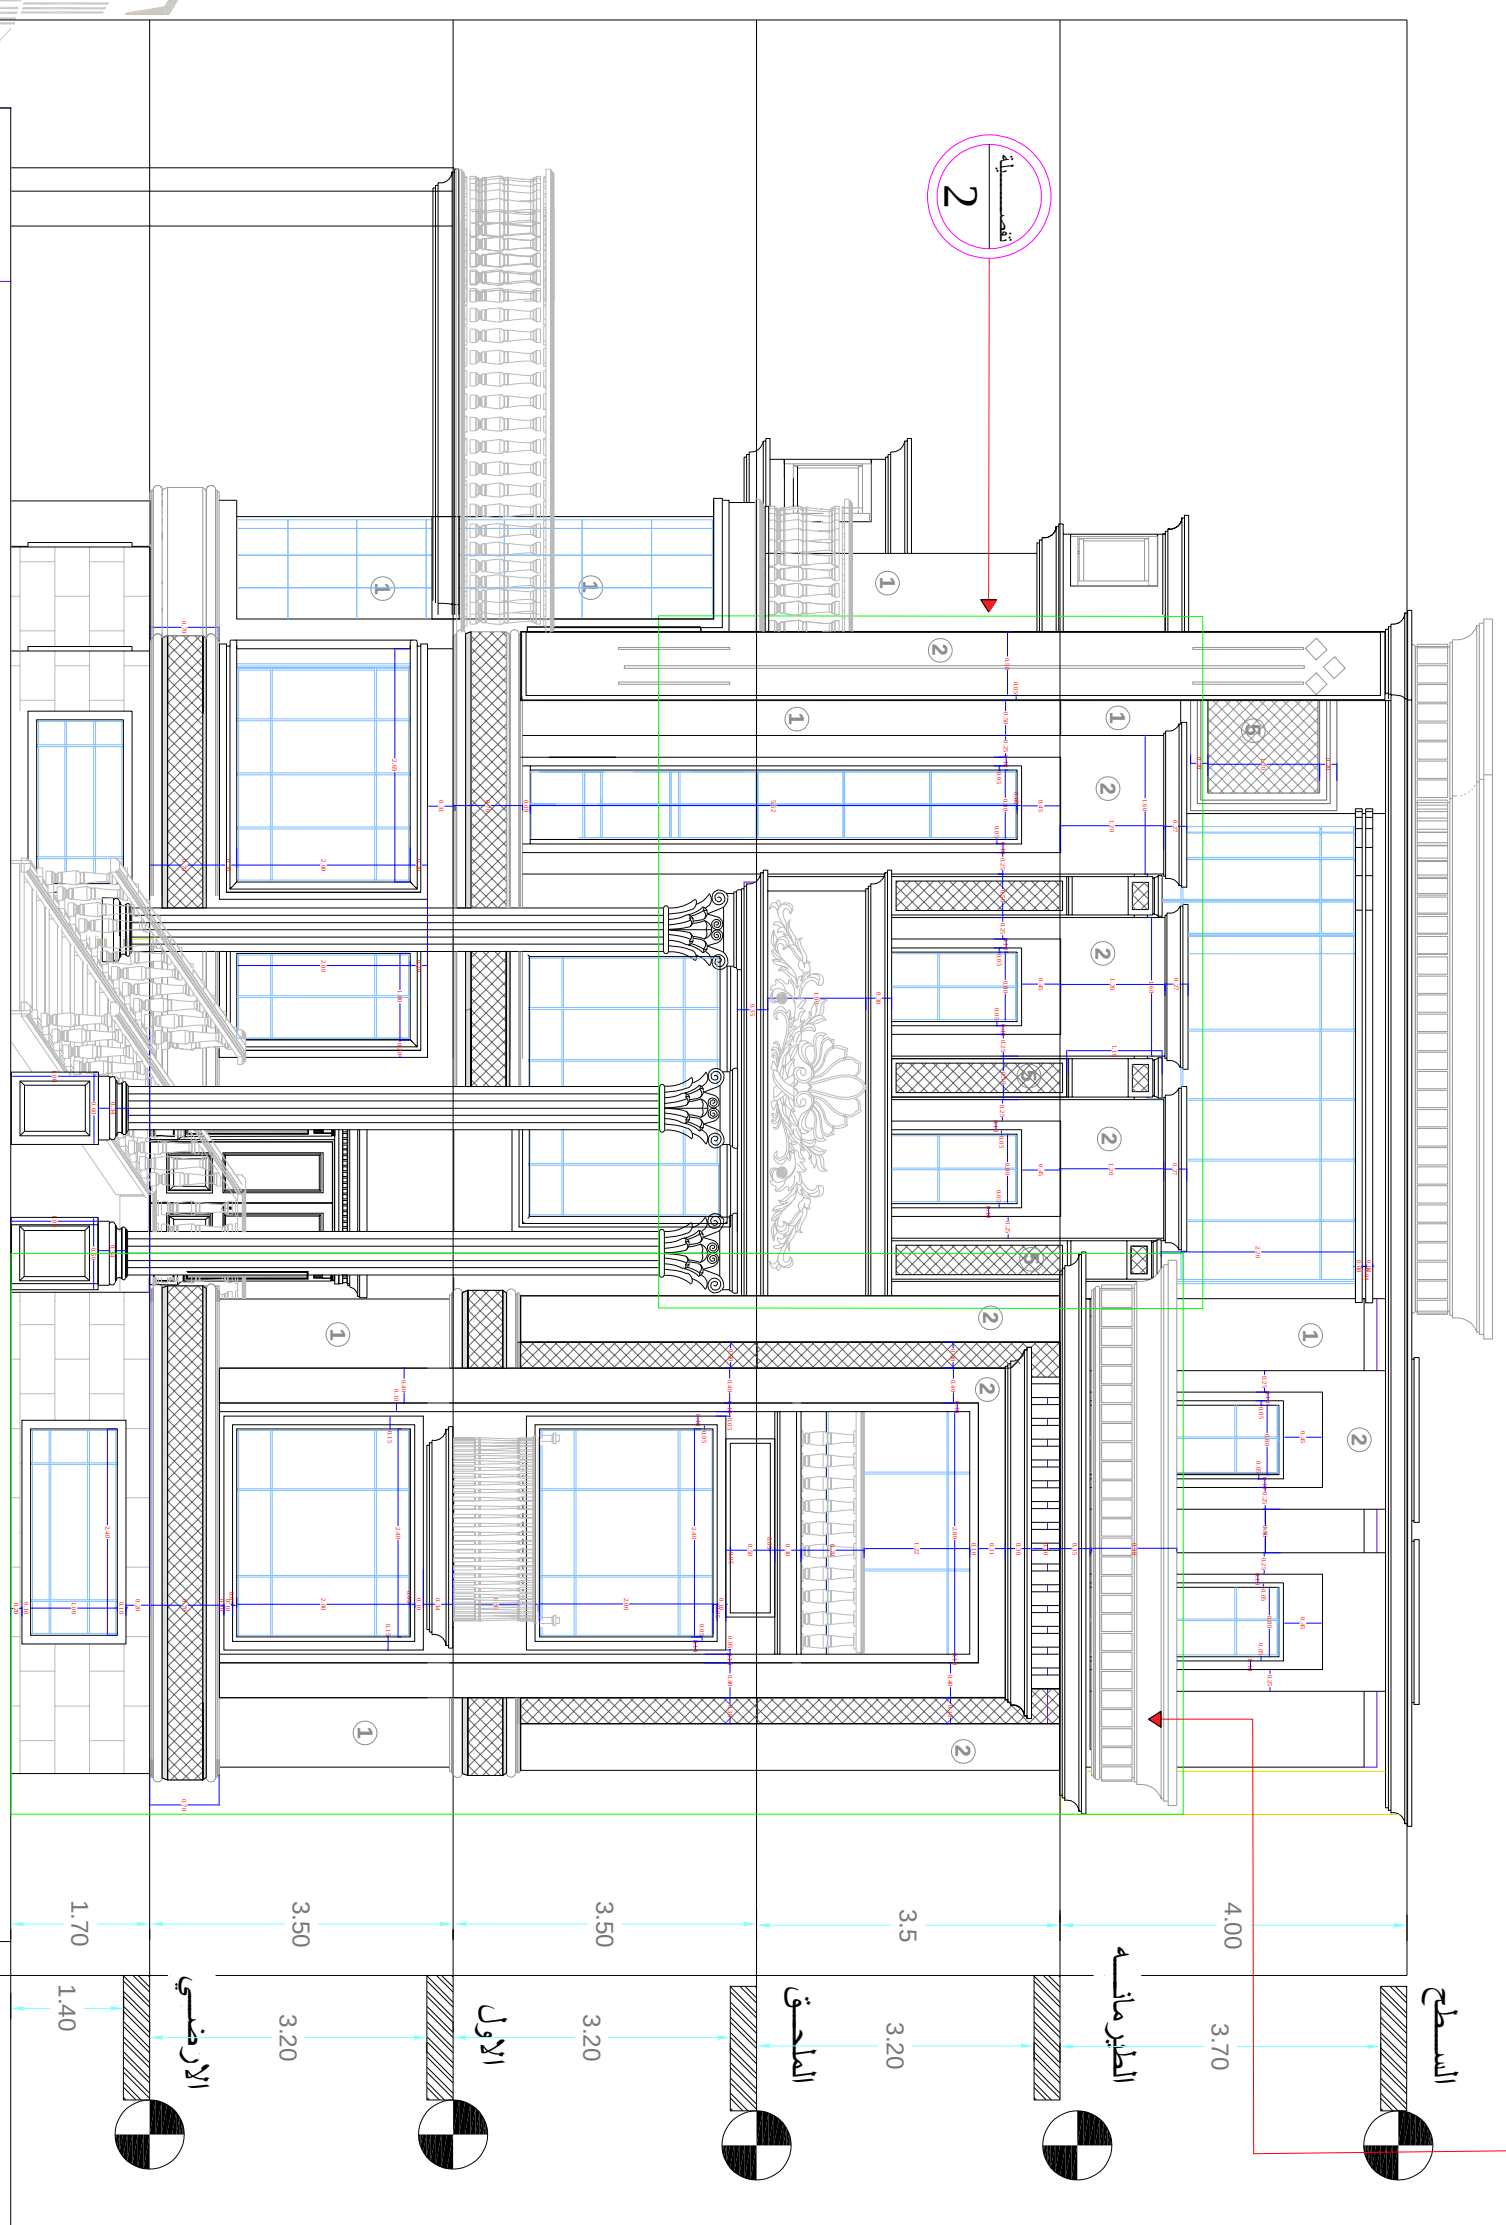

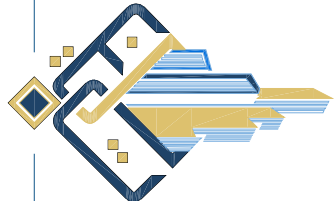

مكتب تمكين للهندسة والمقاولات

T- 773977786 - 771017677 -

نصمناهم واستشاراتهم هندسية - مقاولات - حساب كميات - رفع مساحي - شري دي - تخطيط حضري .

جدول التشطيبات للواجهات الخارجية

الرمز	البيانات
1	حجر بيضاء جوفي مرقم مع مجسم كسب غاطس كسب كل مسرعين
2	حجر بيضاء جوفي بدون رقمه
3	حجر نحت ليزر مفرج
4	لر بنزين حجر البض جوفي المسطحة بيضاء 25 سم
5	حجر مبرش كامل
6	لر بنزين اسفل زجاج
7	نوافذ المنبرم زجاج
8	

تم إضافة علفهم جديده للواجهه في المخططات التنفيذيه وهي غير موجوده في اليناظر ولذلك يتم اعتماد بشكل رئيسي على المخططات التنفيذيه وتعليمات المهندسين المعممين.

المخططات التنفيذيه

المالك
الاخ / جبران المخرفي

المشروع
فيلا سكنيه

اسم الوجهه
الواجهه الجانبيه الشرقيه

نصمهم
معماري
د/ عبد الله بينون
م/ نوح القاضي
د/ عبد الرحمن المغربي

التاريخ
مجلس الرس
التم الموجه

